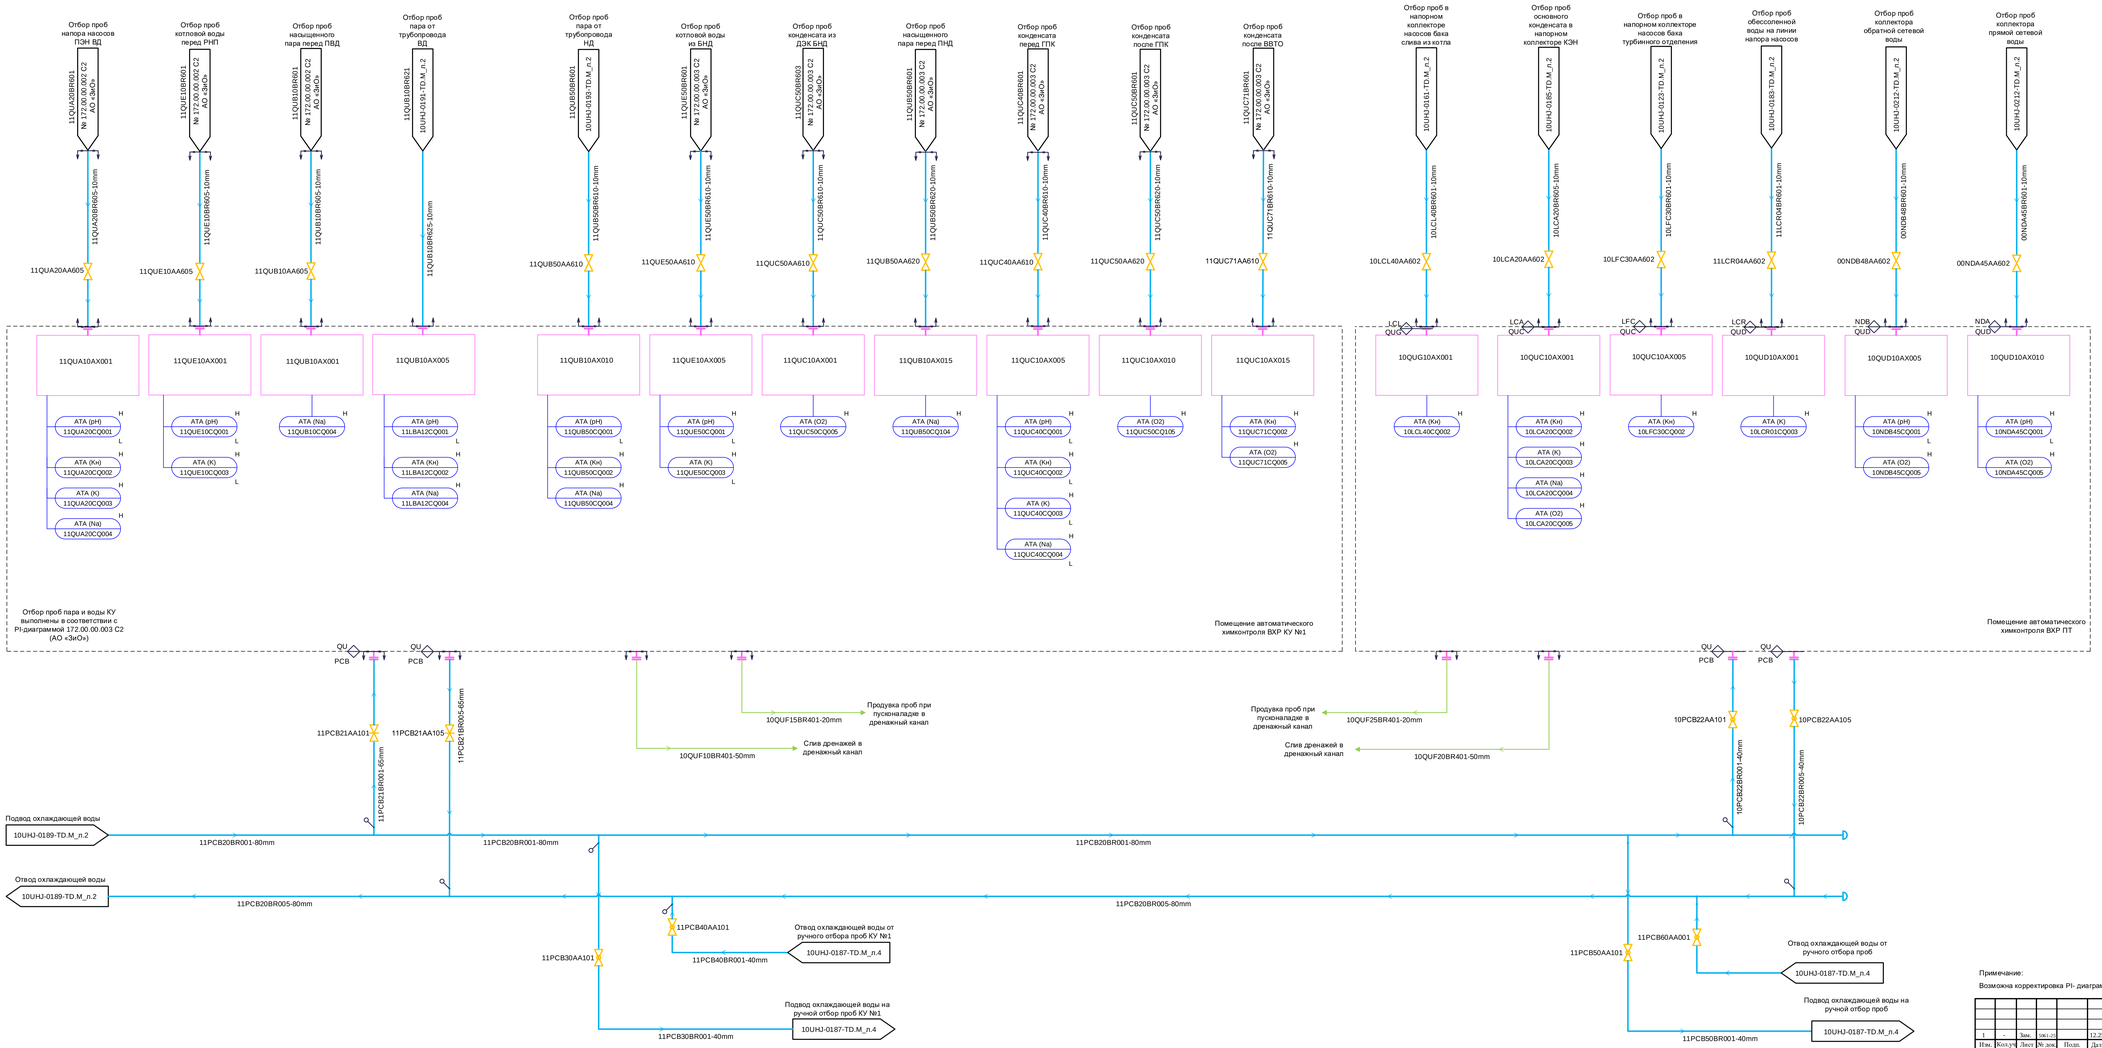

Примечание:

Возможна корректировка PI- диаграммы после получения ИД от поставщика оборудования

1	-	Зам.	5061-25		12.25	261N1 – 10UHJ – 0187 – TD.M
Изм.	Кол.уч.	Лист	№ док.	Подп.	Дата	Южно-Якутская ТЭС. Рабочая документация

Разработал	Евстифеев			Главный корпус. PI-диаграмма трубопроводов отбора проб пара и воды.	Стадия: Р; Лист: 2; Листов:
Проверил	Ляпрасова				
Гл. спец.	Сергеева				
Н. контр.	Черемушкина			PI-диаграммы трубопроводов отбора проб пара и воды КУ №1 в обвязывающей части. Система PCB, QUB, QUC, QUE, QUA, LBA, LCA, LFC, LCL, NDF, LCP, NDB, NDB.	АКЦИОНЕРНОЕ ОБЩЕСТВО «ТЕХНОПРОМЭКСПОРТ»

Согласовано

ОАО"У

Взам. инв. №

Подпись и дата

Инв. № подл.

Формат А2х3