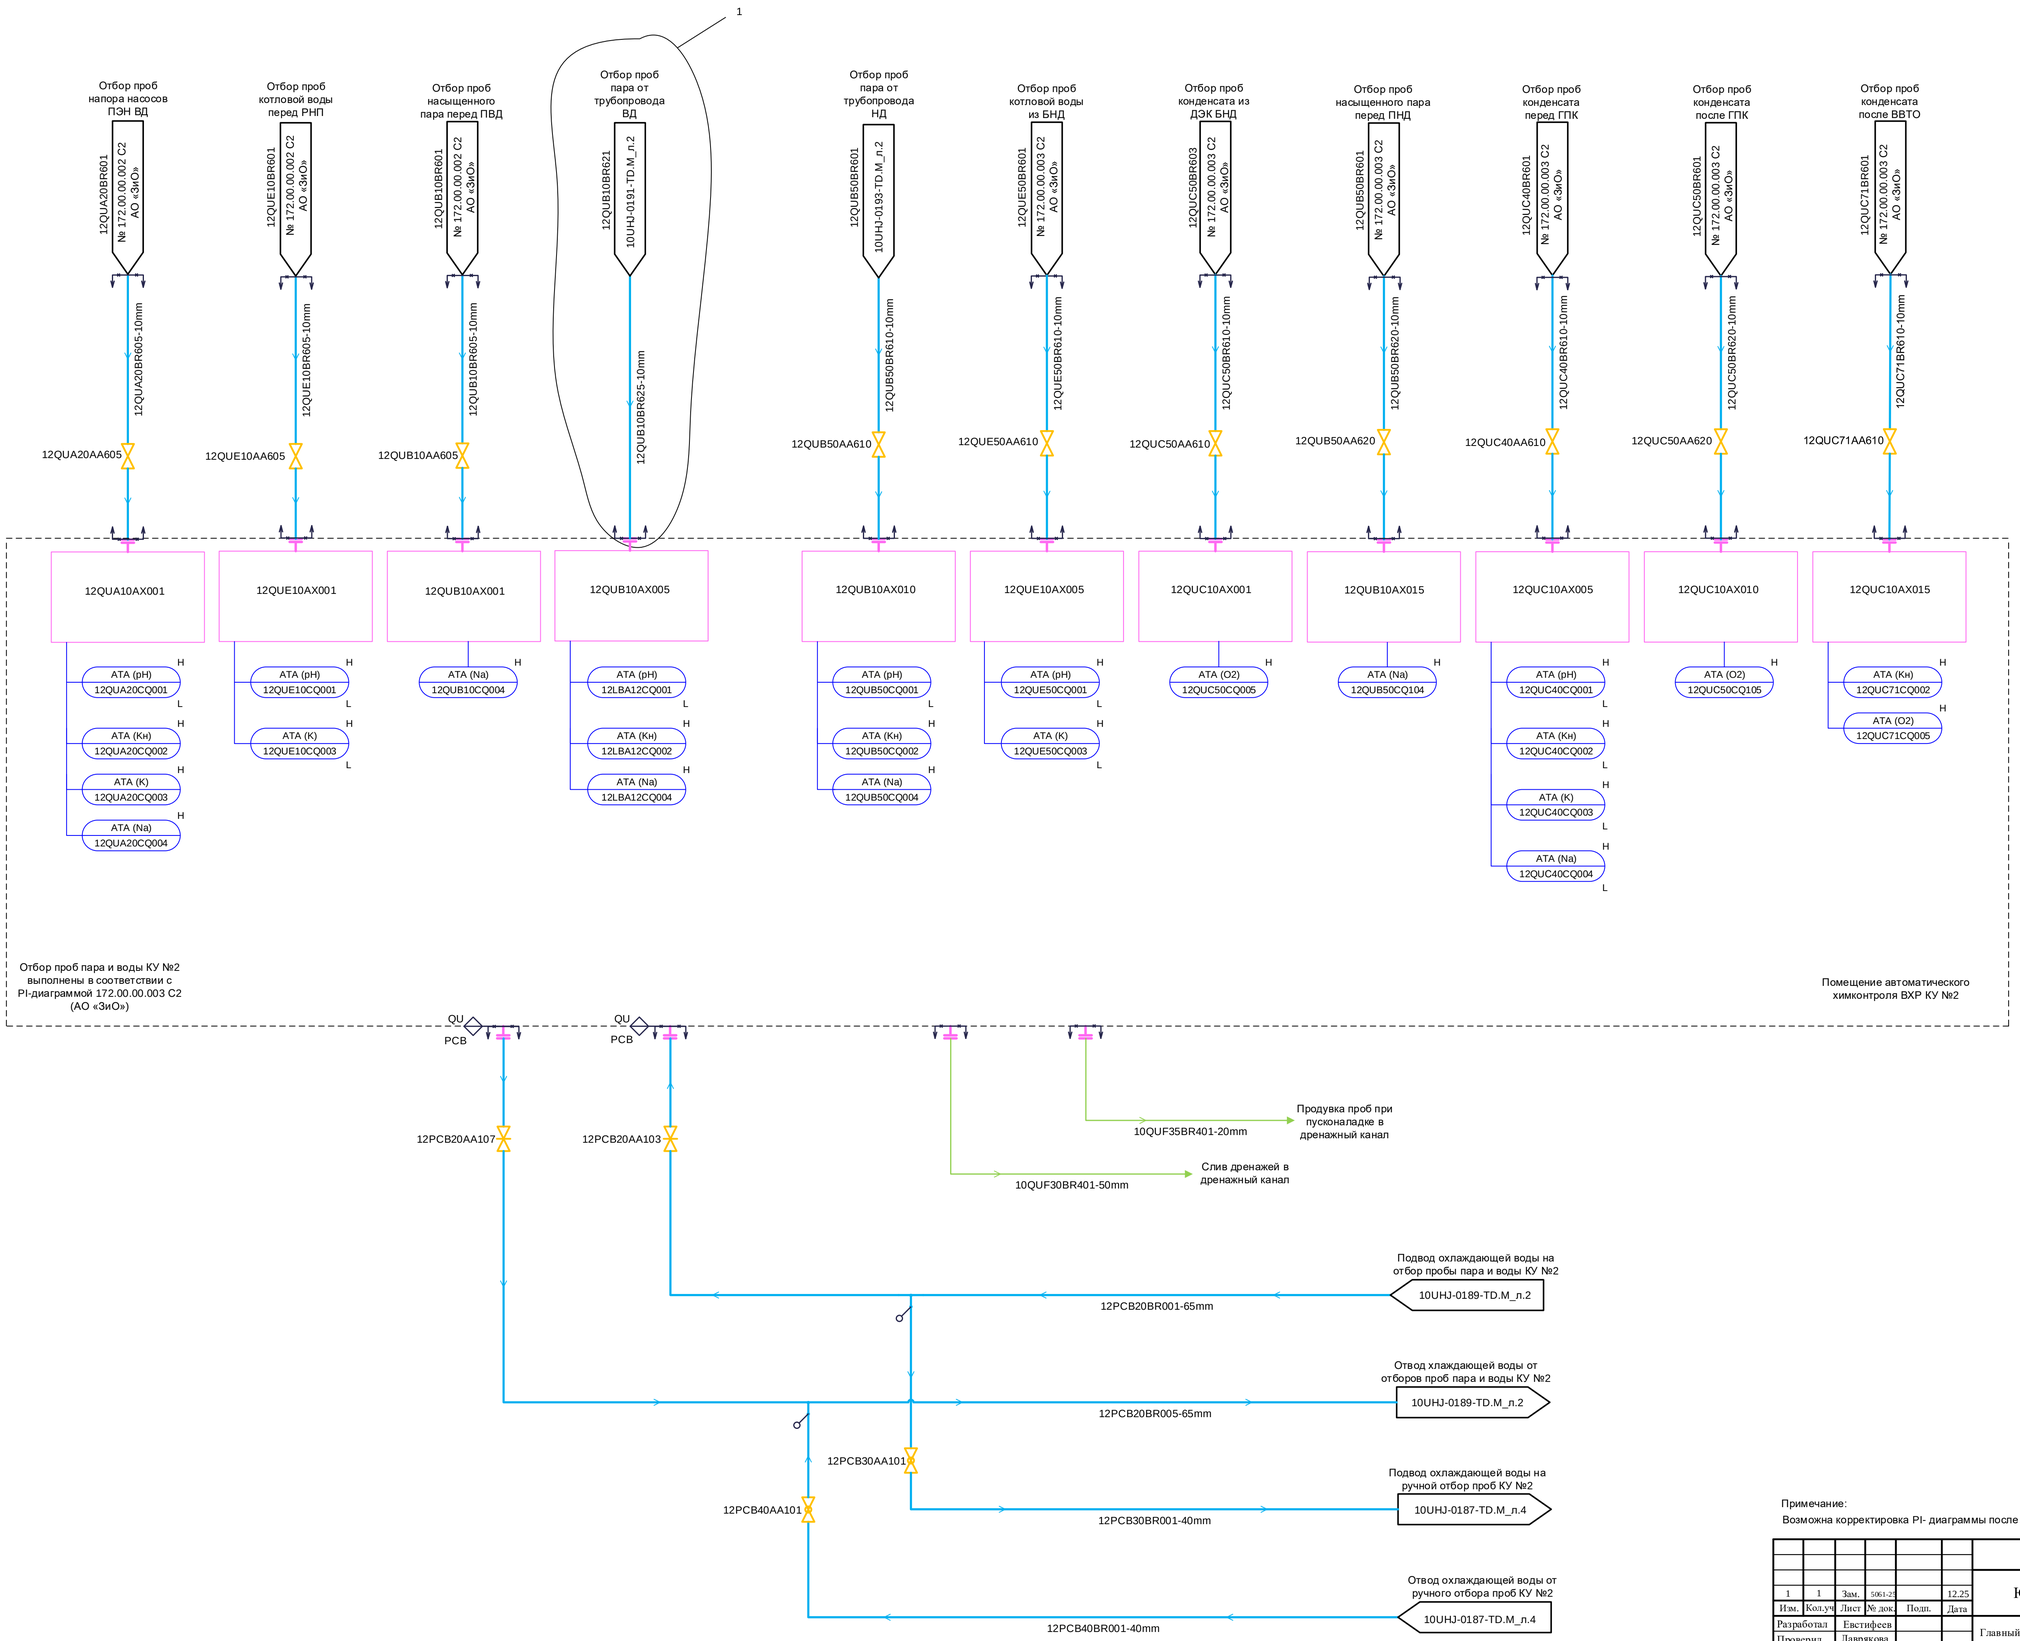

Примечание:

Возможна корректировка PI- диаграммы после получения ИД от поставщика оборудования

1	1	Зам.	5061-23		12.25	261N1 – 10UHJ – 0187 – TD.M
Изм.	Кол.уч	Лист	№ док.	Подп.	Дата	Южно-Якутская ТЭС. Рабочая документация
Разработал		Евстифеев				Главный корпус. PI-диаграмма трубопроводов отбора проб пара и воды.
Проверил		Лаврякова				Стадия: Р; Лист: 3; Листов:
Гл. спец.		Сергеева				
Н. контр.		Черемушкина				PI-диаграмма трубопроводов отбора проб пара и воды КУ №2. Система PCB, QUB, QUC, QUE, QUA, LBA.

АКЦИОНЕРНОЕ ОБЩЕСТВО ИНСТИТУТ ТЕПЛОЭЛЕКТРОПРОЕКТ г. МОСКВА

Согласовано

ОАСУ

Взам. инв. №

Подпись и дата

Инв. № подл.

Формат А1