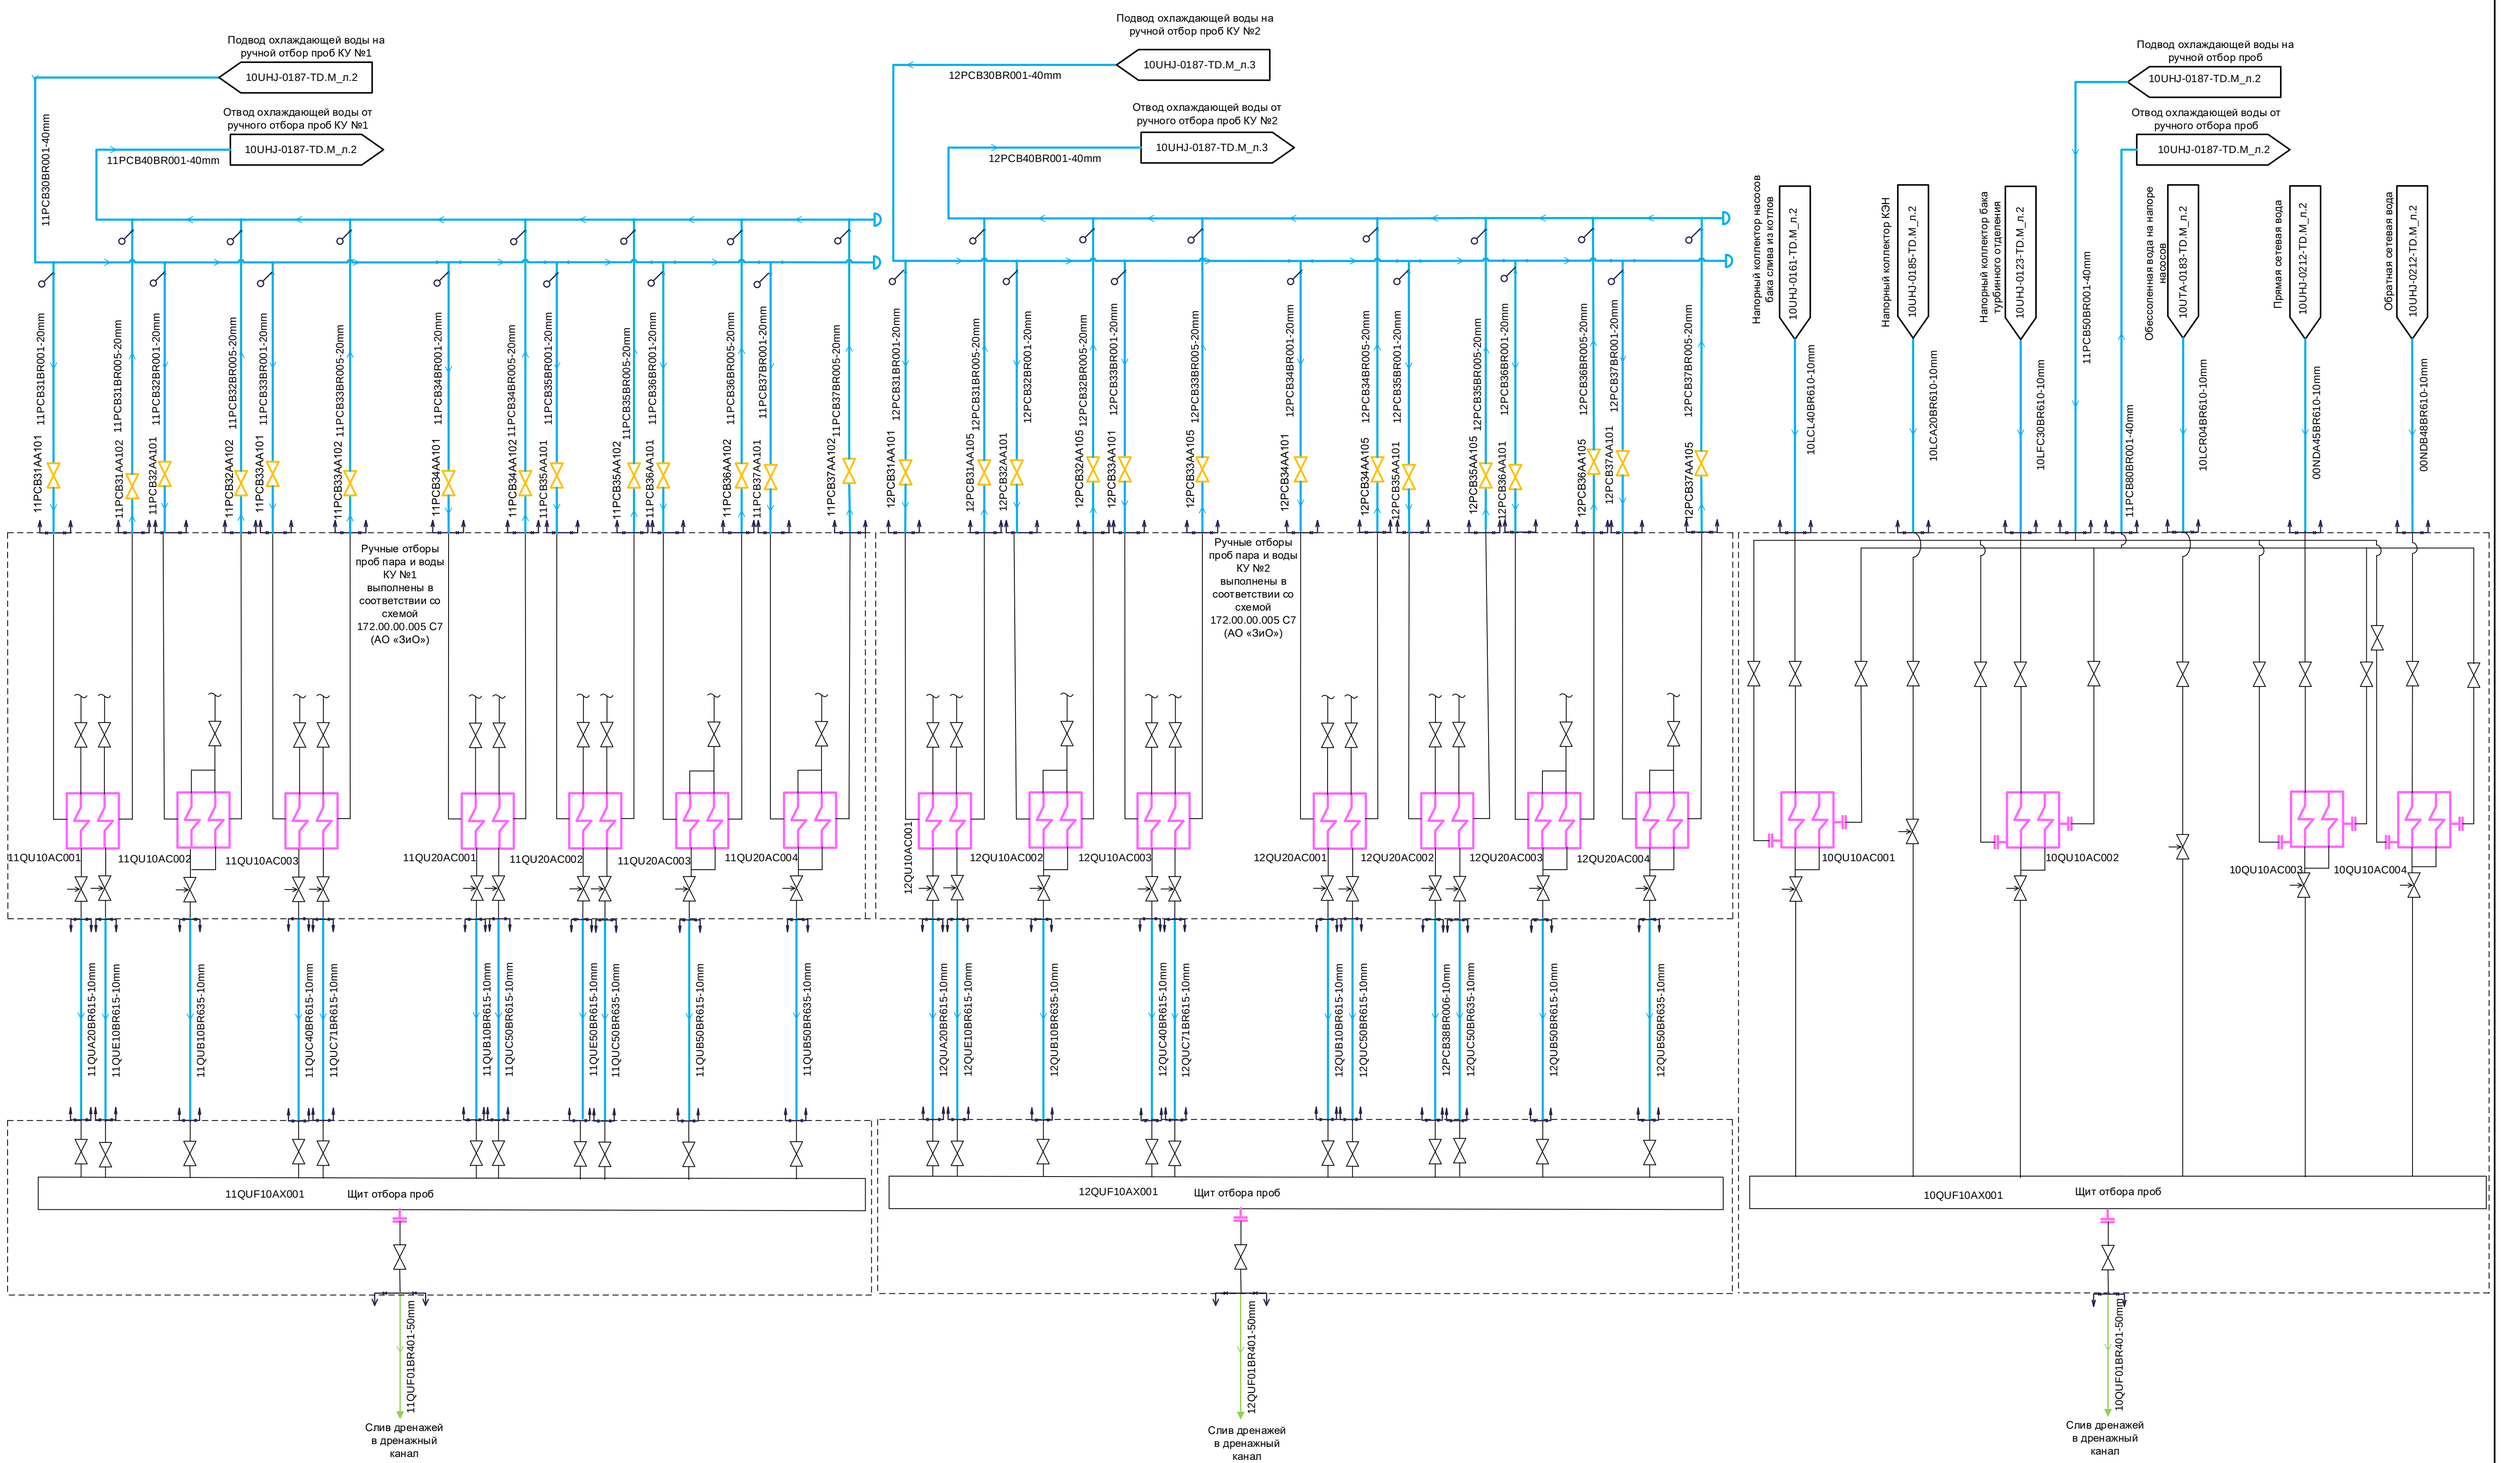

Примечание:

Возможна корректировка PI- диаграммы после получения ИД от поставщика оборудования

						261N1 – 10UHJ – 0187 – TD.M		
1	-	Зам.	5061-25		12.25	Южно-Якутская ТЭС. Рабочая документация		
Изм.	Кол.уч	Лист	№ док.	Подп.	Дата			
Разработал		Евстифеев				Главный корпус. PI-диаграмма трубопроводов отбора проб пара и воды.	Стадия	Лист	Листов
Проверил		Лаврякова					Р	4	
Гл. спец.		Сергеева							
Н. контр.		Черемушкина				PI-диаграмма трубопроводов ручных отборов проб пара и воды КУ №1, КУ №2 и общестанционной части. Система PCB, QUB, QUC, QUE, QUA.	АКЦИОНЕРНОЕ ОБЩЕСТВО «ВНИИПИ Теплоэлектропроект» г. Москва	

Согласовано

ОАСУ

Взам. инв. №

Подпись и дата

Инв. № подл.

Формат А1