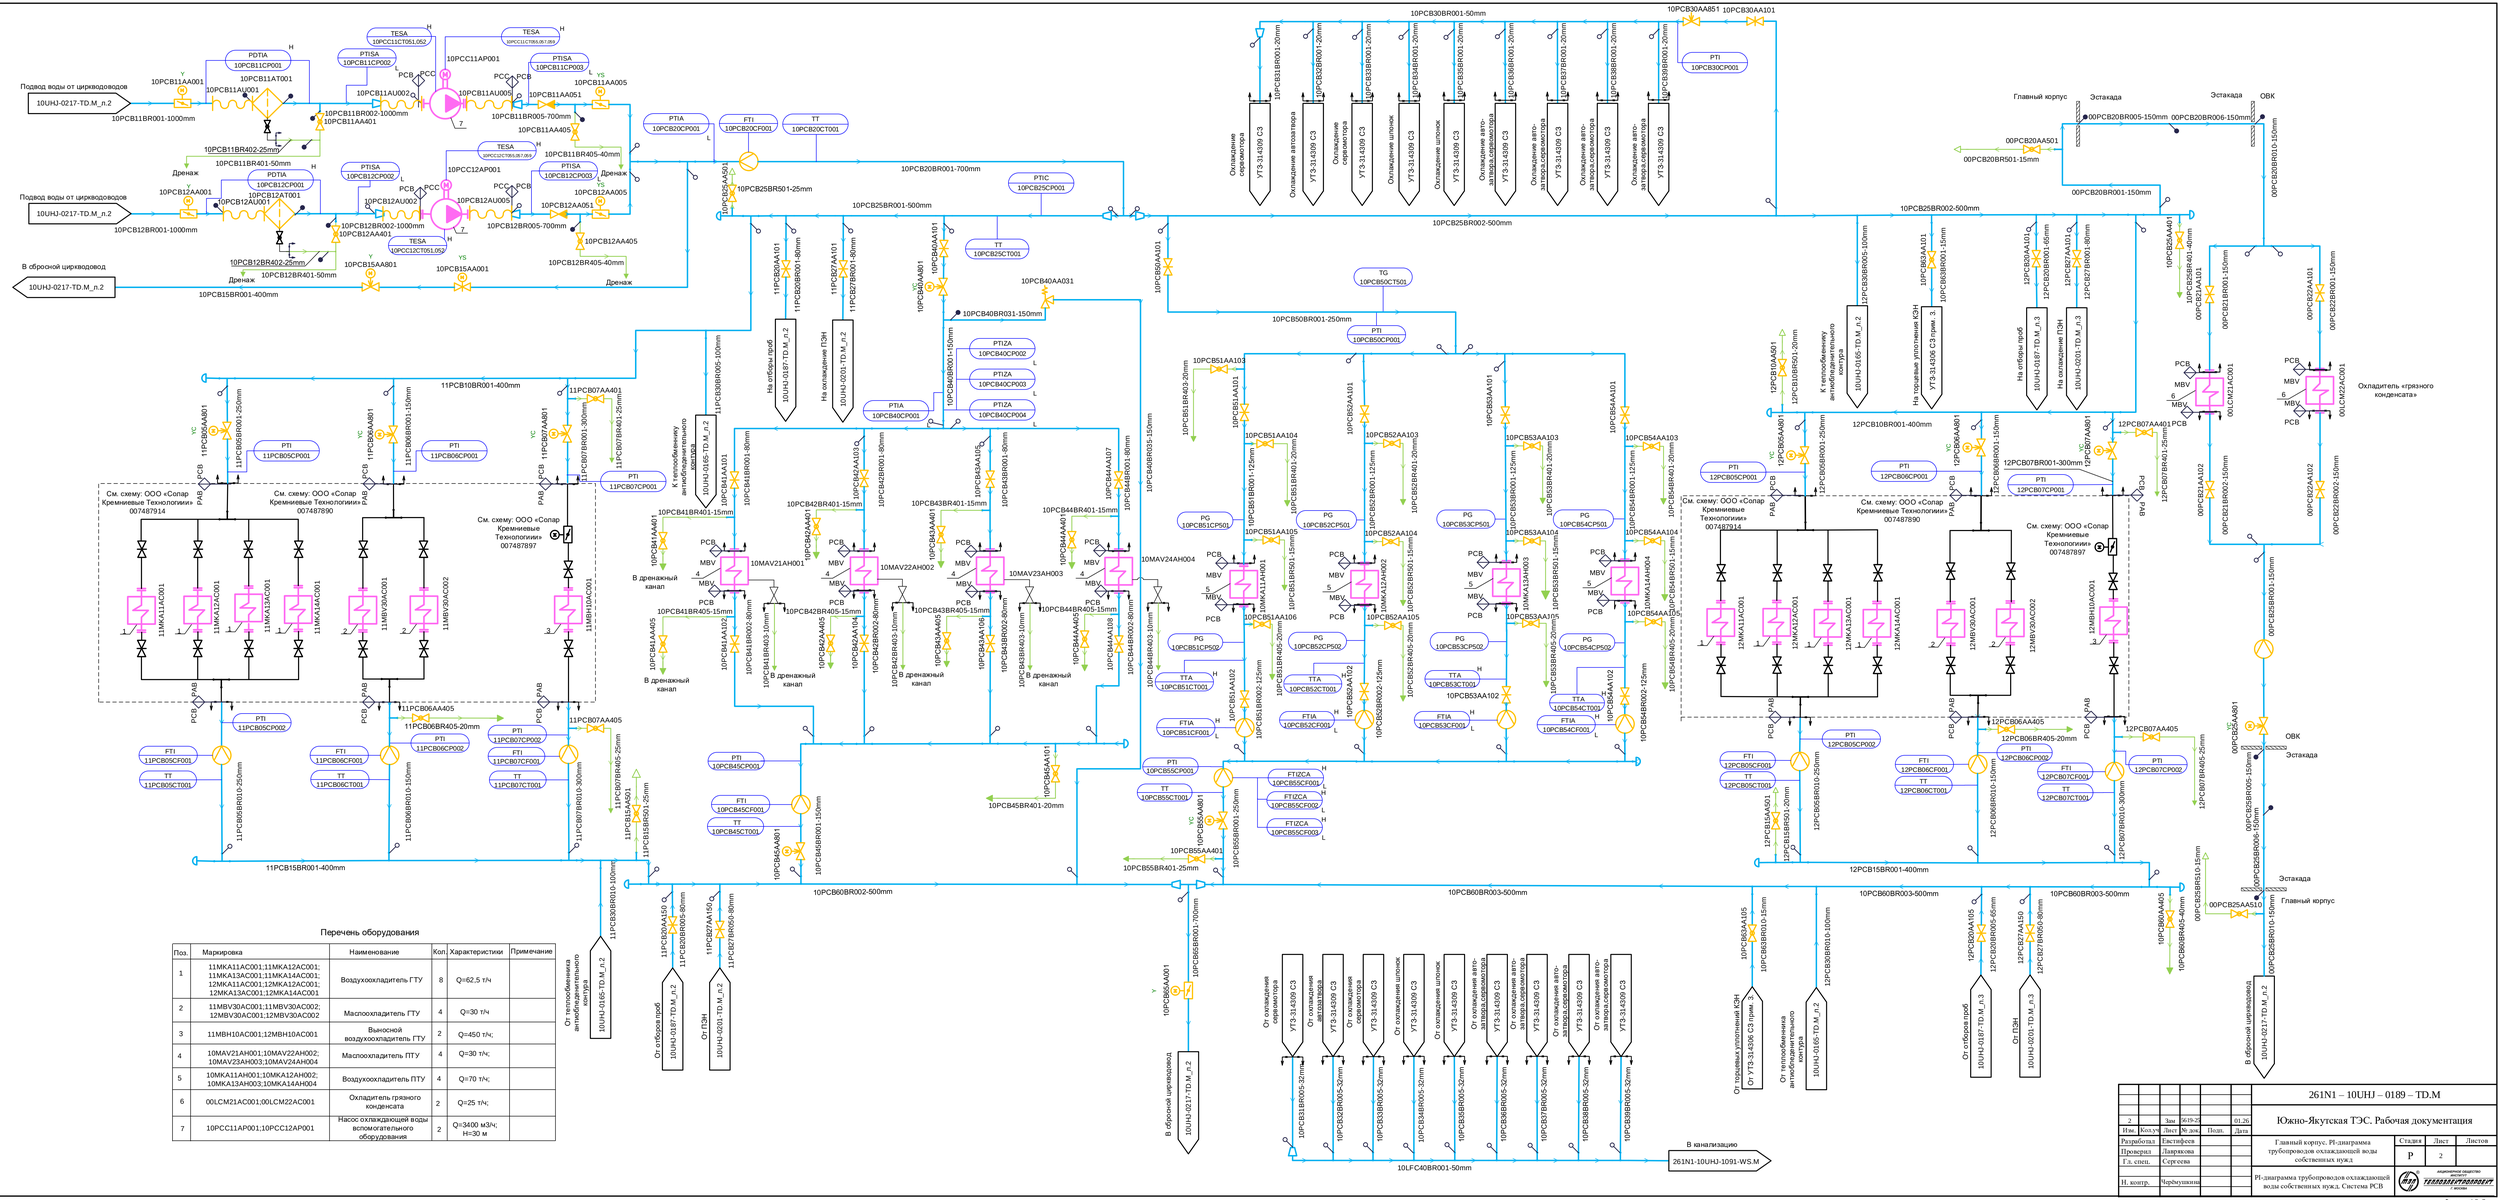


## Перечень оборудования

| Поз. | Маркировка | Наименование | Кол. | Характеристики | Примечание |
|---|---|---|---|---|---|
| 1 | 11MKA11AC001;11MKA12AC001;<br>11MKA13AC001;11MKA14AC001;<br>12MKA11AC001;12MKA12AC001;<br>12MKA13AC001;12MKA14AC001 | Воздухоохладитель ГТУ | 8 | Q=62,5 т/ч | |
| 2 | 11MBV30AC001;11MBV30AC002;<br>12MBV30AC001;12MBV30AC002 | Маслоохладитель ГТУ | 4 | Q=30 т/ч | |
| 3 | 11MBH10AC001;12MBH10AC001 | Выносной воздухоохладитель ГТУ | 2 | Q=450 т/ч; | |
| 4 | 10MAV21AH001;10MAV22AH002;<br>10MAV23AH003;10MAV24AH004 | Маслоохладитель ПТУ | 4 | Q=30 т/ч; | |
| 5 | 10MKA11AH001;10MKA12AH002;<br>10MKA13AH003;10MKA14AH004 | Воздухоохладитель ПТУ | 4 | Q=70 т/ч; | |
| 6 | 00LCM21AC001;00LCM22AC001 | Охладитель грязного конденсата | 2 | Q=25 т/ч; | |
| 7 | 10PCC11AP001;10PCC12AP001 | Насос охлаждающей воды вспомогательного оборудования | 2 | Q=3400 м3/ч;<br>H=30 м | |

| | | | | | | | |
|---|---|---|---|---|---|---|---|
| 2 | | Зам | 5619-23 | | 01.26 | 261N1 – 10UHJ – 0189 – TD.M | |
| Изм. | Кол.уч | Лист | № док. | Подп. | Дата | Южно-Якутская ТЭС. Рабочая документация | |
| Разработал | | Евстифеев | | | | Главный корпус. PI-диаграмма трубопроводов охлаждающей воды собственных нужд | Стадия: Р; Лист: 2; Листов: |
| Проверил | | Ларионов | | | | | |
| Гл. спец. | | Сергеева | | | | | |
| Н. контр. | | Черемушкина | | | | PI-диаграмма трубопроводов охлаждающей воды собственных нужд. Система PCB | АКЦИОНЕРНОЕ ОБЩЕСТВО «ТЕХНОПРОМЭКСПОРТ» |

Согласовано

ОАСУ

Взам. инв. №

Подпись и дата

Инв. № подл.

Формат А2х3