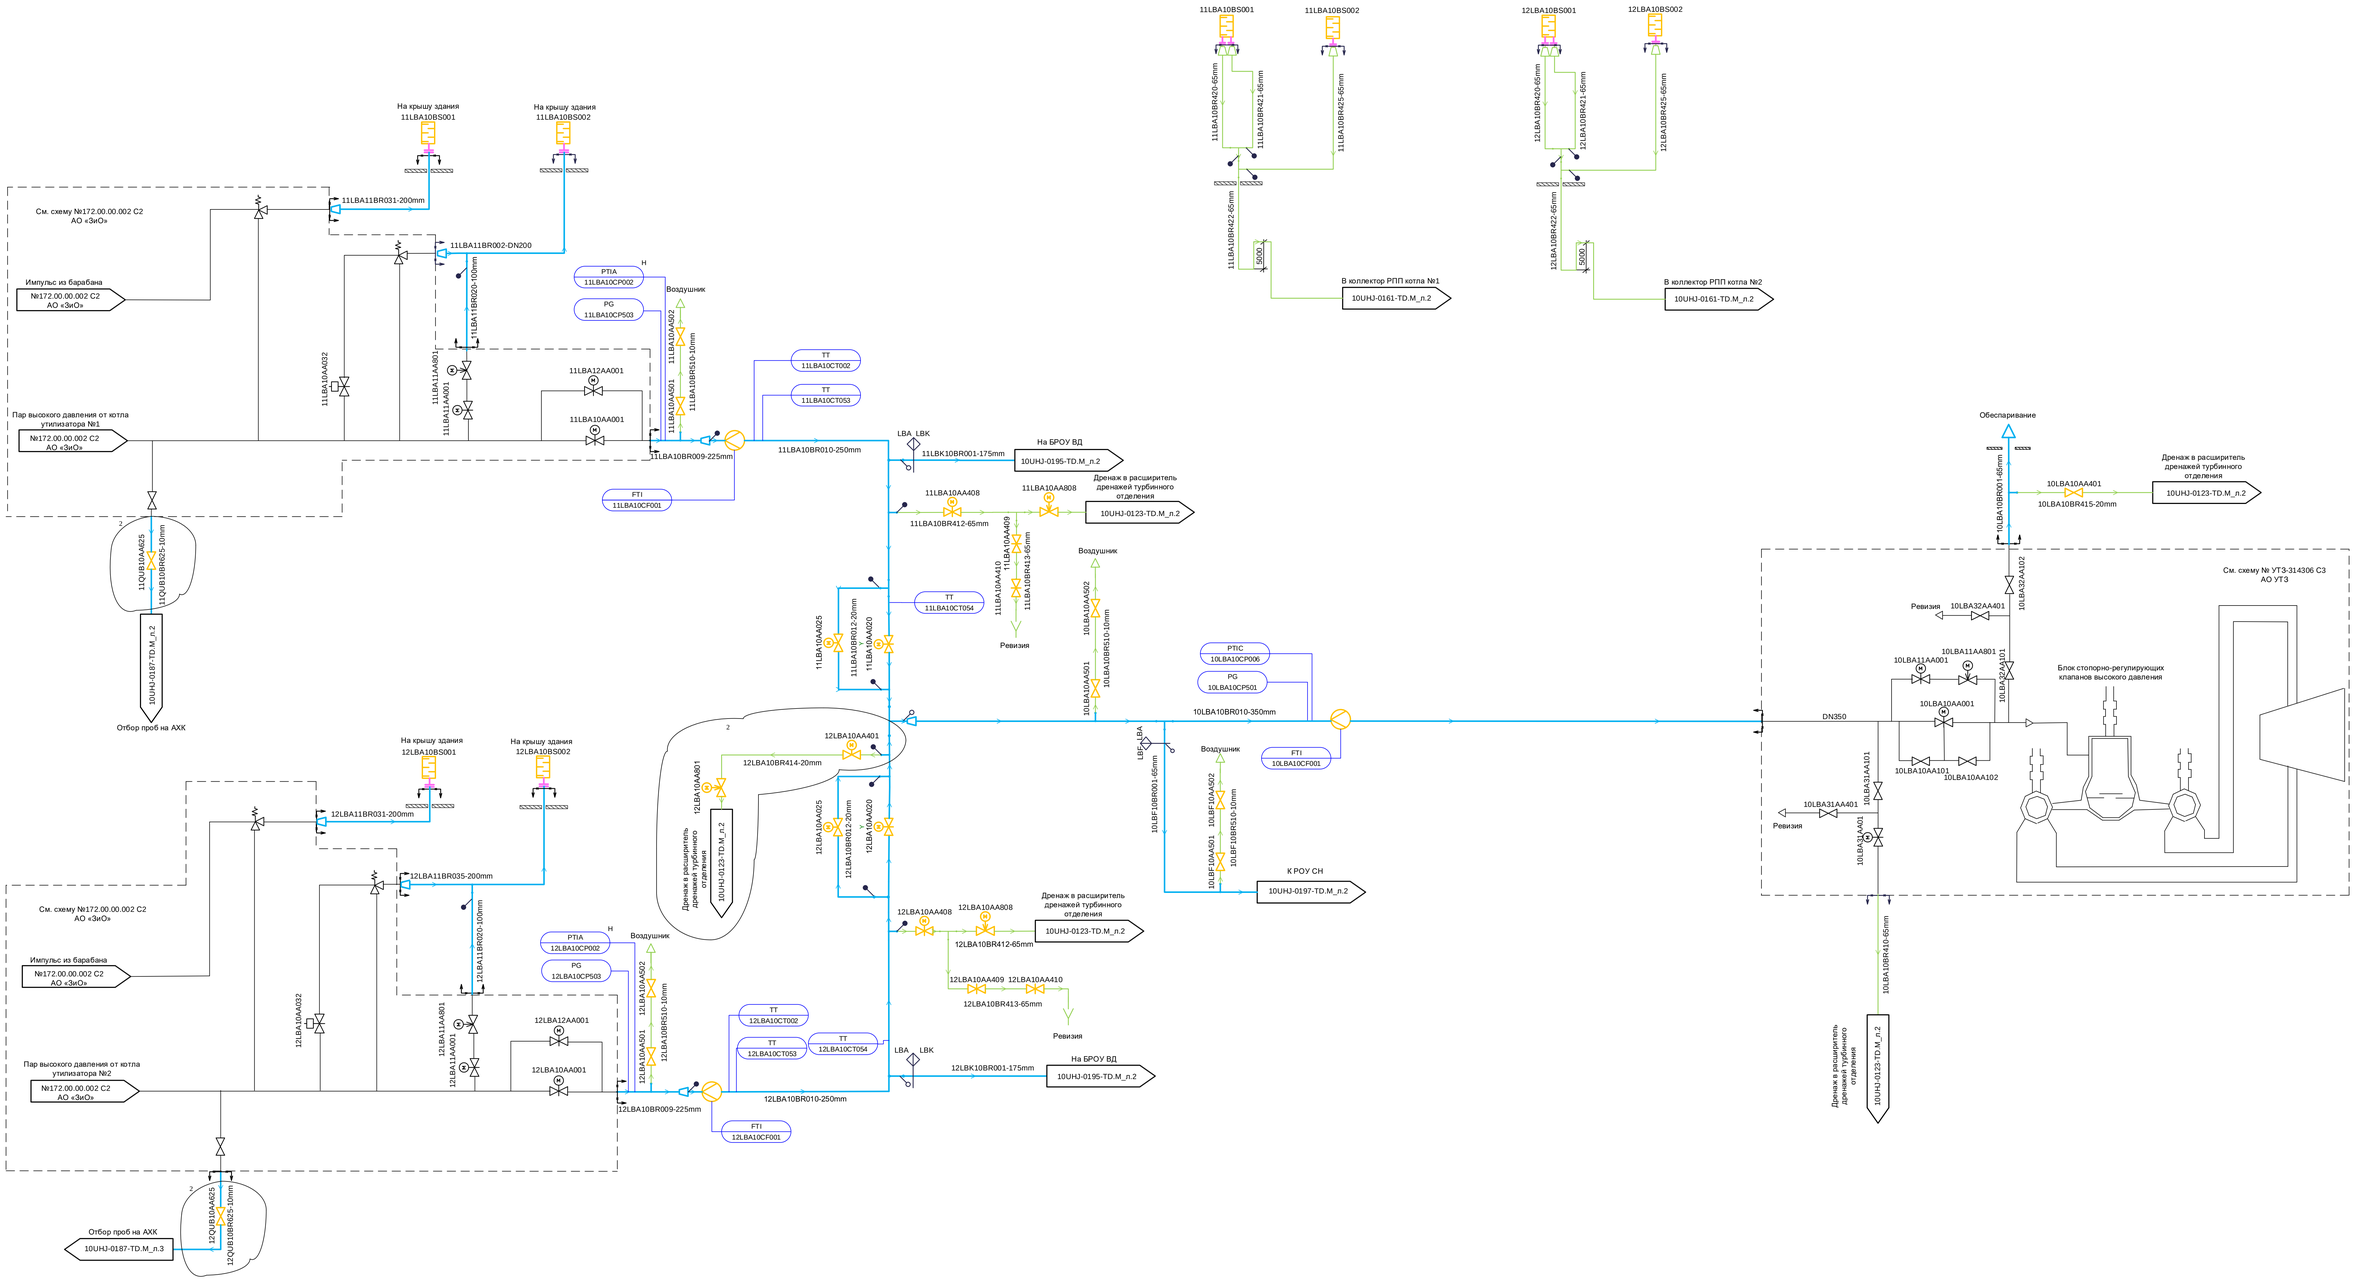

						261N1-10UHJ-0191-TD.M
1		Зам.	3018-25		10.25	Южно-Якутская ТЭС. Рабочая документация
Изм.	Кол.уч.	Лист	№ док.	Подп.	Дата	
Разработал		Евстифеев				Главный корпус. PI-диаграмма трубопроводов пара высокого давления.
Проверил		Лаврикова				
Гл. спец.		Сергеева				
Н. контр.		Черемушкина				PI-диаграмма трубопроводов пара высокого давления. Система LBA

Стадия	Лист	Листов
Р	2	

АКЦИОНЕРНОЕ ОБЩЕСТВО ИНСТИТУТ ТЕПЛОЭЛЕКТРОПРОЕКТ

Согласовано

ОЛКУ

Взам. инв. №

Подпись и дата

Инв. № подл.

Формат А1х2