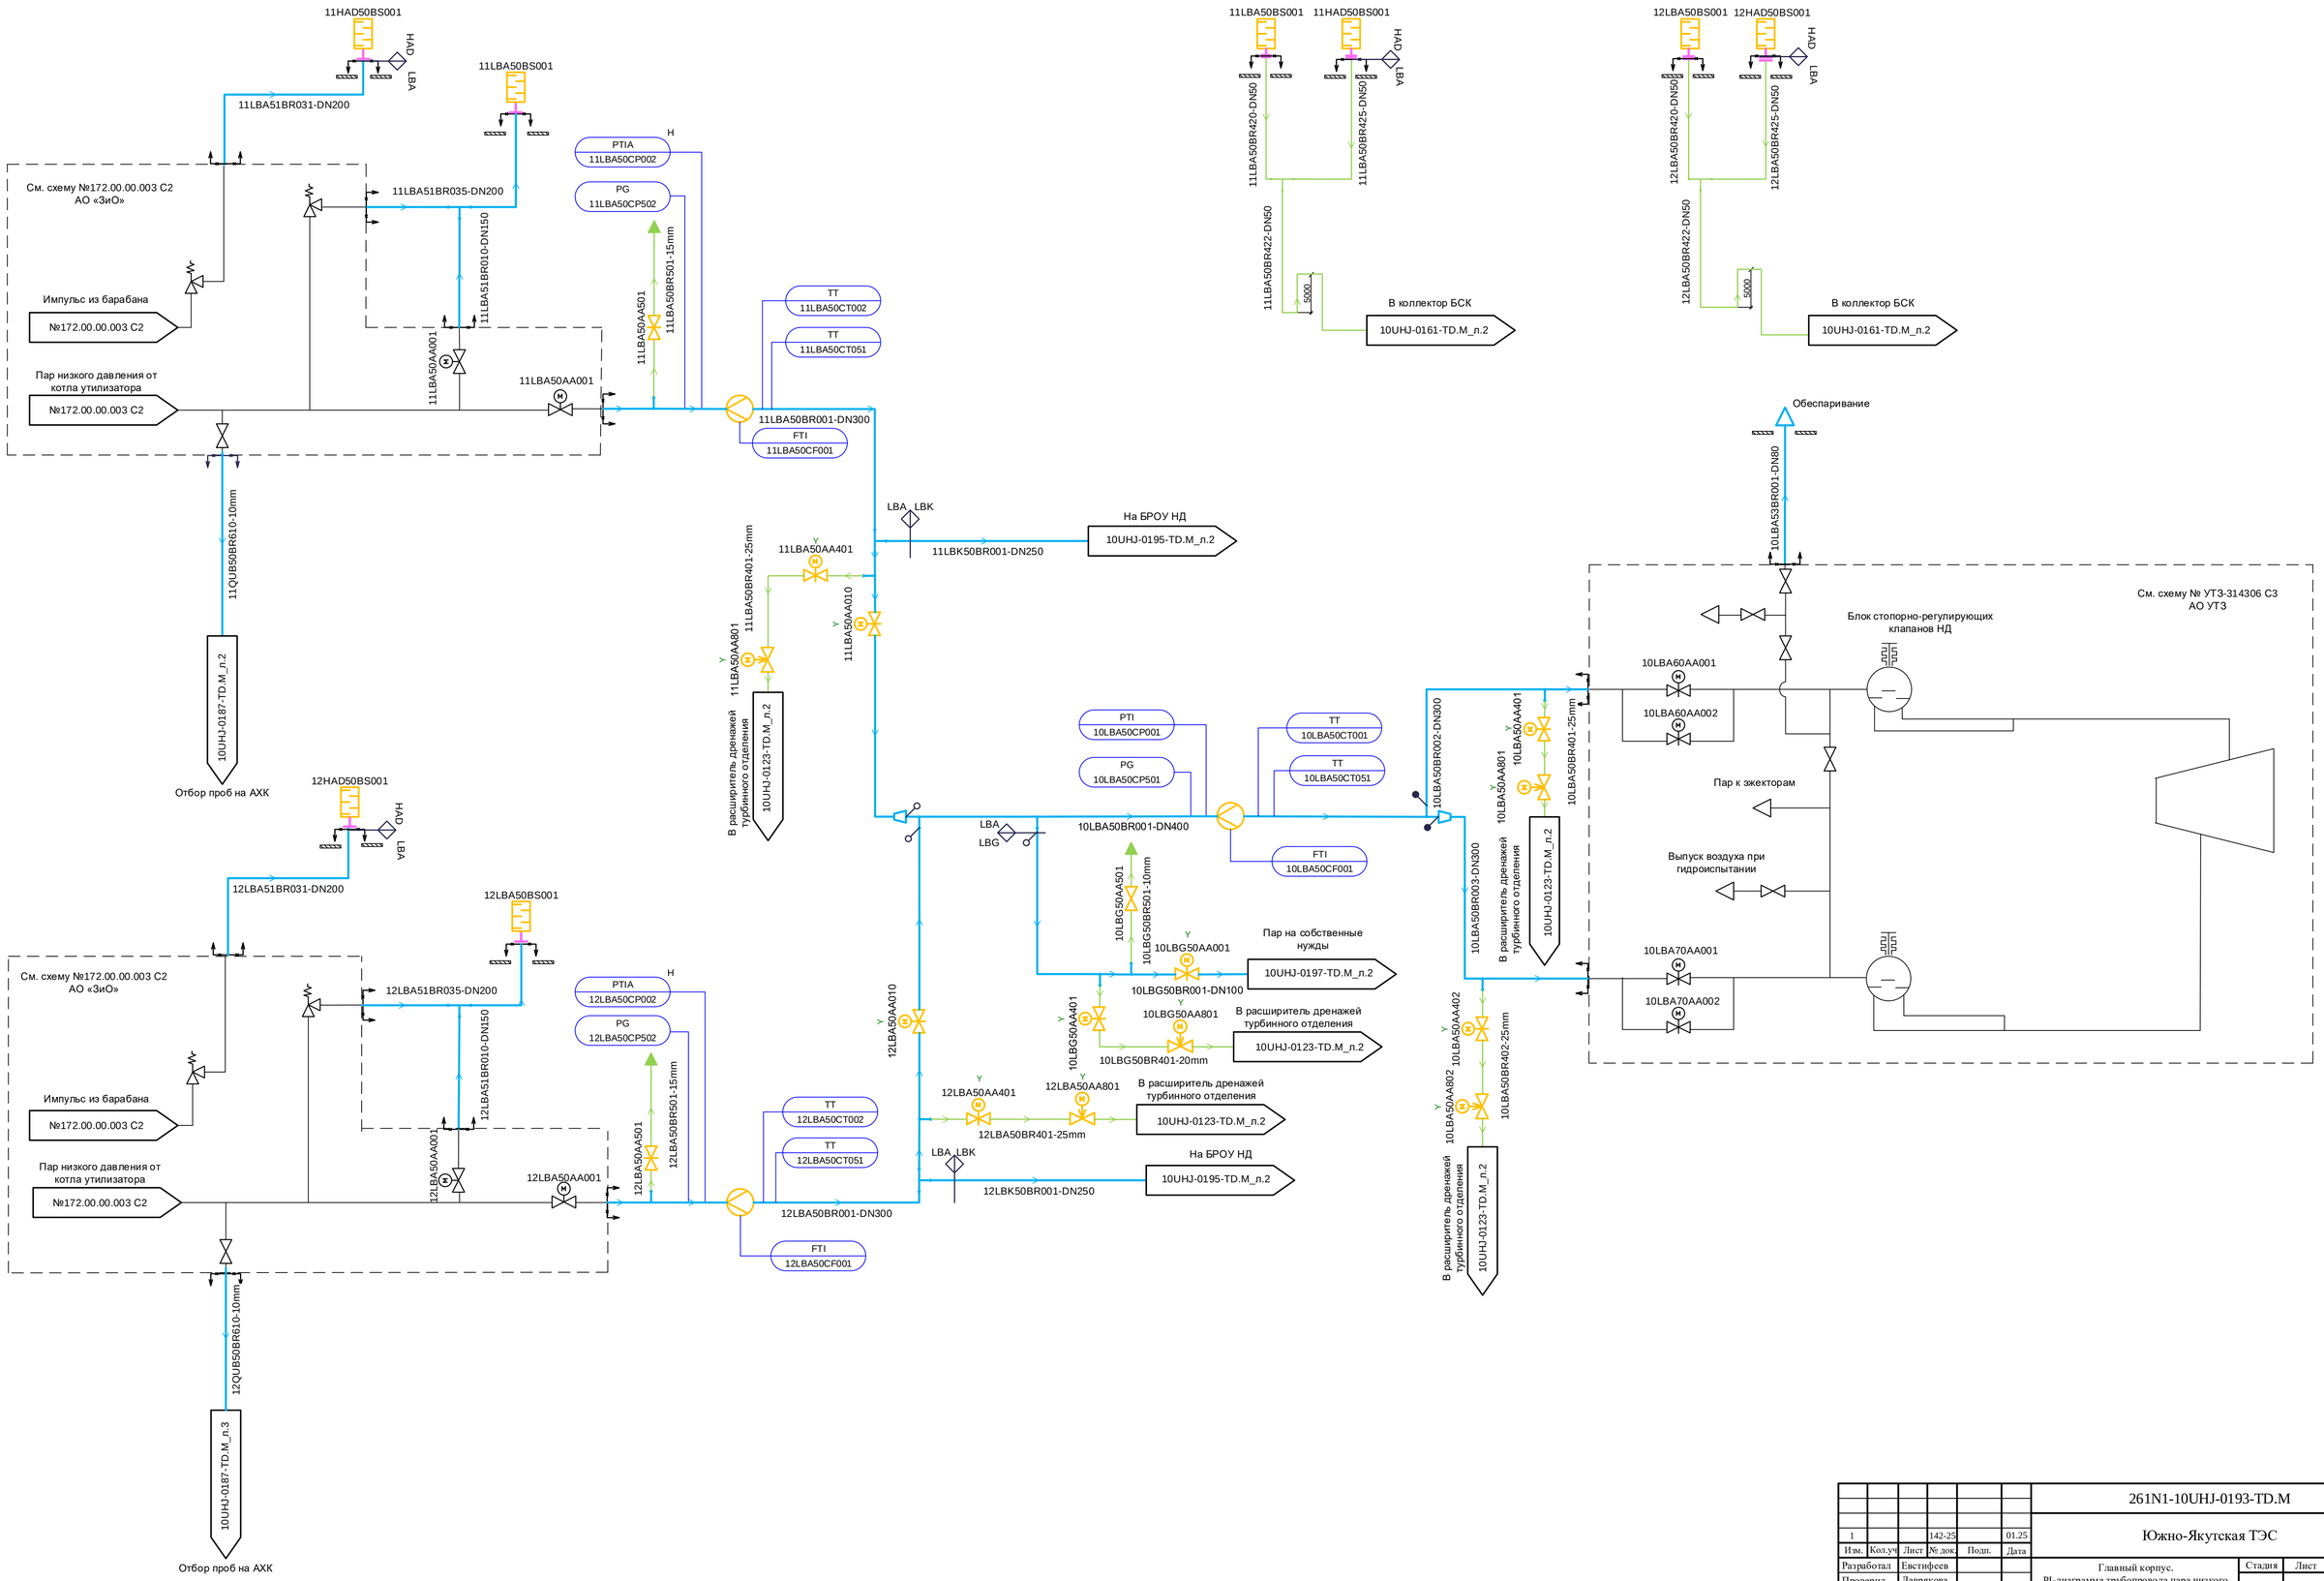

						261N1-10UHJ-0193-TD.M		
1			142-25		01.25	Южно-Якутская ТЭС		
Изм.	Кол.уч	Лист	№ док.	Подп.	Дата			
Разработал	Евстифеев					Главный корпус. PI-диаграмма трубопровода пара низкого давления	Стадия	Лист	Листов
Проверил	Лаврякова						Р	2	
Гл. спец.	Супонина								
Н. контр.	Черемушкина					PI-диаграмма трубопровода пара низкого давления. Система LBA	АКЦИОНЕРНОЕ ОБЩЕСТВО ИНСТИТУТ ТЕПЛОЭЛЕКТРОПРОЕКТ г. МОСКВА		

Согласовано

ОАСУ

Взам. инв. №

Подпись и дата

Инв. № подл.

Формат А1