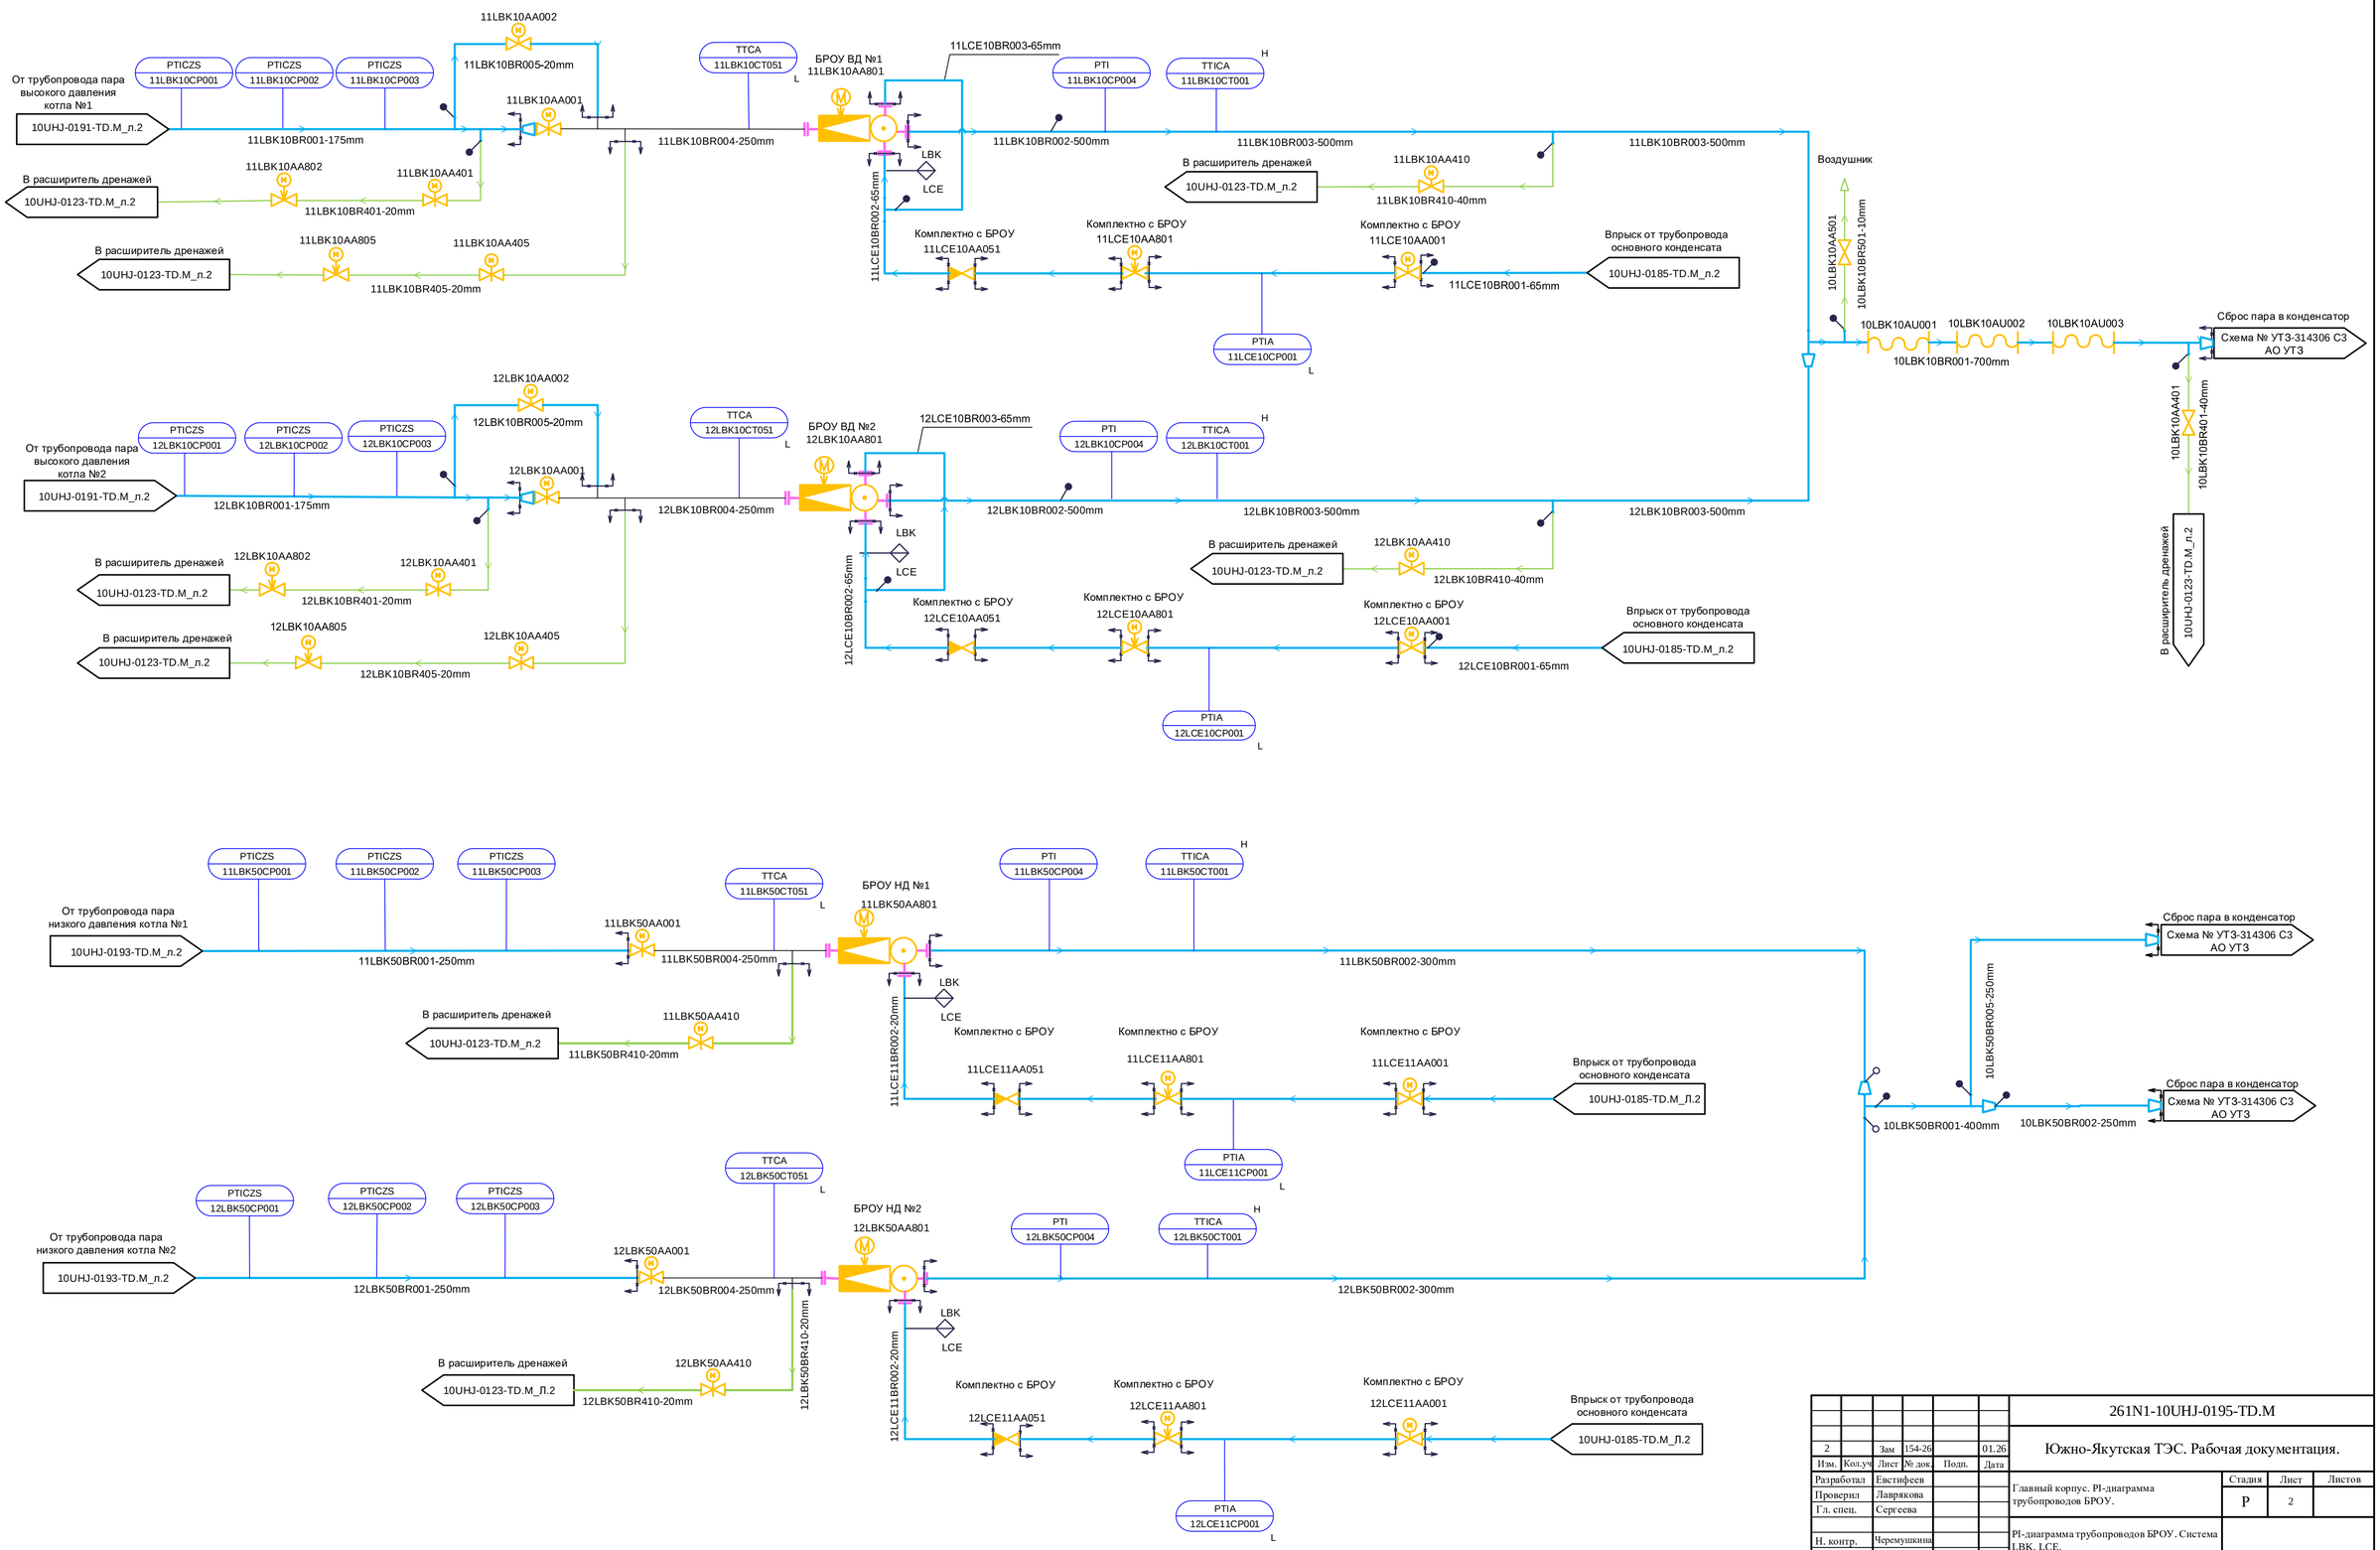

2		Зам	154-26		01.26	261N1-10UHJ-0195-TD.M
Изм.	Кол.уч	Лист	№ док.	Подп.	Дата	Южно-Якутская ТЭС. Рабочая документация.
Разработал		Евстифеев				Главный корпус. PI-диаграмма трубопроводов БРОУ.
Проверил		Лаврякова				Стадия: Р; Лист: 2; Листов:
Гл. спец.		Сергеева				
Н. контр.		Черемушкина				PI-диаграмма трубопроводов БРОУ. Система LBK, LCE.

Согласовано

ОАСУ

Взам. инв. №

Подпись и дата

Инв. № подл.

Формат А1