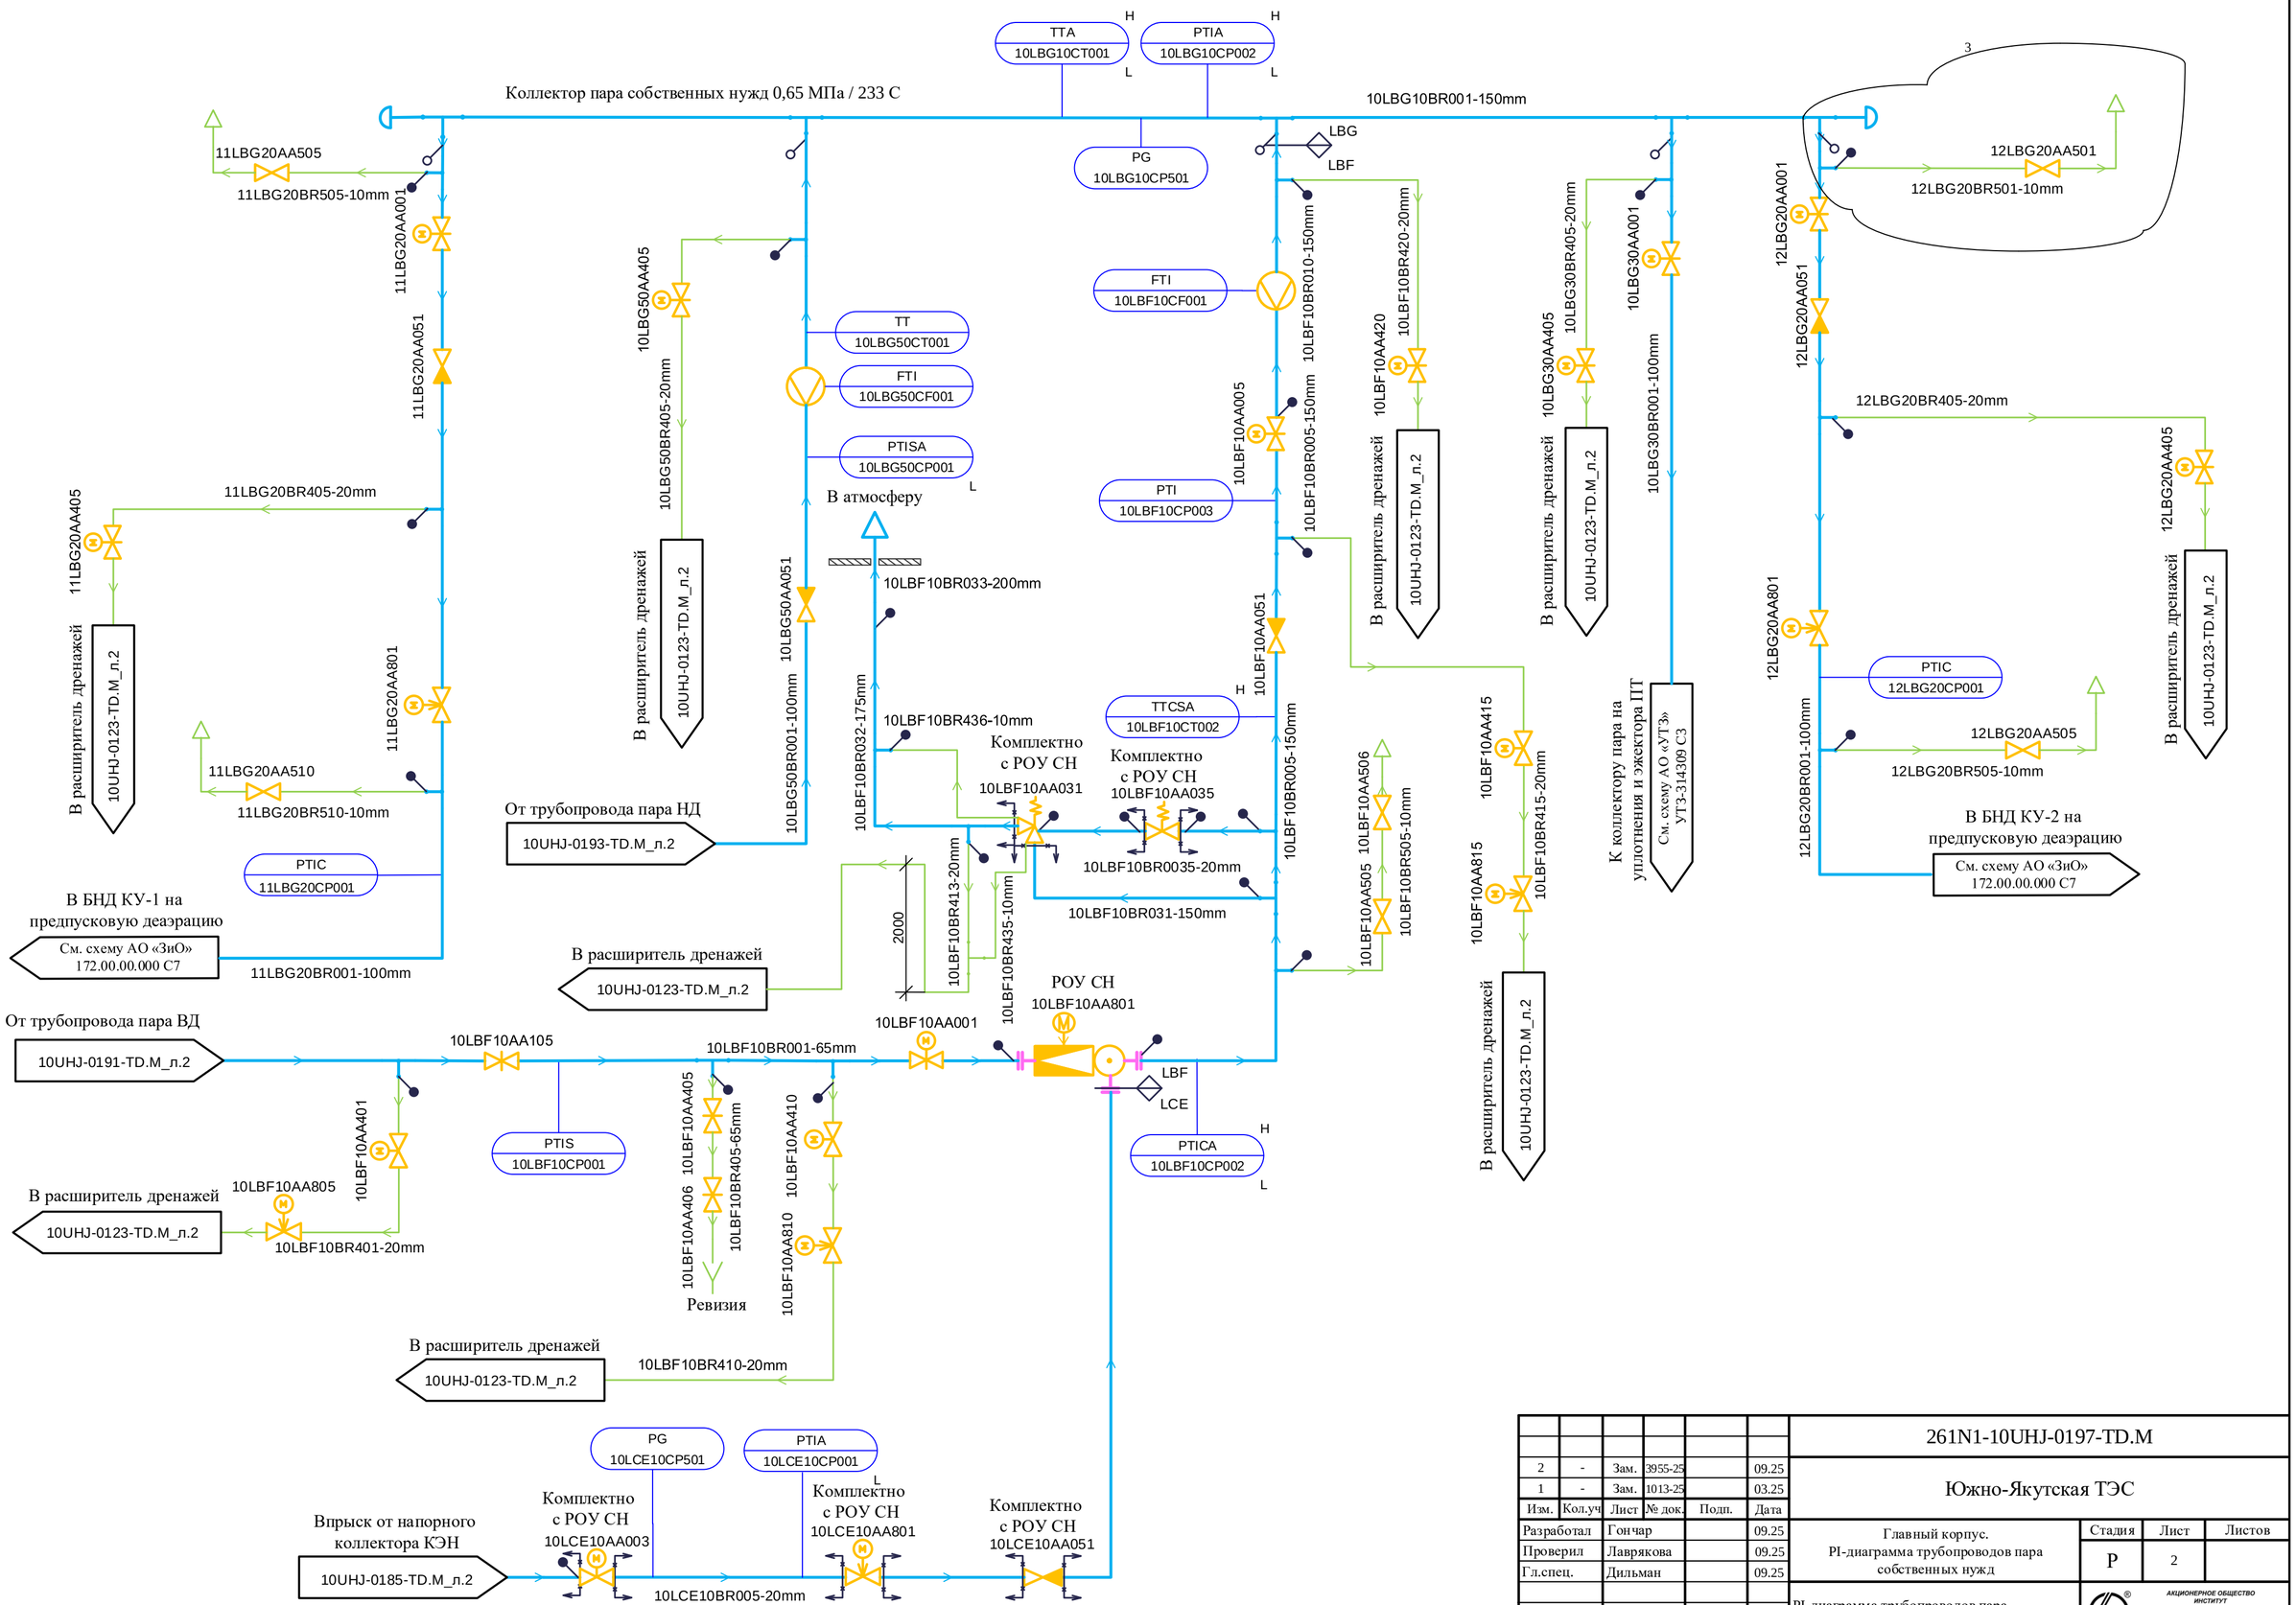

2	-	Зам.	3955-25		09.25	261N1-10UHJ-0197-TD.M
1	-	Зам.	1013-25		03.25	Южно-Якутская ТЭС
Изм.	Кол.уч	Лист	№ док.	Подп.	Дата	
Разработал		Гончар			09.25	Главный корпус. PI-диаграмма трубопроводов пара собственных нужд
Проверил		Лаврякова			09.25	
Гл.спец.		Дильман			09.25	
Н. контр.		Черемушкина			09.25	PI-диаграмма трубопроводов пара собственных нужд. Система LBG

Стадия	Лист	Листов
Р	2	

АКЦИОНЕРНОЕ ОБЩЕСТВО ИНСТИТУТ ТЕПЛОЭЛЕКТРОПРОЕКТ г. МОСКВА

Согласовано

ОАСУ

Взам. инв. №

Подпись и дата

Инв. № подл.

Формат А2