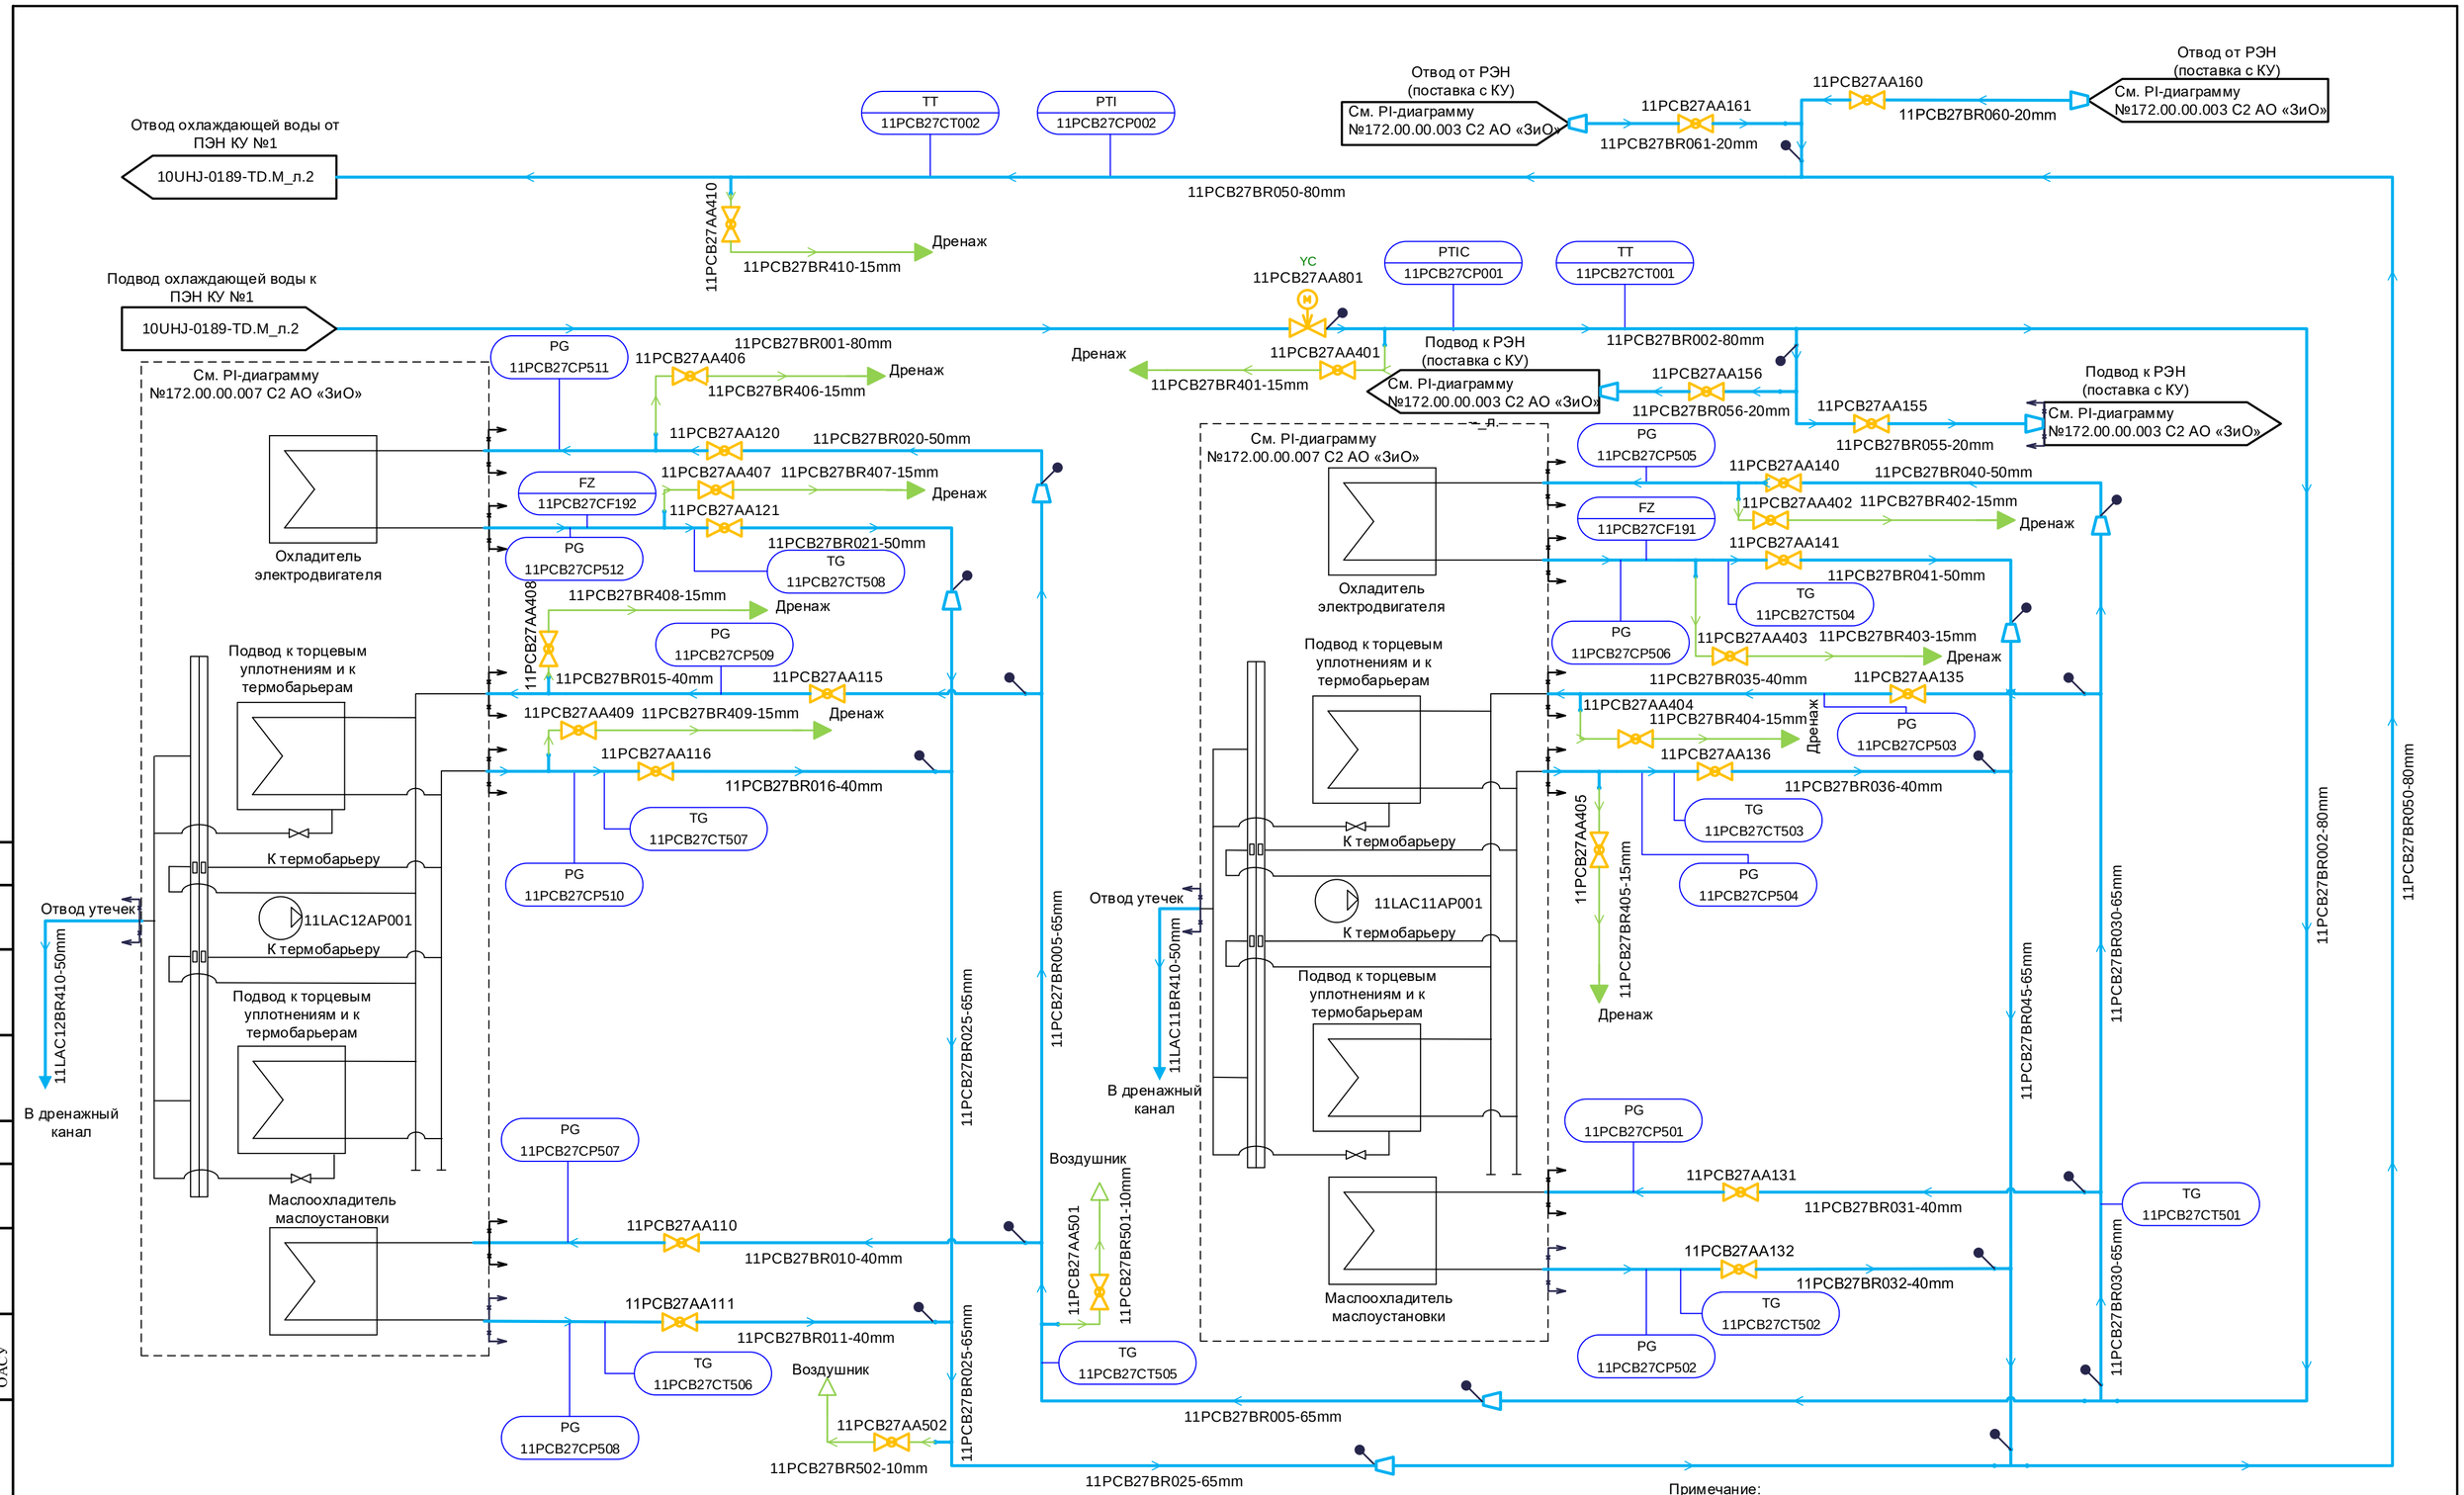

Примечание:
Возможна корректировка PI- диаграммы после получения ИД от поставщика оборудования

1	-	Зам.	5061-25		12.25	
Изм.	Кол.уч	Лист	№ док.	Подп.	Дата	

261N1 – 10UHJ – 0201 – TD.M

Южно-Якутская ТЭС. Рабочая документация

Разработал	Евстифеев	
Проверил	Лаврякова	
Гл. спец.	Сергеева	
Н. контр.	Черемушкина	

Главный корпус. PI-диаграмма вспомогательных трубопроводов охлаждения ПЭН.

Стадия	Лист	Листов
Р	2	

PI-диаграмма вспомогательных трубопроводов охлаждения ПЭН КУ №1. Система РСВ.

АКЦИОНЕРНОЕ ОБЩЕСТВО ИНСТИТУТ ТЕПЛОЭЛЕКТРОПРОЕКТ Г. МОСКВА

Согласовано

ОАСУ

Взам. инв. №

Подпись и дата

Инв. № подл.

Формат А2