Перечень оборудования

Поз.	KKS	Наименование	Кол.	Хар-ки	Примечание
1	10NDE10BB001	Дренажный бак сетевой воды	1	V=35 м3	-
2	10NDE10AP001	Полупогружной насос бака сбора дренажей сетевой воды	1	Q=50 м3/ч; H=0,75 МПа	

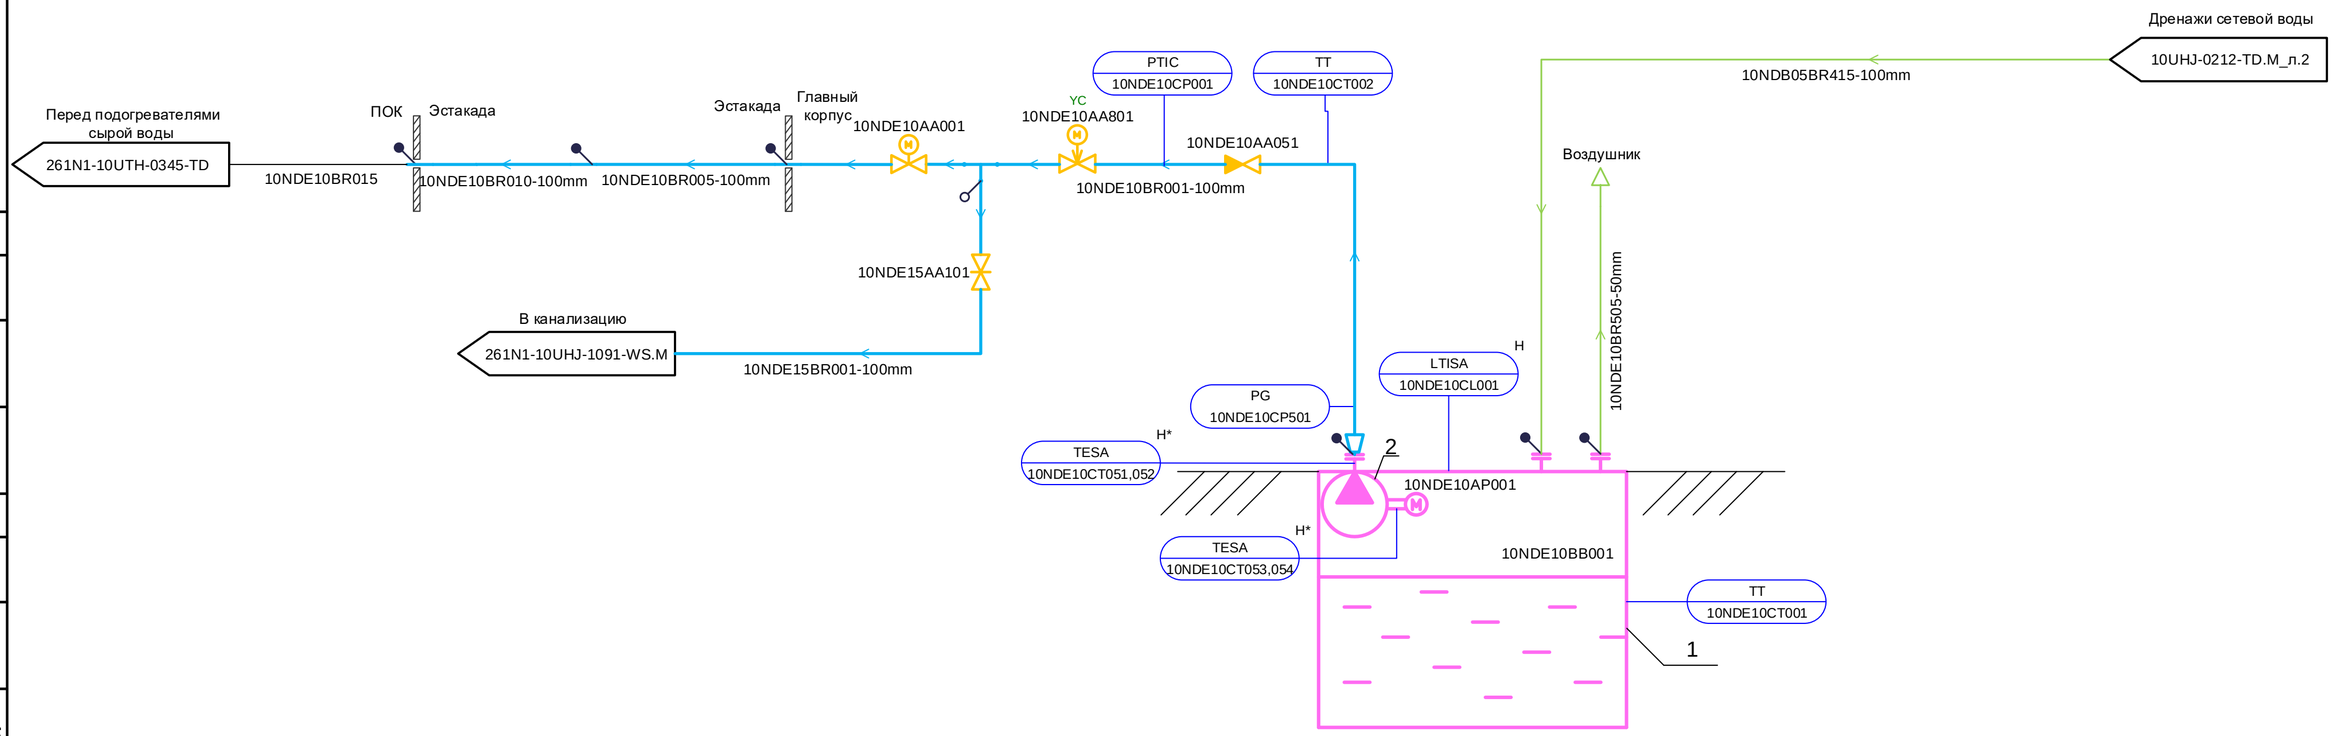

Примечание:

1. * - Датчики поставляются комплектно с насосом.

1	-	Зам.	6302-25		12.25	
Изм.	Кол.уч	Лист	№ док.	Подп.	Дата	

261N1 – 10UHJ – 0207 – TD.M

Южно-Якутская ТЭС. Рабочая документация

Разработал	Лаврякова	
Проверил	Сергеева	
Н. контр.	Черемушкина	

Главный корпус. PI-диаграмма трубопроводов сбора дренажей сетевой воды.

Стадия	Лист	Листов
Р	2	

PI-диаграмма трубопроводов сбора дренажей сетевой воды. Система NDB, NDE.

АКЦИОНЕРНОЕ ОБЩЕСТВО ИНСТИТУТ ТЕПЛОЭЛЕКТРОПРОЕКТ Г. МОСКВА

Согласовано

ОАСУ

Взам. инв. №

Подпись и дата

Инв. № подл.

Формат А2