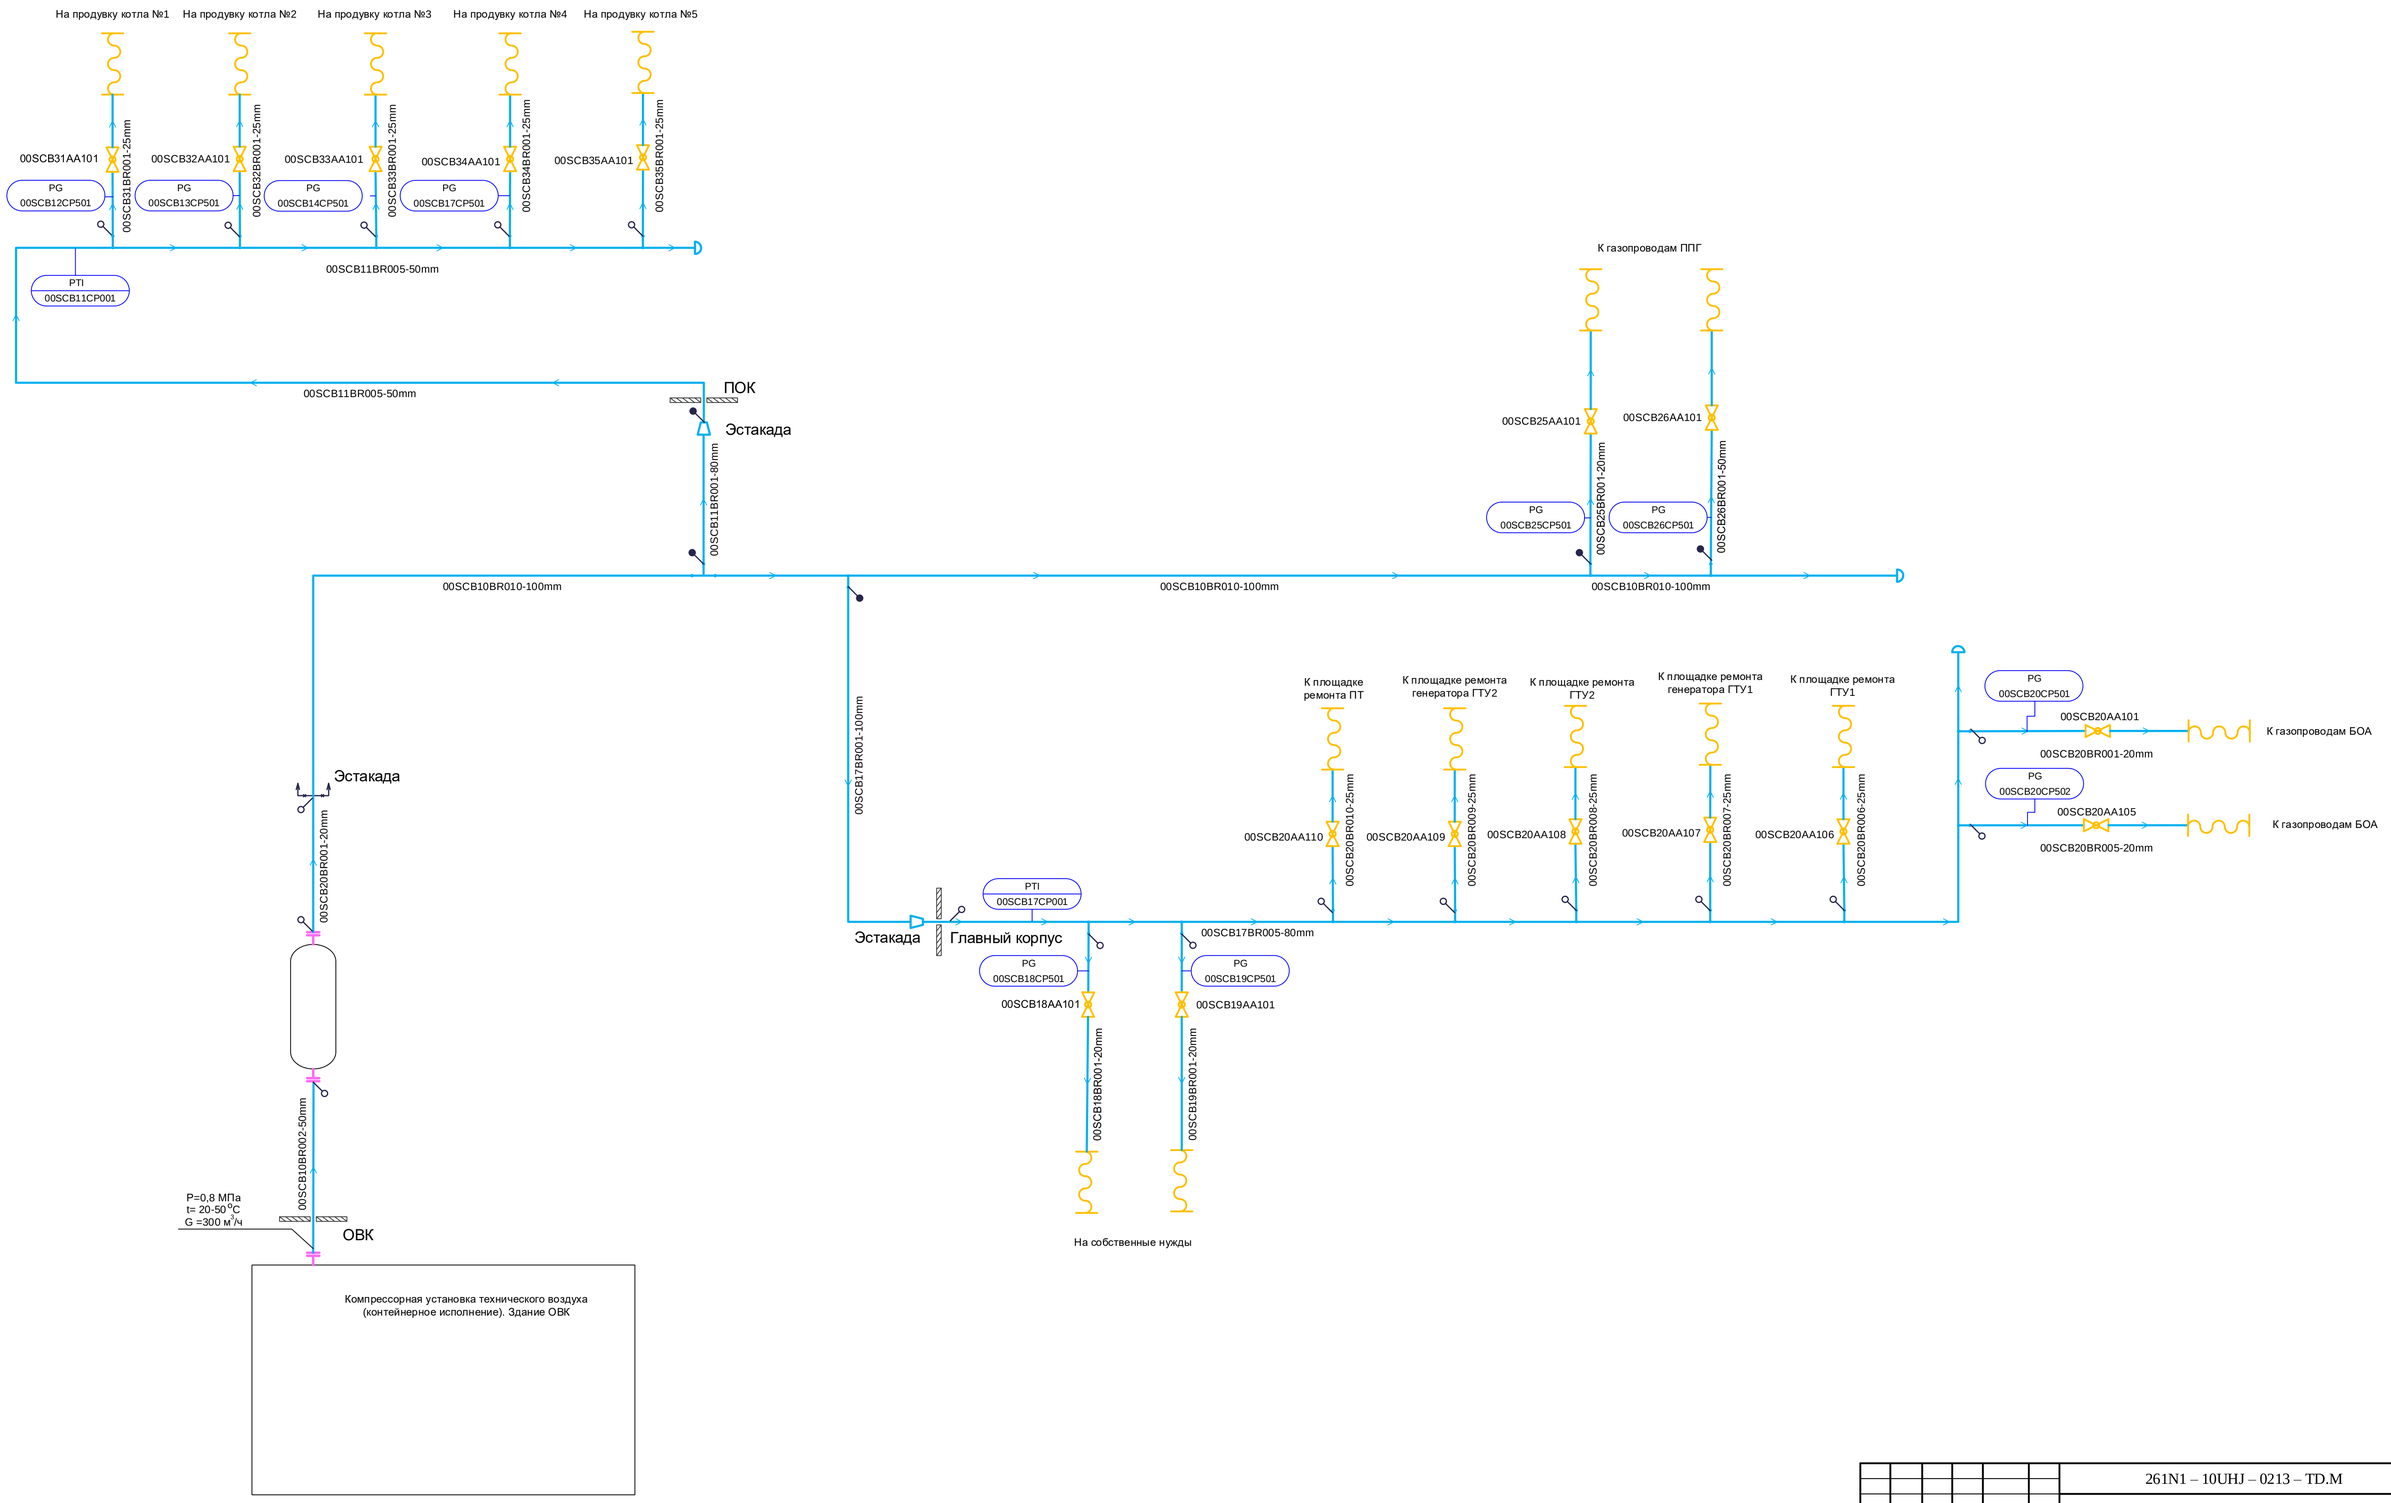

						261N1 – 10UHJ – 0213 – TD.M
1	-	Зам	52-26		01.26	Южно-Якутская ТЭС. Рабочая документация
Изм.	Кол.уч	Лист	№ док.	Подп.	Дата	
Разработал		Полянская			01.26	Главный корпус. PI-Диаграмма трубопроводов сжатого воздуха
Проверил		Сергеева			01.26	
Н. контр.		Черемушкина			01.26	PI-диаграмма трубопроводов сжатого воздуха. Система SCB

Стадия	Лист	Листов
Р	2	

АКЦИОНЕРНОЕ ОБЩЕСТВО ИНСТИТУТ ТЕПЛОЭЛЕКТРОПРОЕКТ Г. МОСКВА

Согласовано

ОАСУ

Взам. инв. №

Подпись и дата

Инв. № подл.

Формат А1