Перечень оборудования

Поз.	Маркировка	Наименование	Кол.	Характеристики	Примечание
1	00GAC11AP001 00GAC12AP001	Насос исходной воды	2	G = 55 М^3/Ч H = 65 м	
2	00GAC15AC001 00GAC16AC001	Подогреватель сырой воды подпитки теплосети	2	1.21 Гкал/ч	

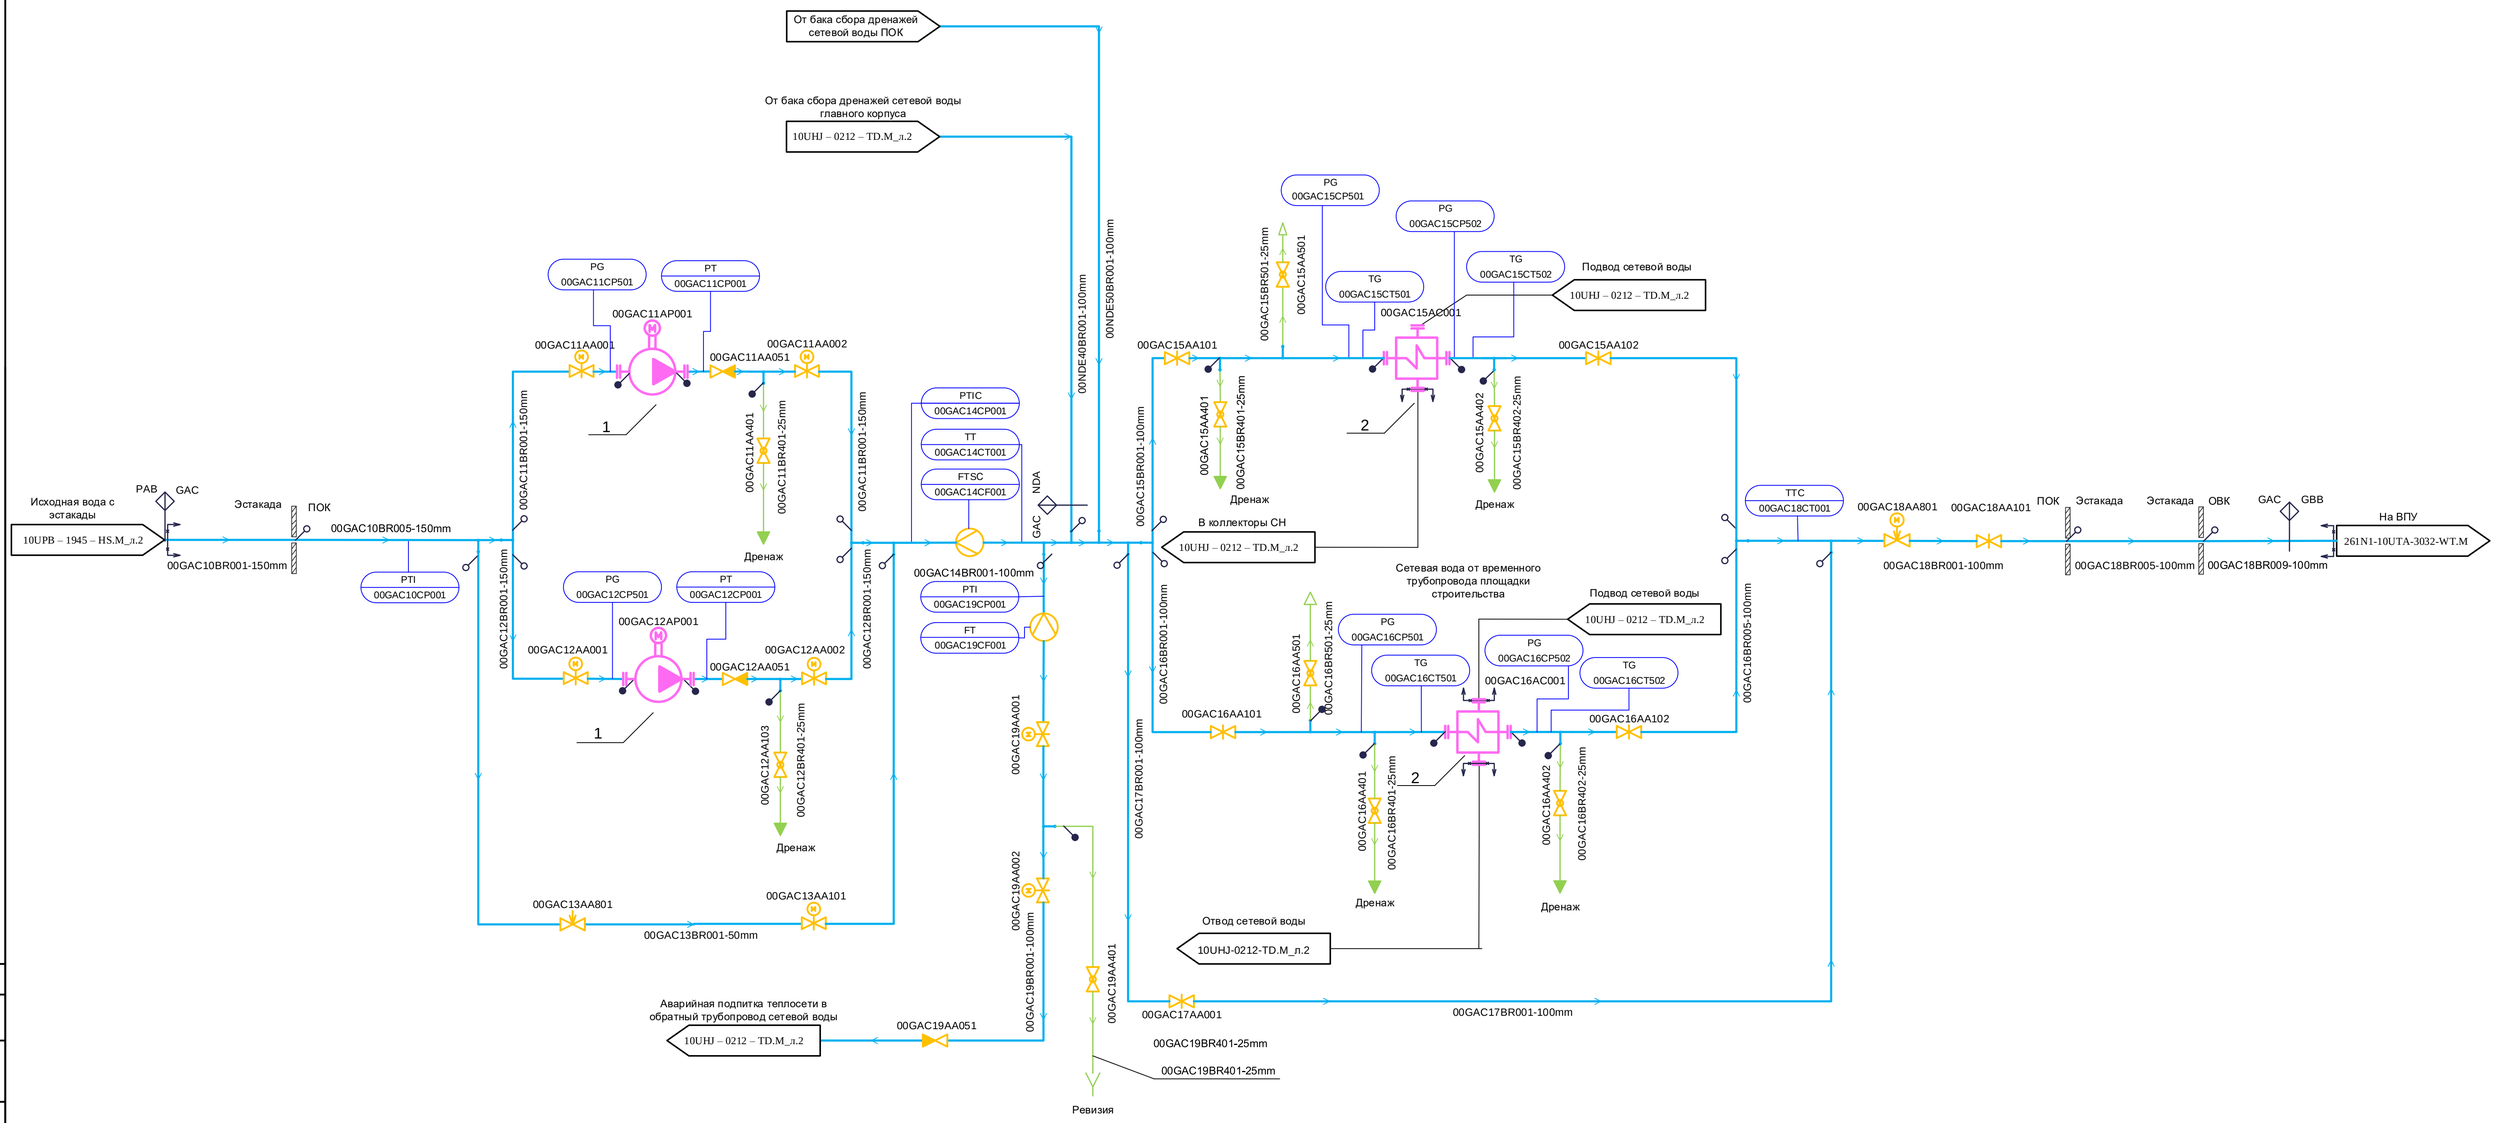

Изм.	Кол.уч	Лист	№ док.	Подп.	Дата
Разработал		Харитонов			
Проверил		Лаврякова			
Глав. спец.		Супонина			
Н. контр.		Черемушкина			

261N1 – 10UTH – 0215 – TD.M

Южно-Якутская ТЭС. Рабочая документация

Пуско-отопительная котельная.
PI-диаграмма трубопроводов сырой воды.

Стадия	Лист	Листов
Р	1	

PI-диаграмма трубопроводов сырой воды.
Система LBA

АКЦИОНЕРНОЕ ОБЩЕСТВО ИНСТИТУТ ТЕПЛОЭЛЕКТРОПРОЕКТ г. МОСКВА

Согласовано

Взам. инв. №

Подпись и дата

Инв. № подл.

Формат А1