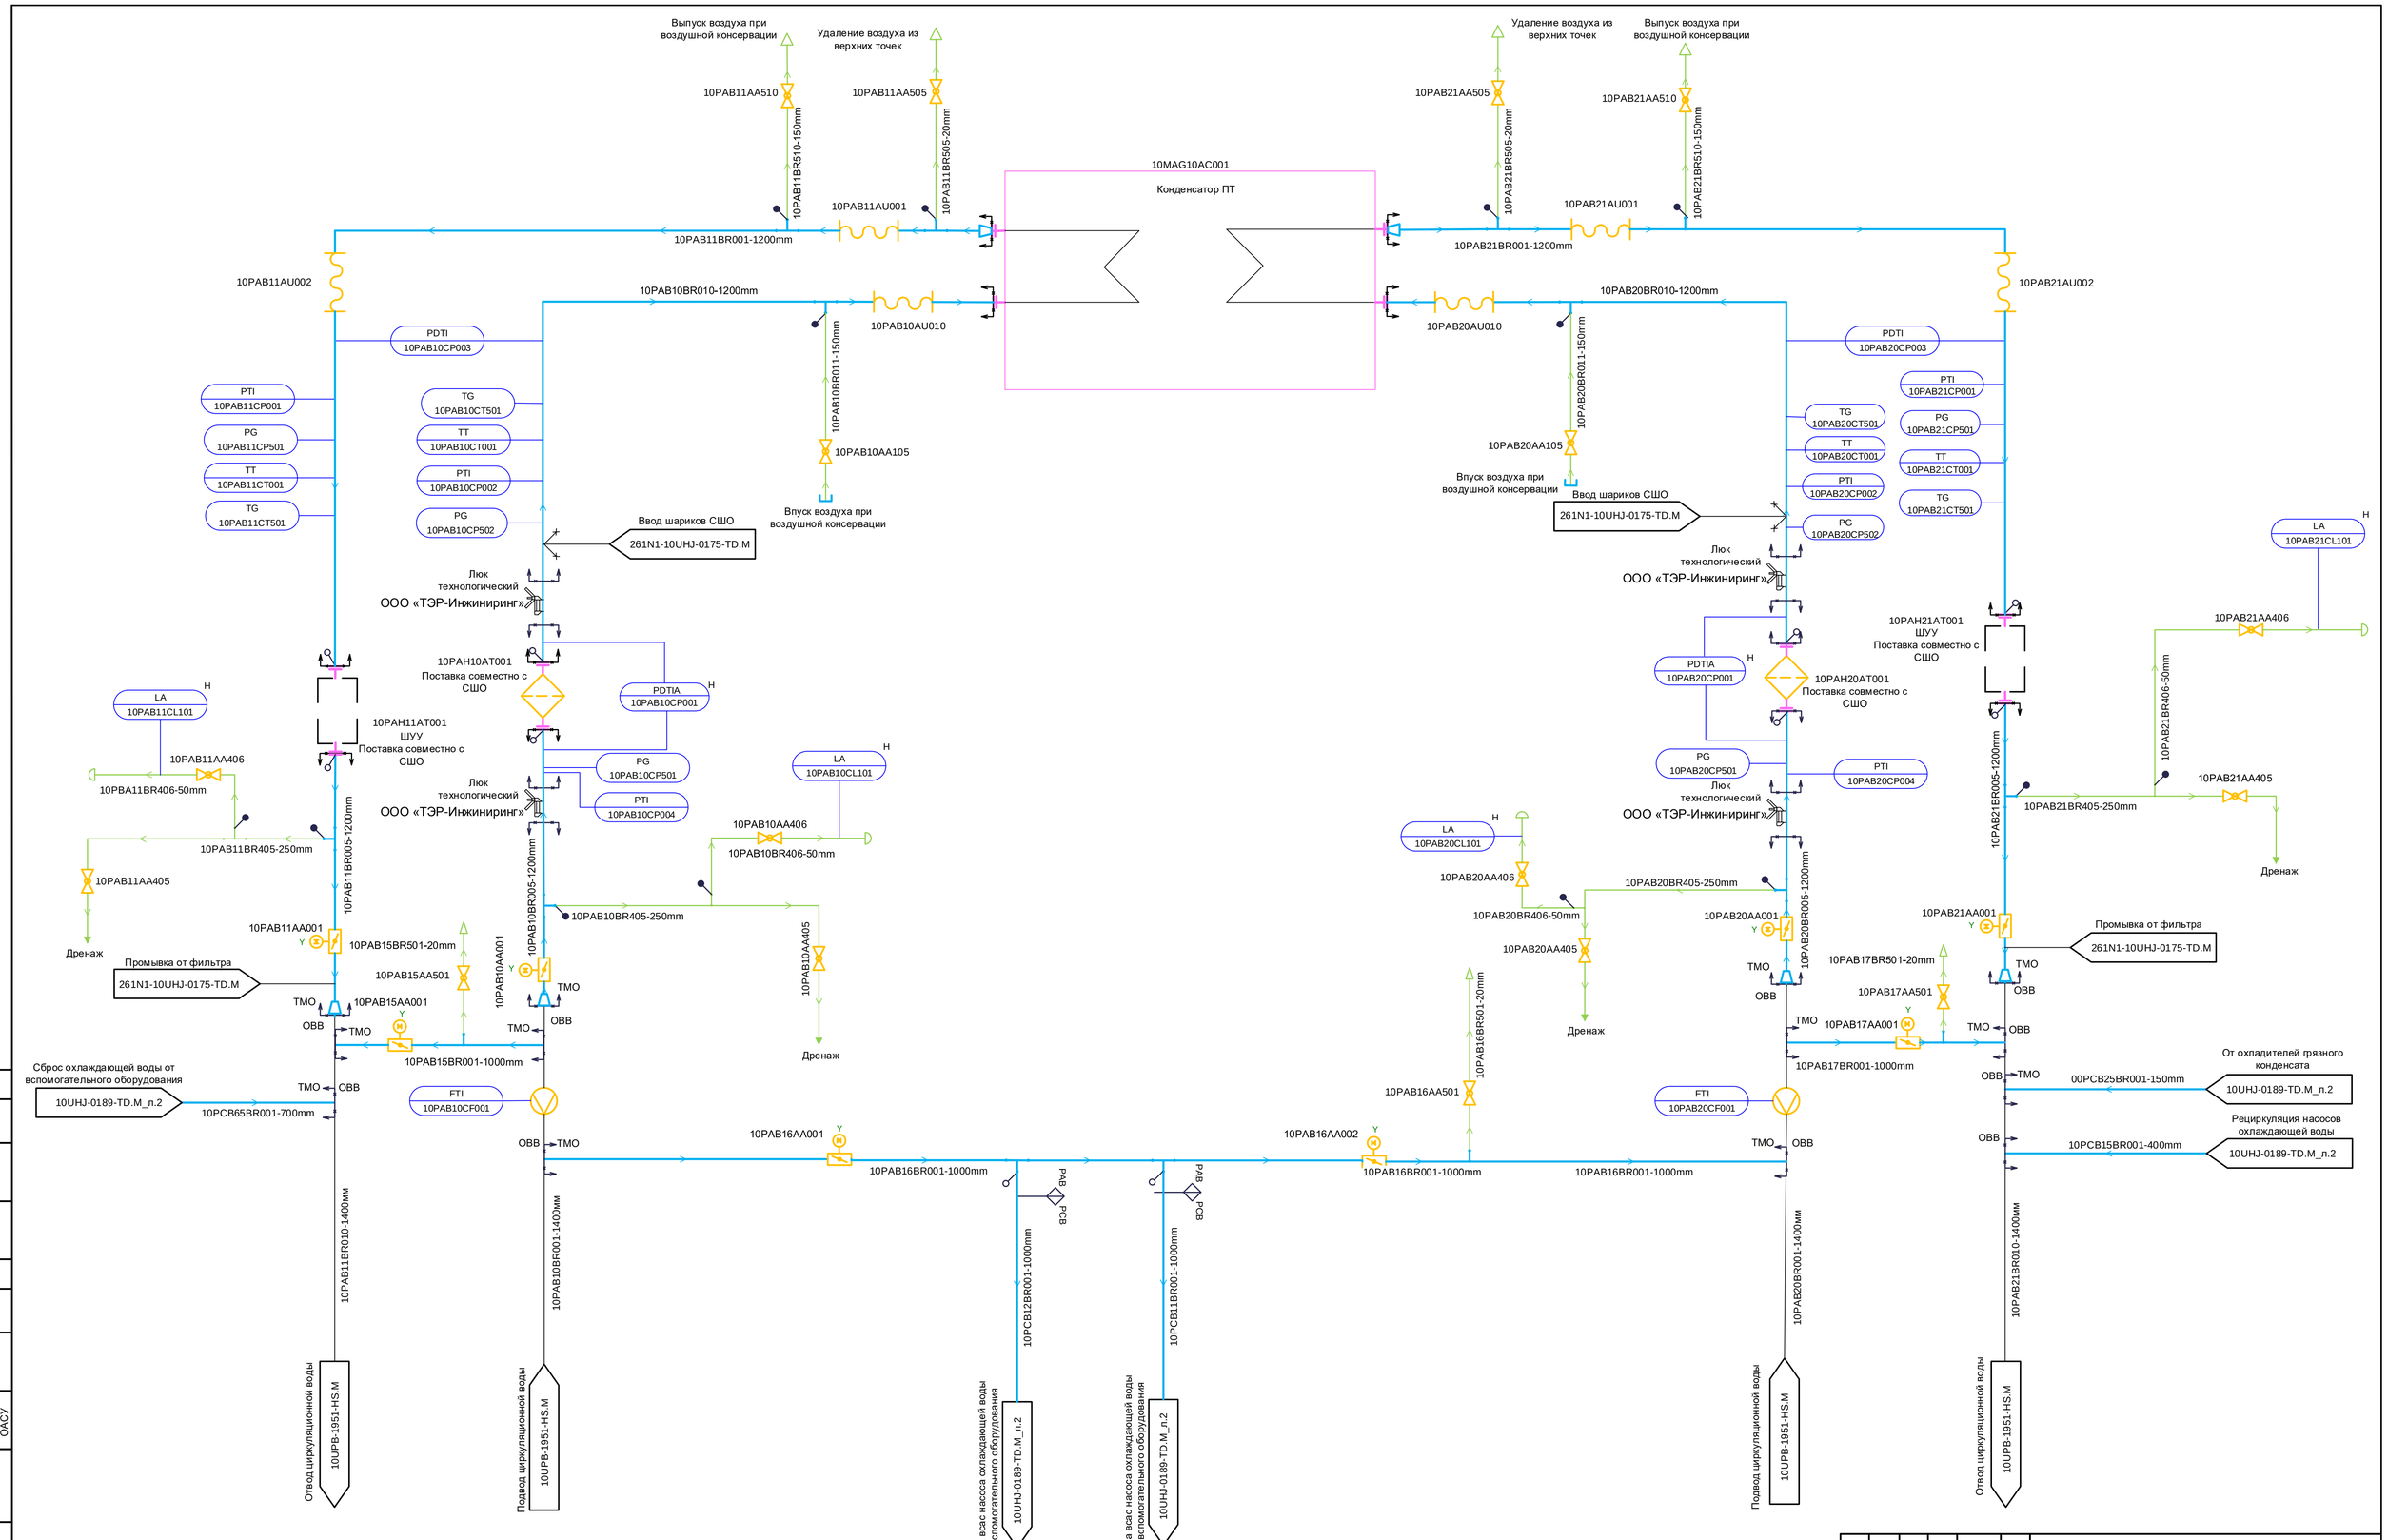

2		Зам.	2613-25		06.25	261N1-10UHJ-0217-TD.M	
1		Зам.	3612-24		12.24	Южно-Якутская ТЭС. Рабочая документация.	
Изм.	Кол.уч	Лист	№ док.	Подп.	Дата		
Разработал		Чехиркина				Главный корпус. P&I-диаграмма трубопроводов циркуляционной охлаждающей воды.	Стадия: Р; Лист: 2; Листов:
Проверил		Лаврякова					
Проверил		Дильман					
Н. контр.		Черемушкина				P&I-диаграмма трубопроводов циркуляционной охлаждающей воды. Система РАВ.	АКЦИОНЕРНОЕ ОБЩЕСТВО ИНСТИТУТ ТЕПЛОЭЛЕКТРОПРОЕКТ г. МОСКВА

Согласовано

ОАСУ

Взам. инв. №

Подпись и дата

Инв. № подл.

Формат А1