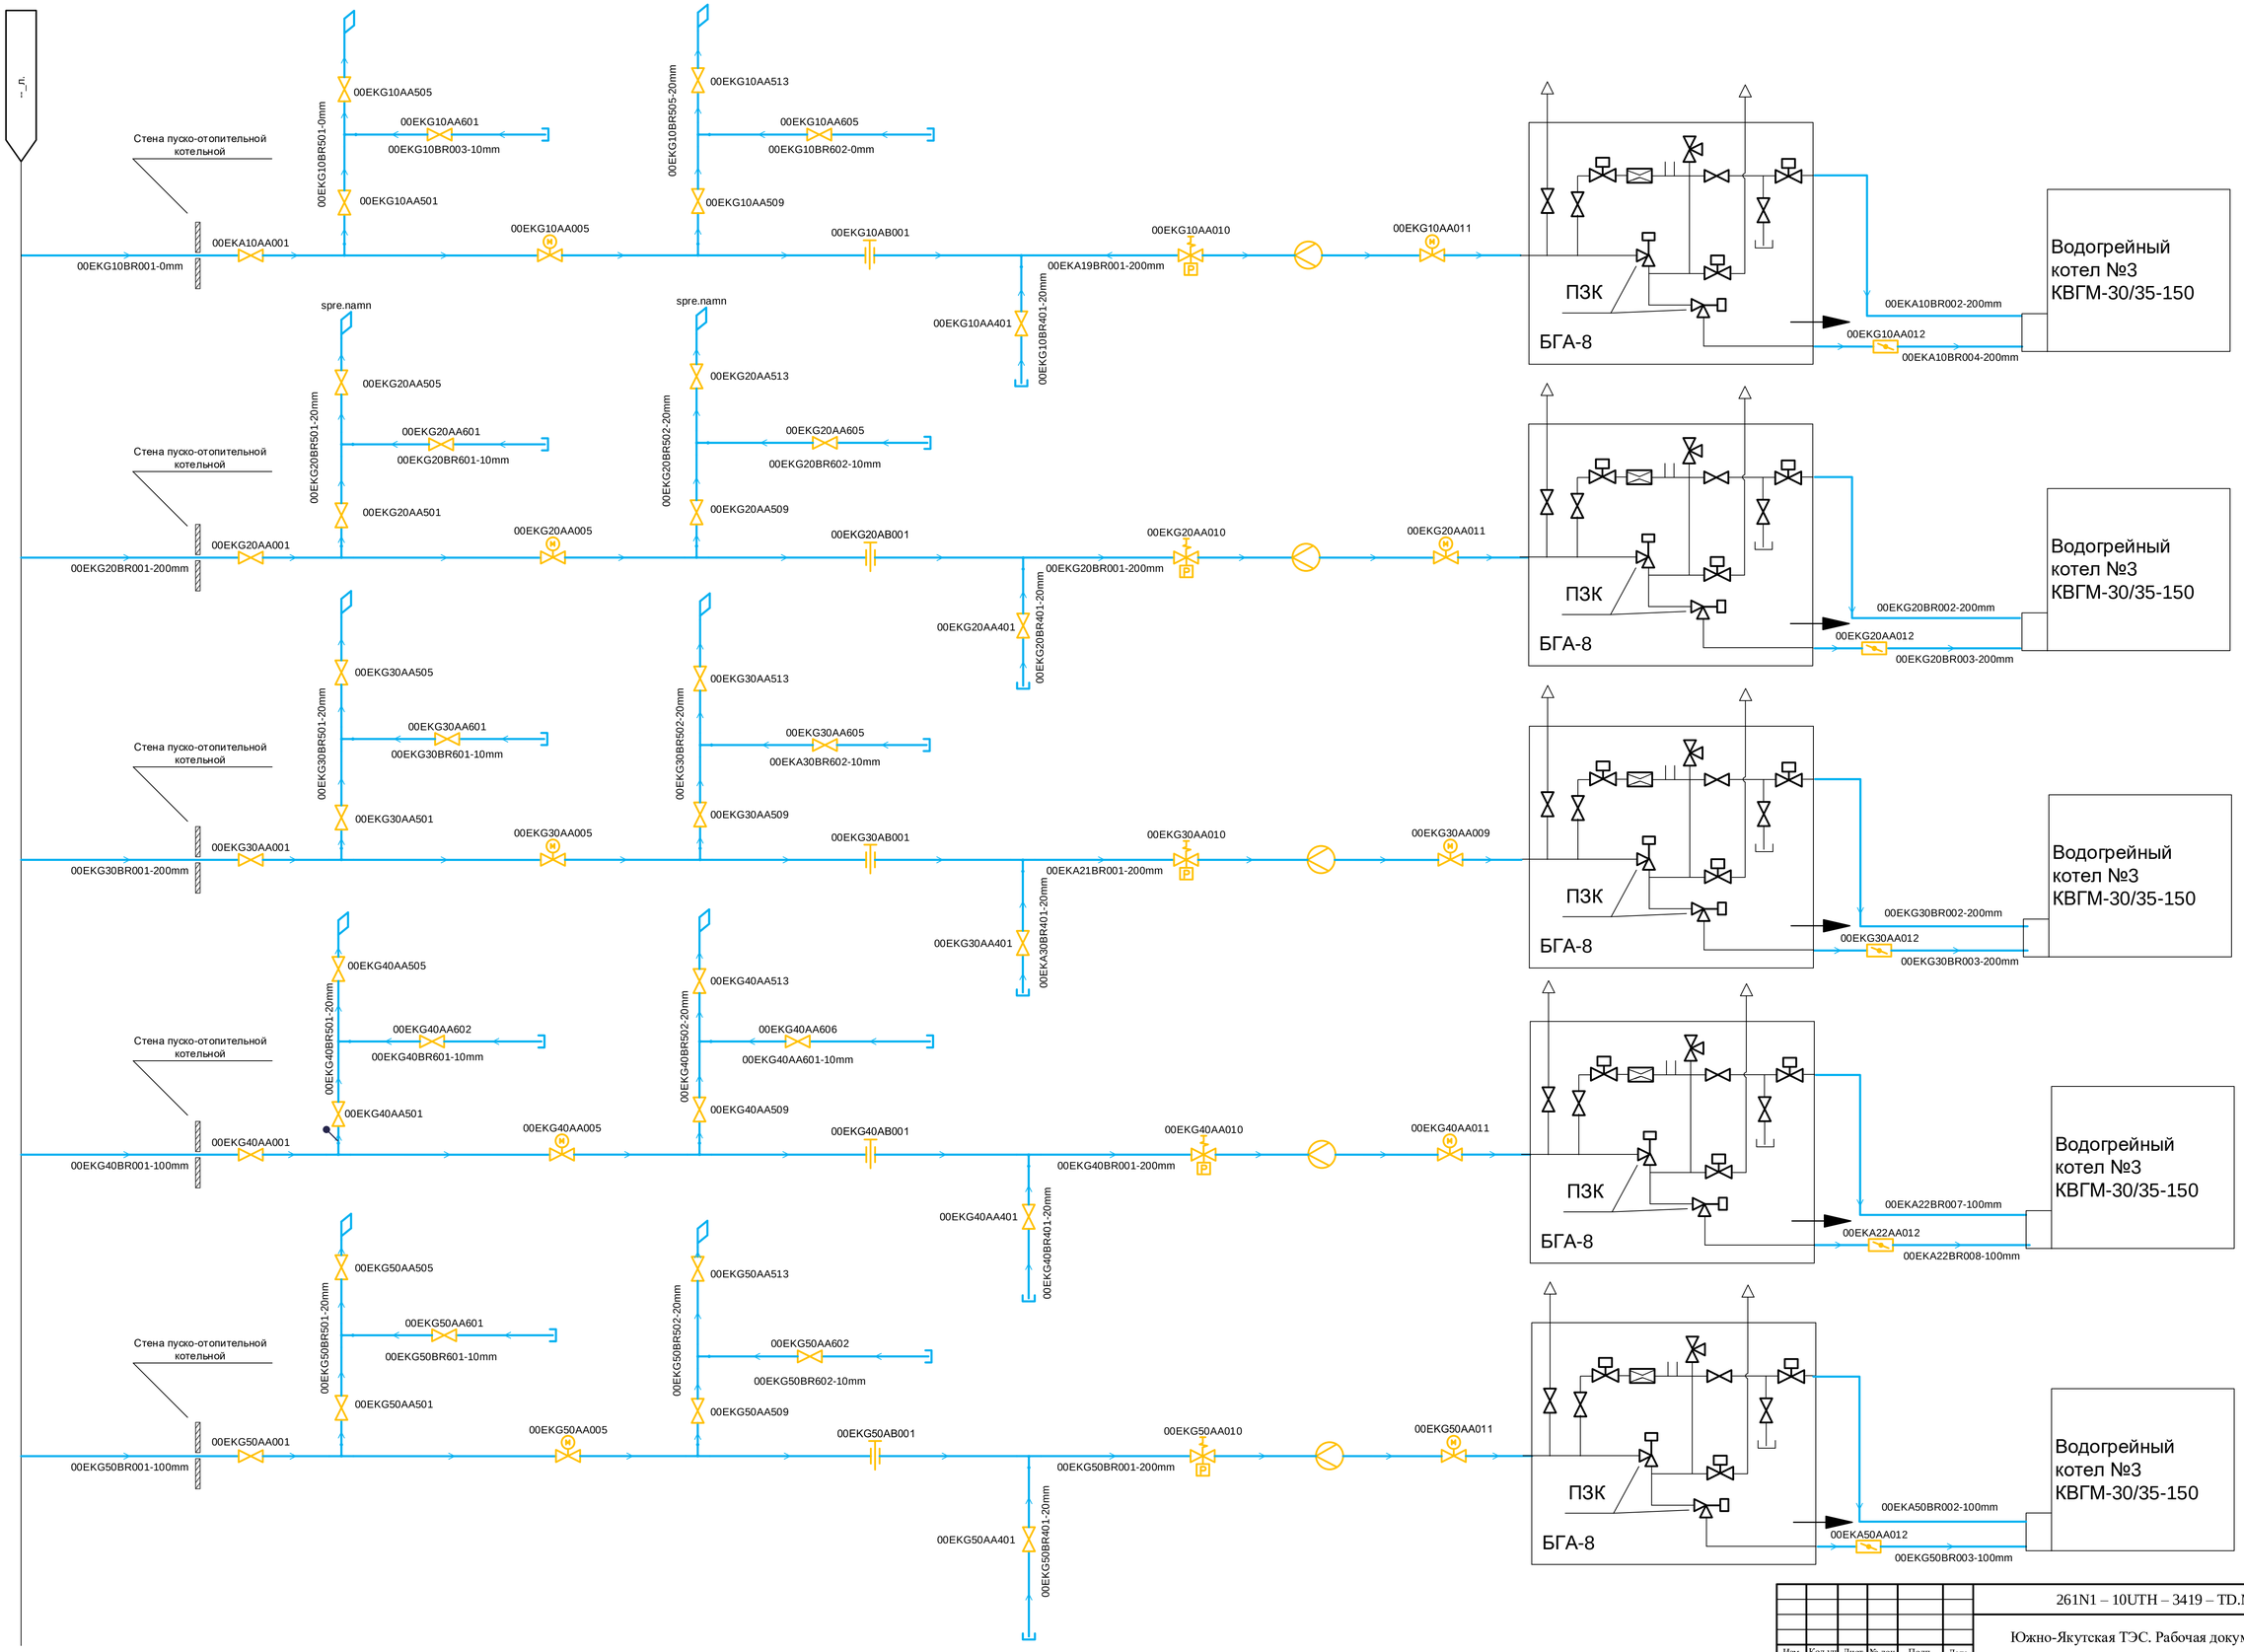

						261N1 – 10UTH – 3419 – TD.M		
						Южно-Якутская ТЭС. Рабочая документация		
Изм.	Кол.уч	Лист	№ док.	Подп.	Дата			
Разработал		Харитонов				PI – Диаграмма трубопроводов газового топлива. Локальное задание	Стадия	Лист	Листов
Проверил		Лаврякова					Р	1	
Н. контр.		Черемушкина				PI – Диаграмма трубопроводов газового топлива. Система EKG.	АКЦИОНЕРНОЕ ОБЩЕСТВО ИНСТИТУТ ТЕПЛОЭЛЕКТРОПРОЕКТ Г. МОСКВА		

Согласовано

ОАСУ

Взам. инв. №

Подпись и дата

Инв. № подл.

Формат А1