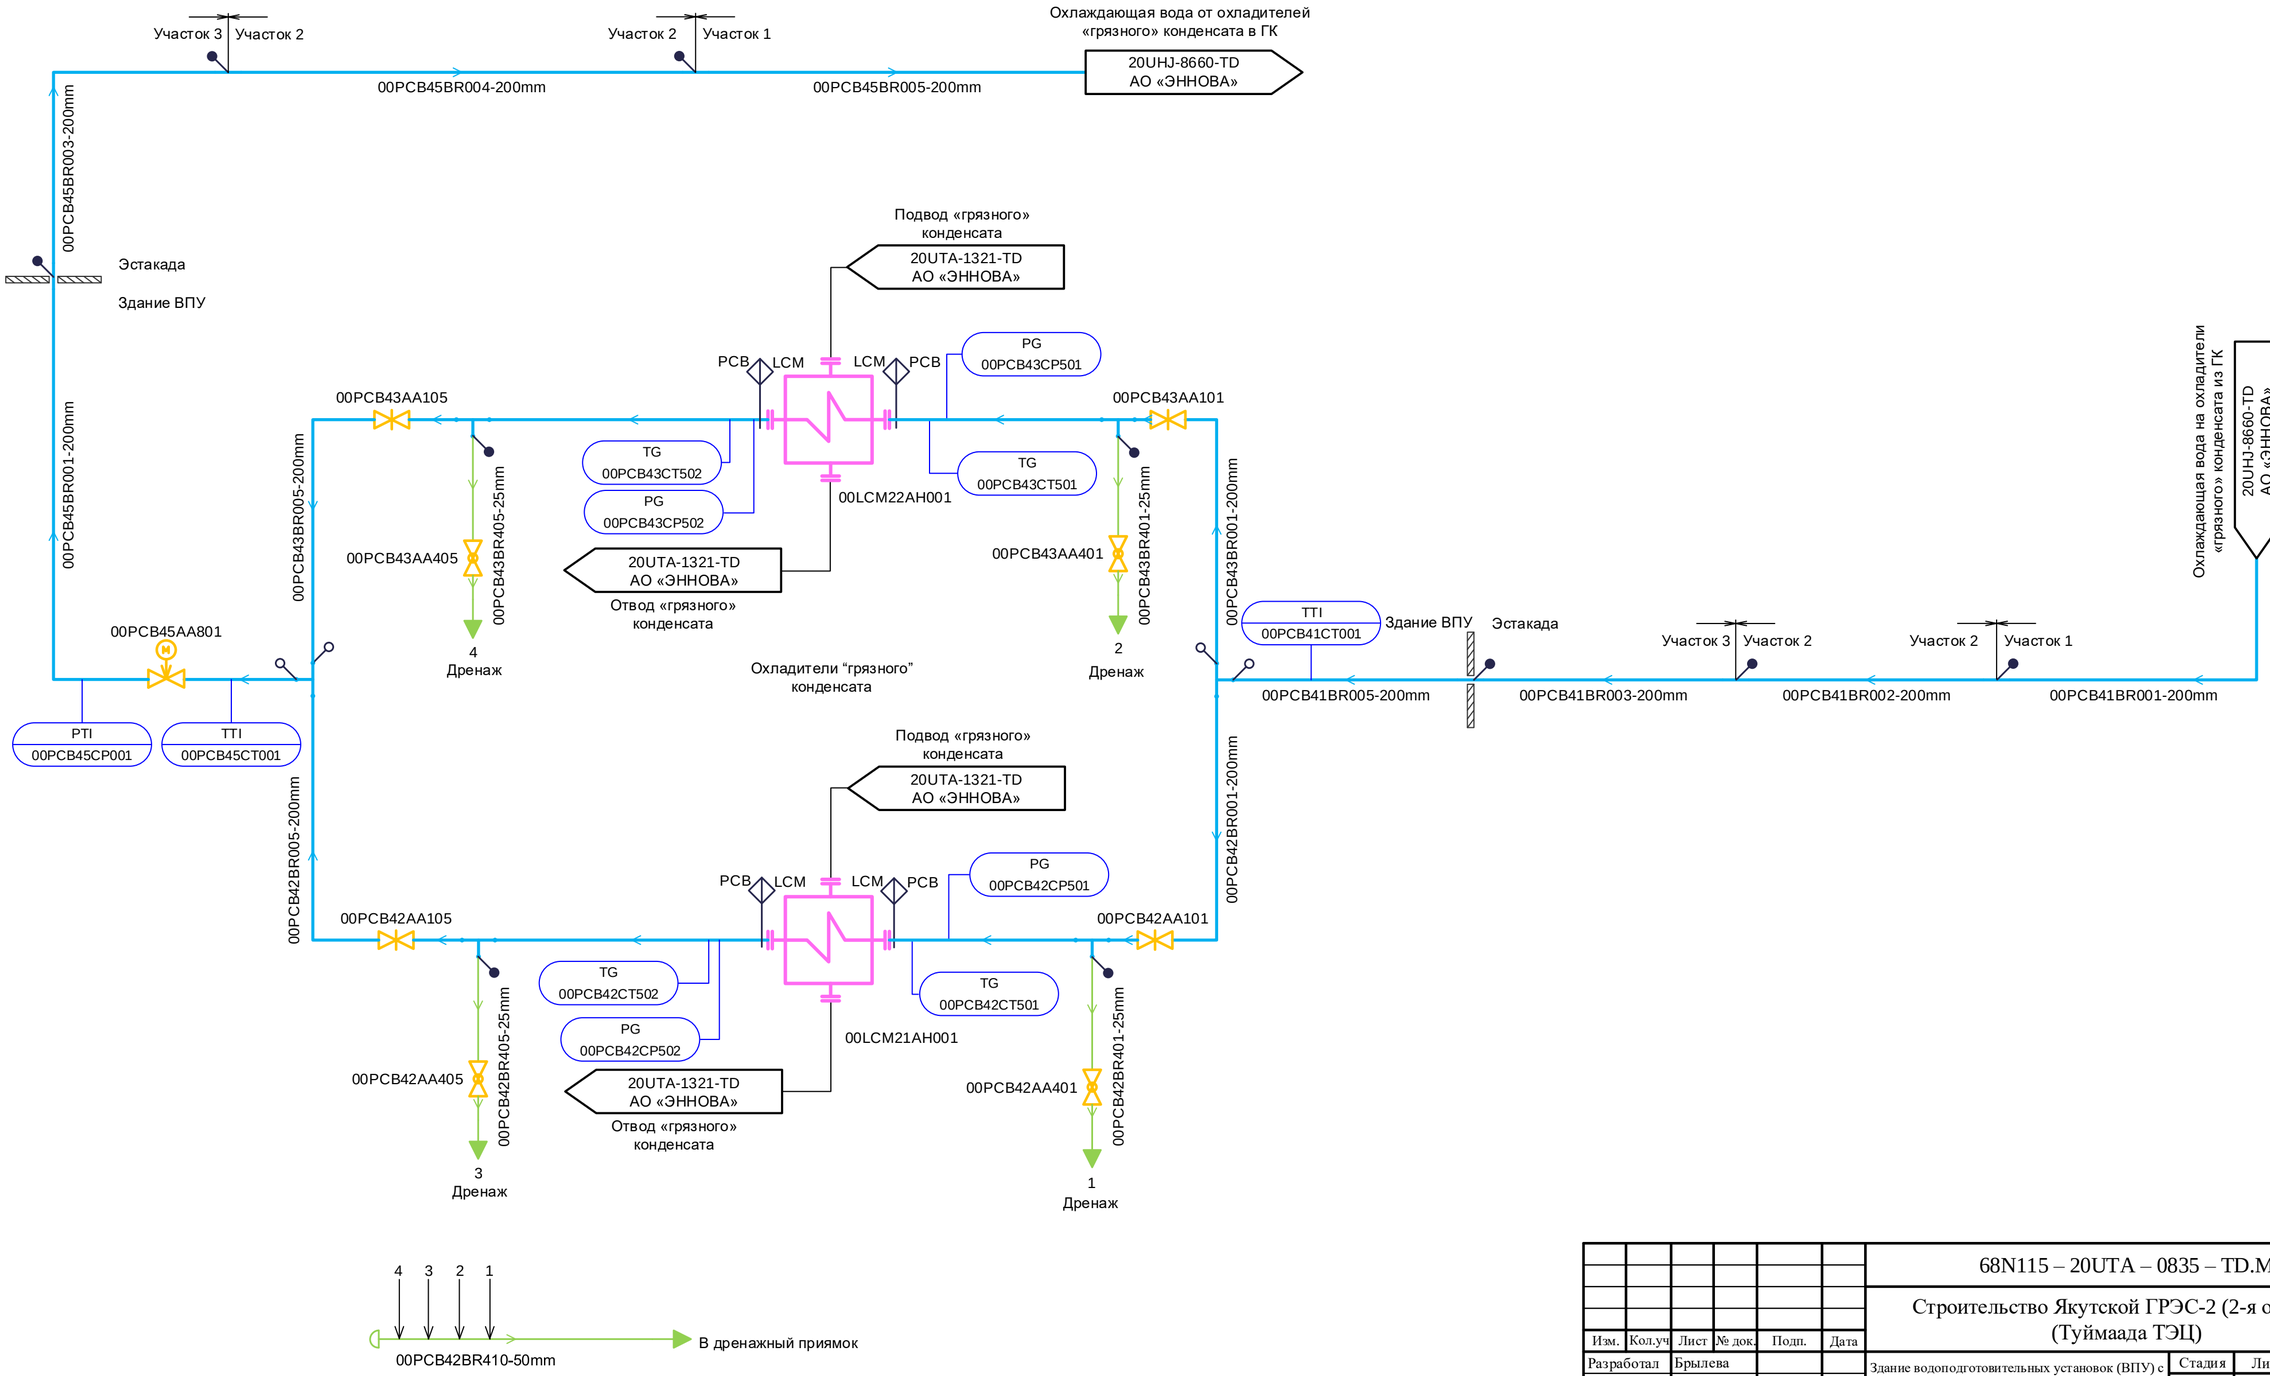

Изм.	Кол.уч	Лист	№ док.	Подп.	Дата	68N115 – 20UTA – 0835 – TD.M
						Строительство Якутской ГРЭС-2 (2-я очередь) (Туймаада ТЭЦ)
Разработал		Брылева				Здание водоподготовительных установок (ВПУ) с насосным и баковым хозяйством. PI-диаграмма трубопроводов охлаждающей воды
Проверил		Машков				Стадия: Р; Лист: 2; Листов:
Гл.спец.		Калабушкина				
Н. контр.		Черемушкина				PI-диаграмма трубопроводов охлаждающей воды. Система PCB.

АКЦИОНЕРНОЕ ОБЩЕСТВО ИНСТИТУТ ТЕПЛОЭЛЕКТРОПРОЕКТ г. МОСКВА

Согласовано
ОАСУ Савенкова

Взам. инв. №
Подпись и дата
Инв. № подл.

Формат А2