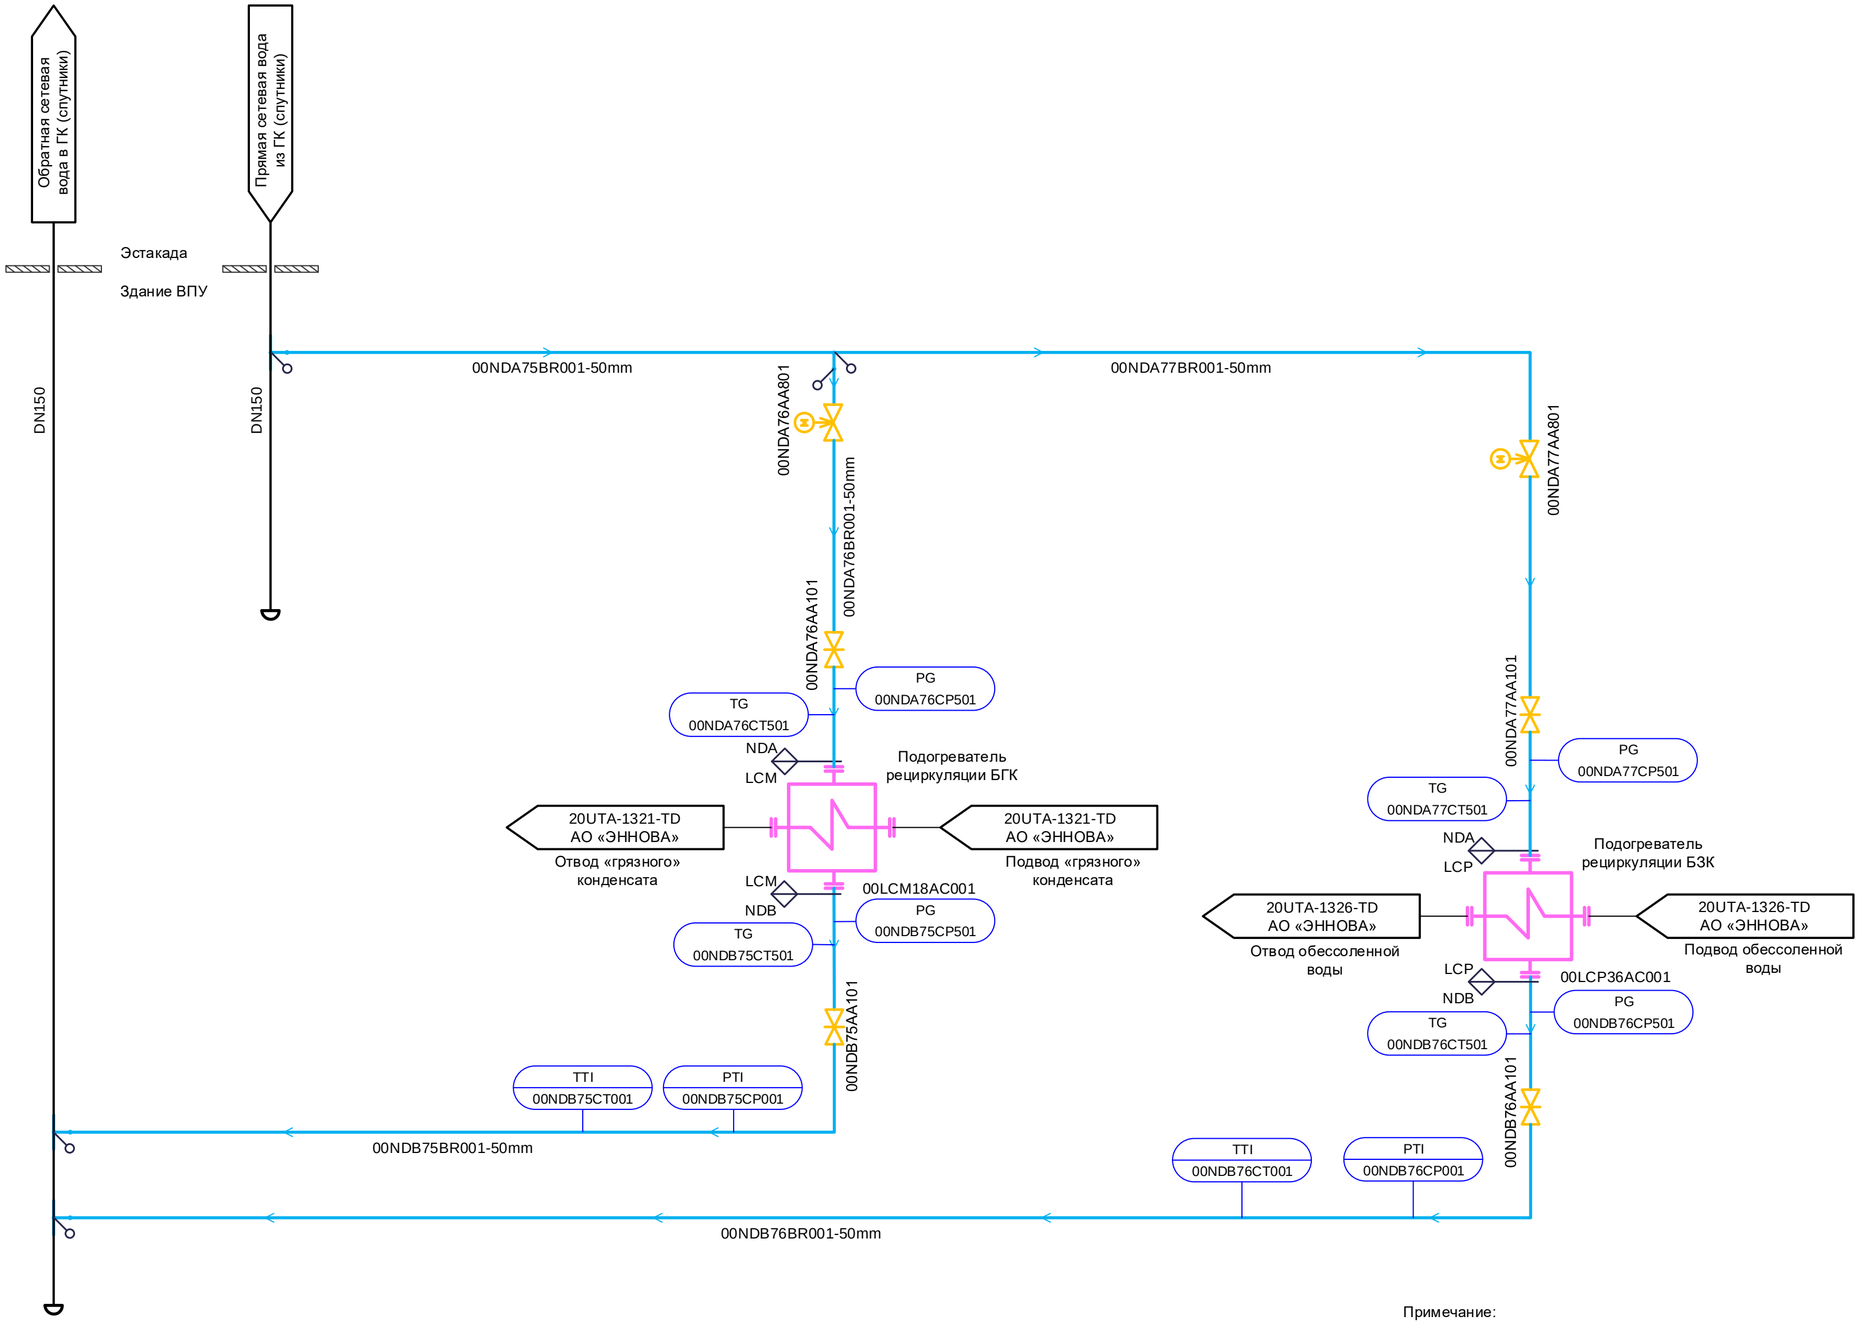

Примечание:
Дренажи и воздушники будут добавлены после выполнения рабочей документации.

Изм.	Кол.уч	Лист	№ док.	Подп.	Дата
Разработал		Брылева			
Проверил		Машков			
Гл.спец.		Калабушкина			
Н. контр.		Черемушкина			

68N115 – 20UTA – 0843 – TD.M

Строительство Якутской ГРЭС-2 (2-я очередь) (Туймаада ТЭЦ)

Здание водоподготовительных установок (ВПУ) с насосным и баковым хозяйством. PI-диаграмма трубопроводов охлаждающей воды

Стадия	Лист	Листов
Р	2	

PI-диаграмма трубопроводов сетевой воды. Система NDA, NDB.

АКЦИОНЕРНОЕ ОБЩЕСТВО ИНСТИТУТ ТЕПЛОЭЛЕКТРОПРОЕКТ Г. МОСКВА

Согласовано
ОАСУ Савенкова

Взам. инв. №
Подпись и дата
Инв. № подл.

Формат А2