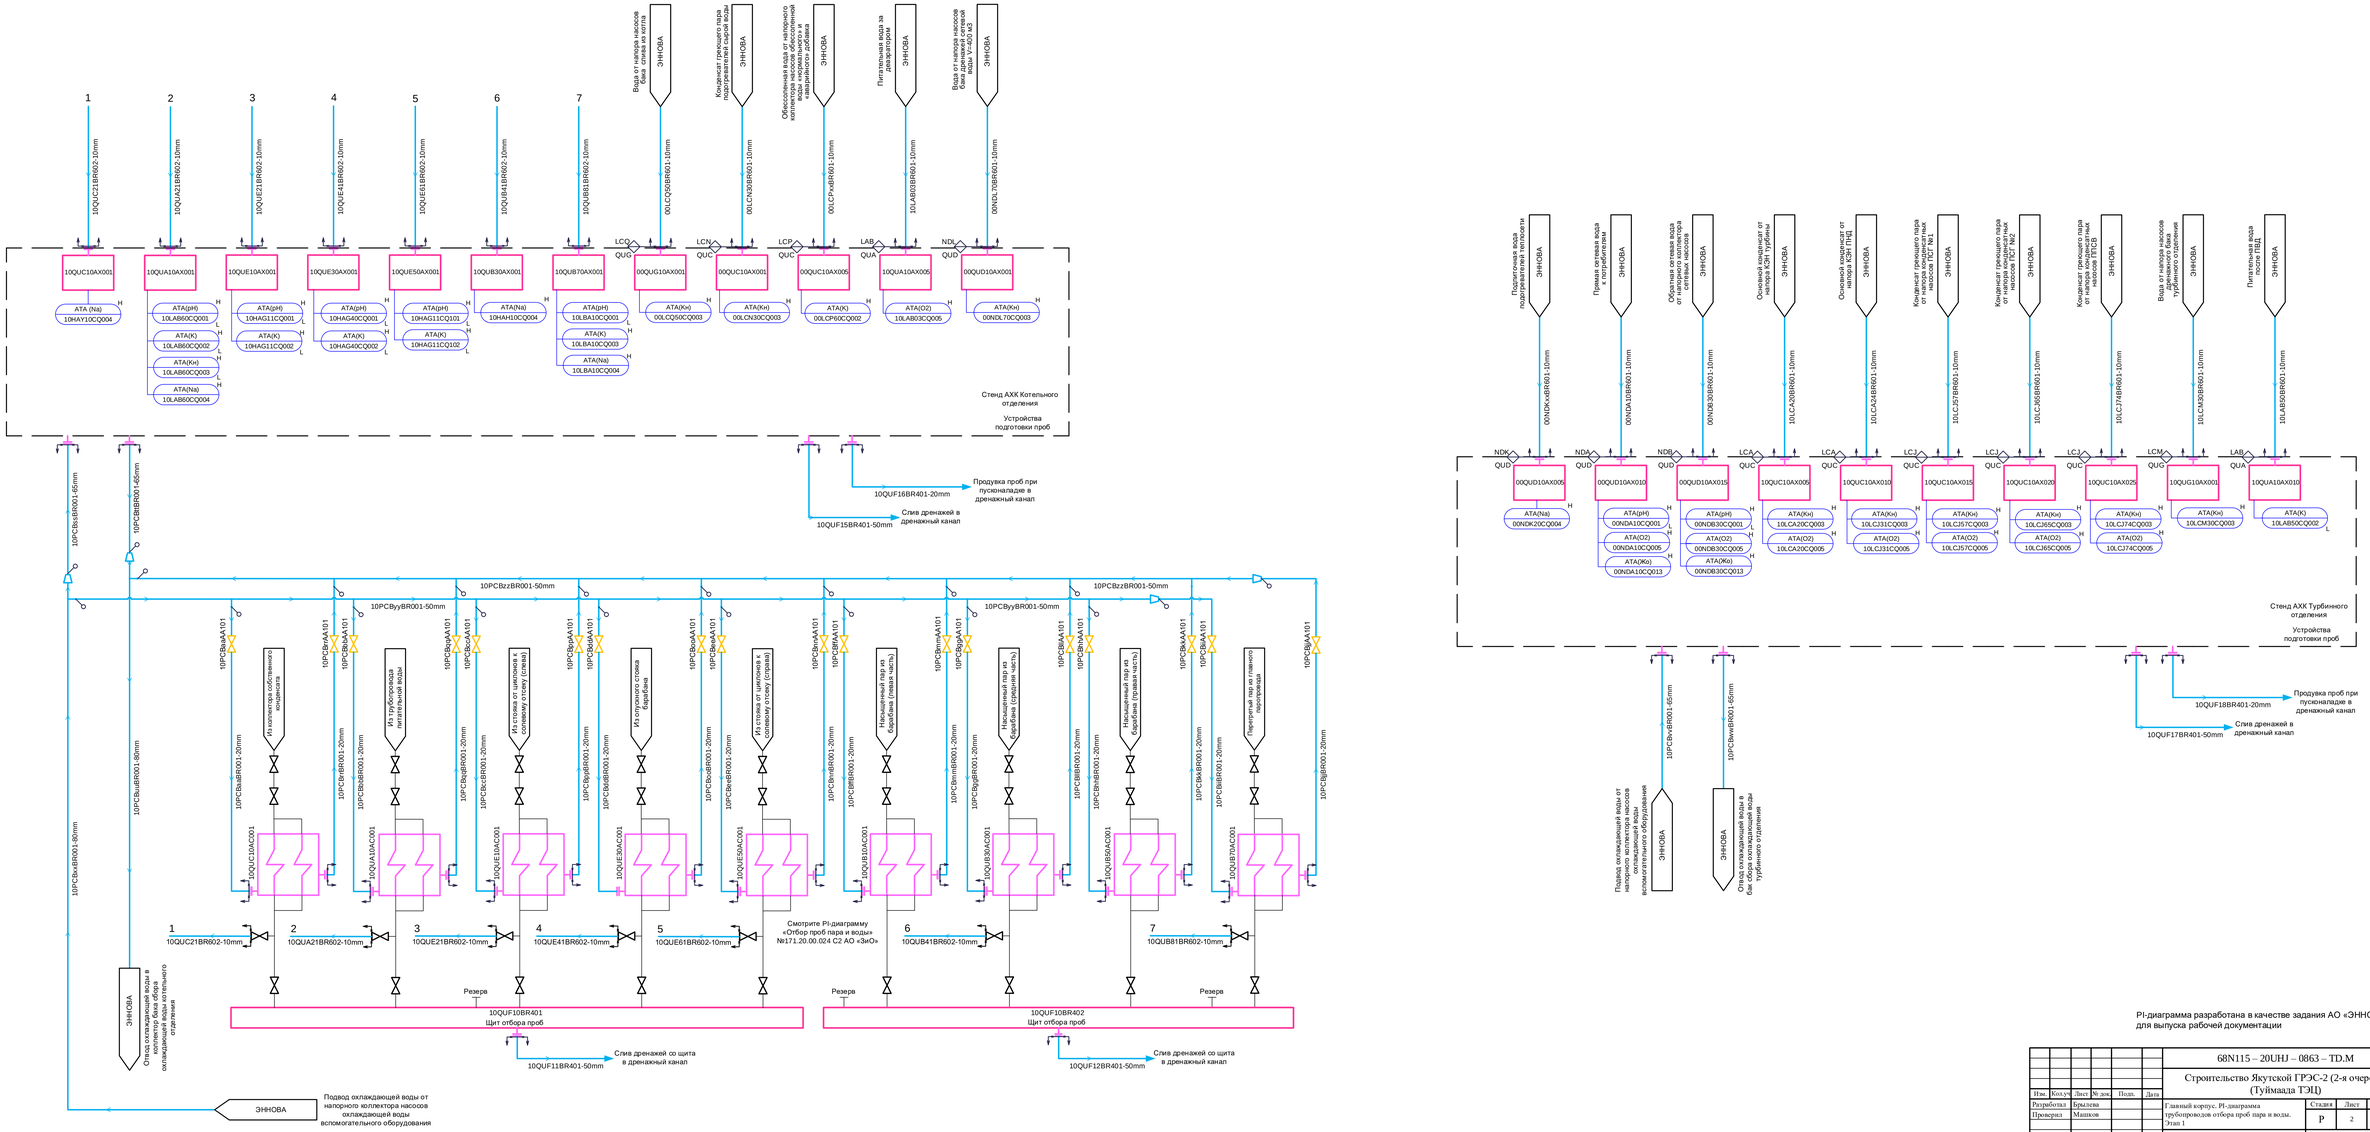

PI-диаграмма разработана в качестве задания АО «ЭННОВА» для выпуска рабочей документации

							68N115 – 20UHJ – 0863 – TD.M		
							Строительство Якутской ГРЭС-2 (2-я очередь) (Туймазда ТЭЦ)		
Изм.	Кол.уч.	Лист	№ док.	Подп.	Дата				
Разработал		Брыкова					Главный корпус. PI-диаграмма трубопроводов отбора проб пара и воды. Этап 1	Стадия	Лист	Листов
Проверил		Машков						Р	2	
Н. контр.		Черемушкин					PI-диаграмма трубопроводов отбора проб пара и воды. Этап 1. Система QU, PCB.	ОБЩЕСТВО С ОГРАНИЧЕННОЙ ОТВЕТСТВЕННОСТЬЮ «ЭНЕРГОСЕТЬПРОЕКТ» МОСКВА	

Согласовано

Взам. инв. №

Подпись и дата

Инв. № подл.

Формат А2х3