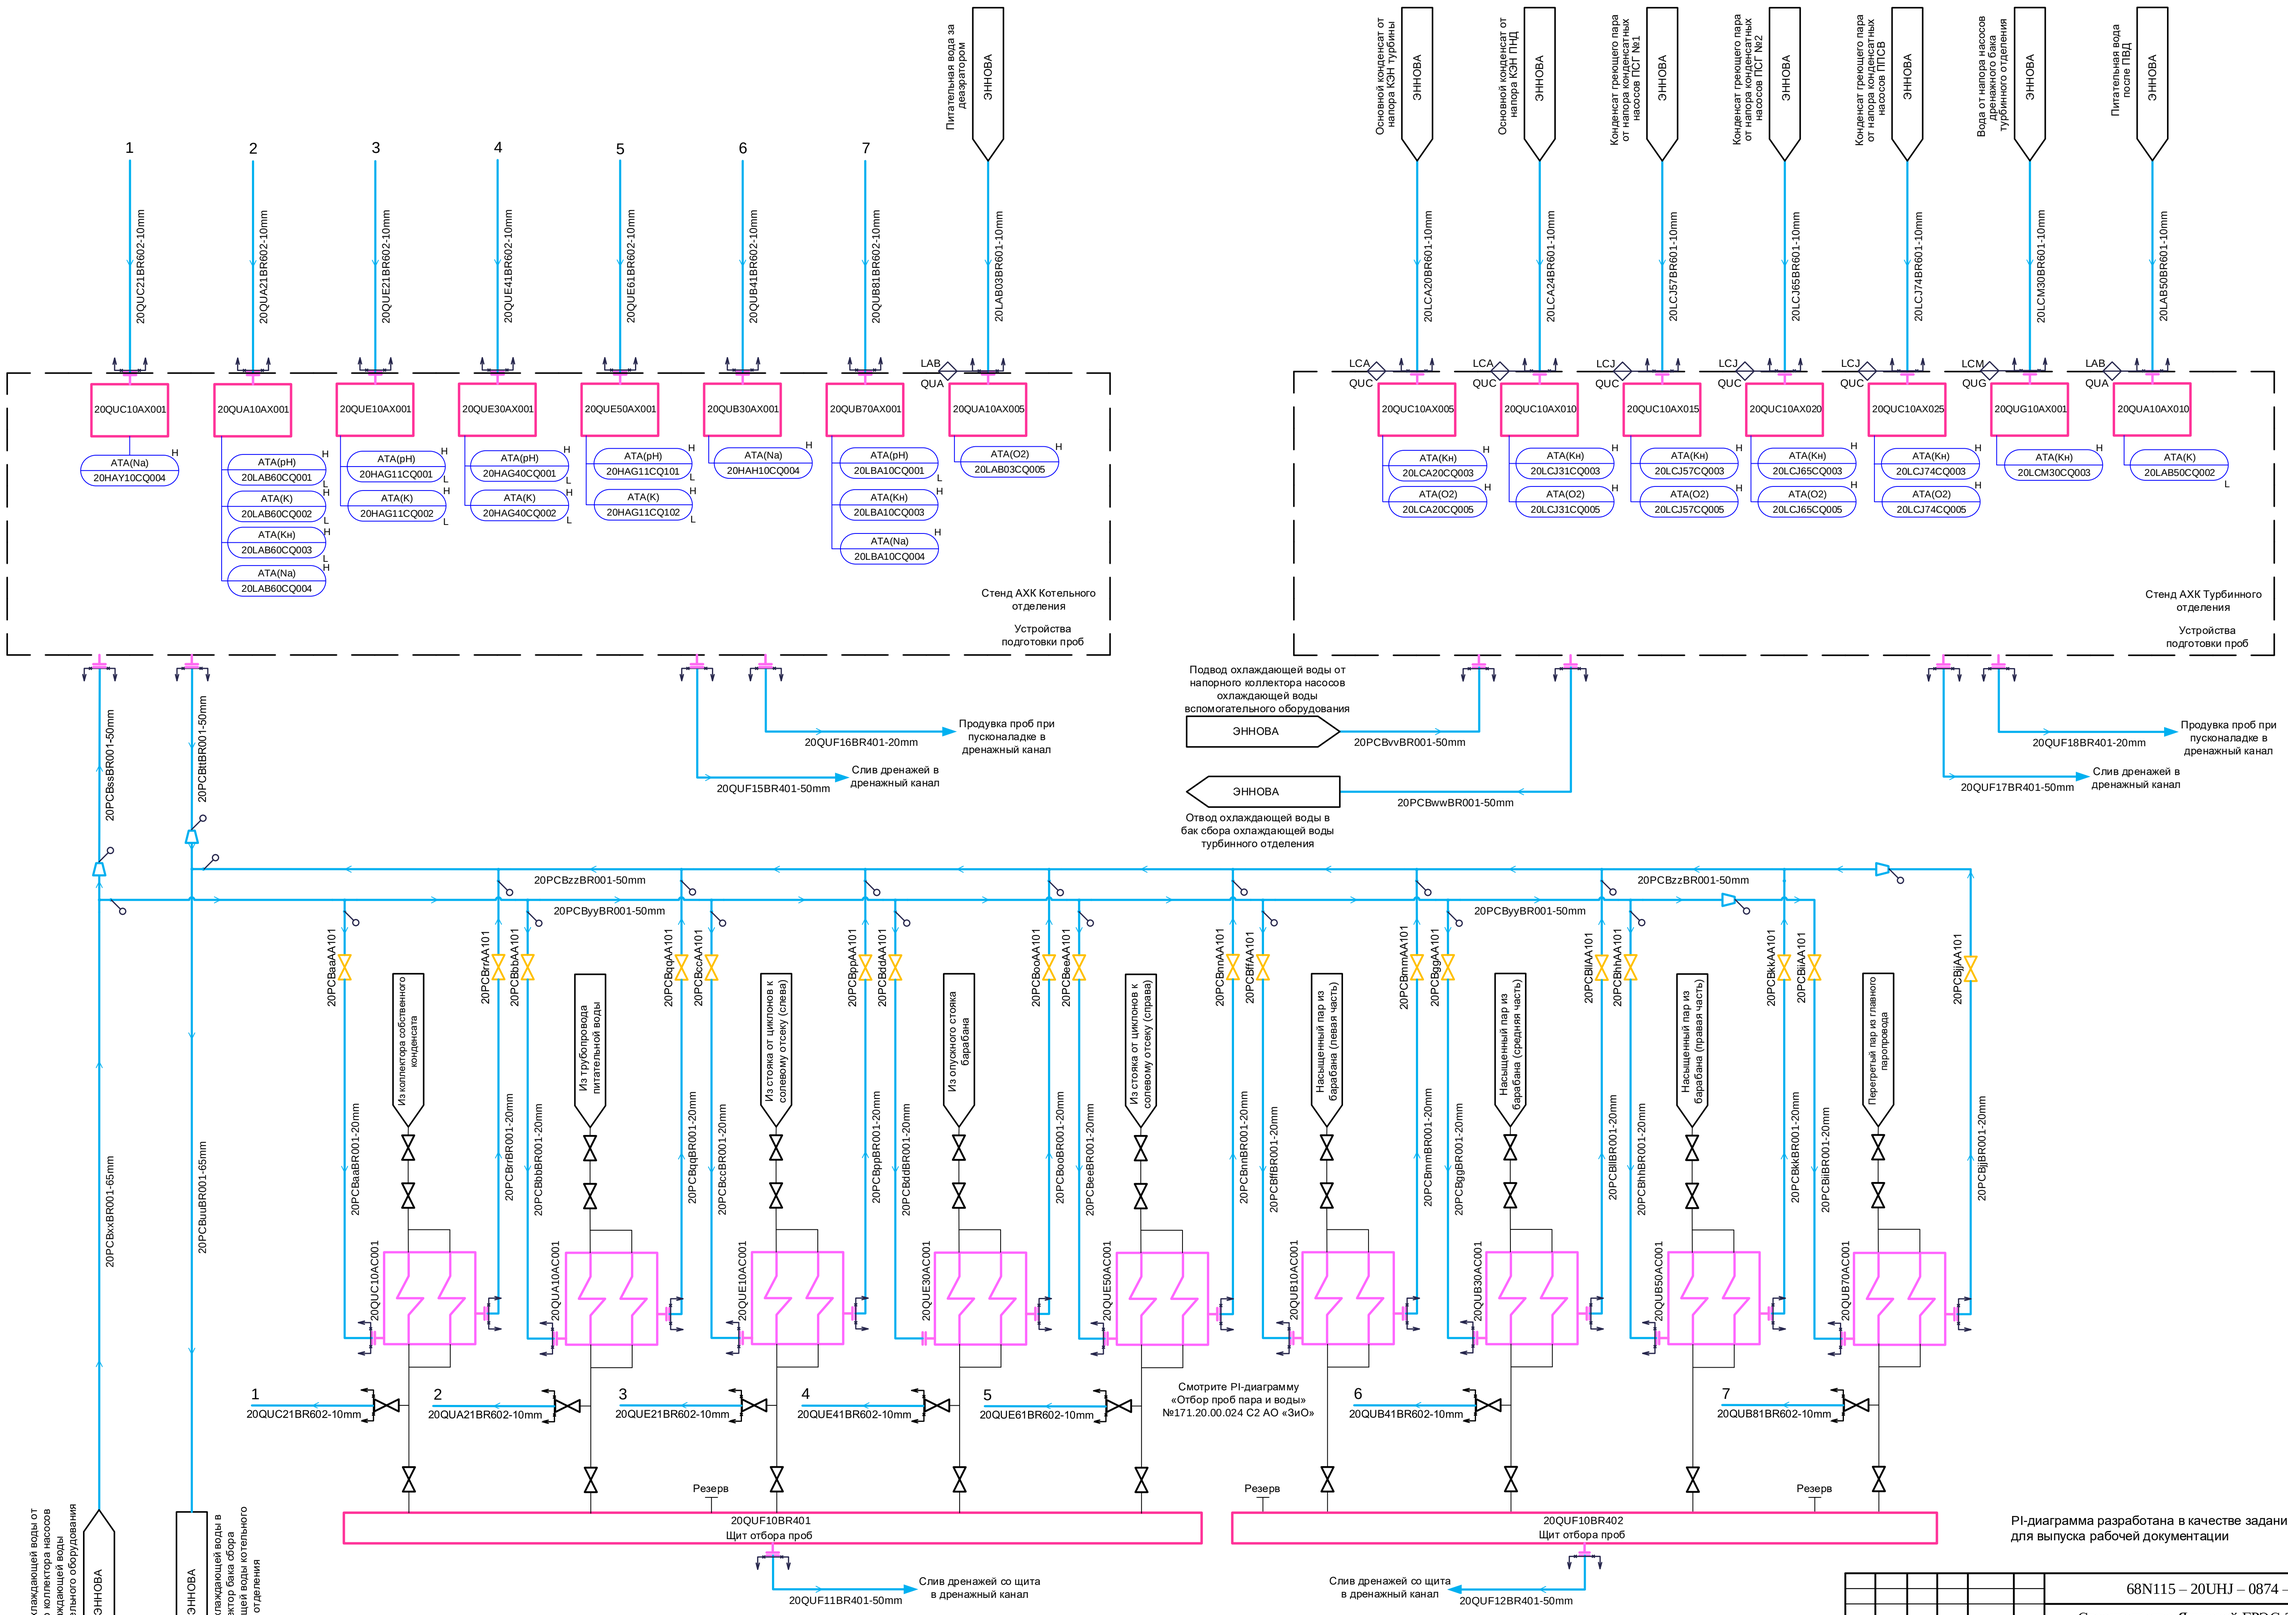

PI-диаграмма разработана в качестве задания АО «ЭННОВА» для выпуска рабочей документации

Изм.	Кол.уч	Лист	№ док.	Подп.	Дата	68N115 – 20UHJ – 0874 – TD.M
						Строительство Якутской ГРЭС-2 (2-я очередь) (Туймаада ТЭЦ)
Разработал		Брылева				Главный корпус. PI-диаграмма трубопроводов отбора проб пара и воды. Этап 2
Проверил		Машков				Стадия: Р; Лист: 2; Листов:
Н. контр.		Черемушкин				PI-диаграмма трубопроводов отбора проб пара и воды. Этап 2. Системы QU, PCB.
						АКЦИОНЕРНОЕ ОБЩЕСТВО ИНСТИТУТ ТЕПЛОЭЛЕКТРОПРОЕКТ г. МОСКВА

Согласовано: ОАСУ Савенкова

Взам. инв. № | Подпись и дата | Инв. № подл.

Формат А1