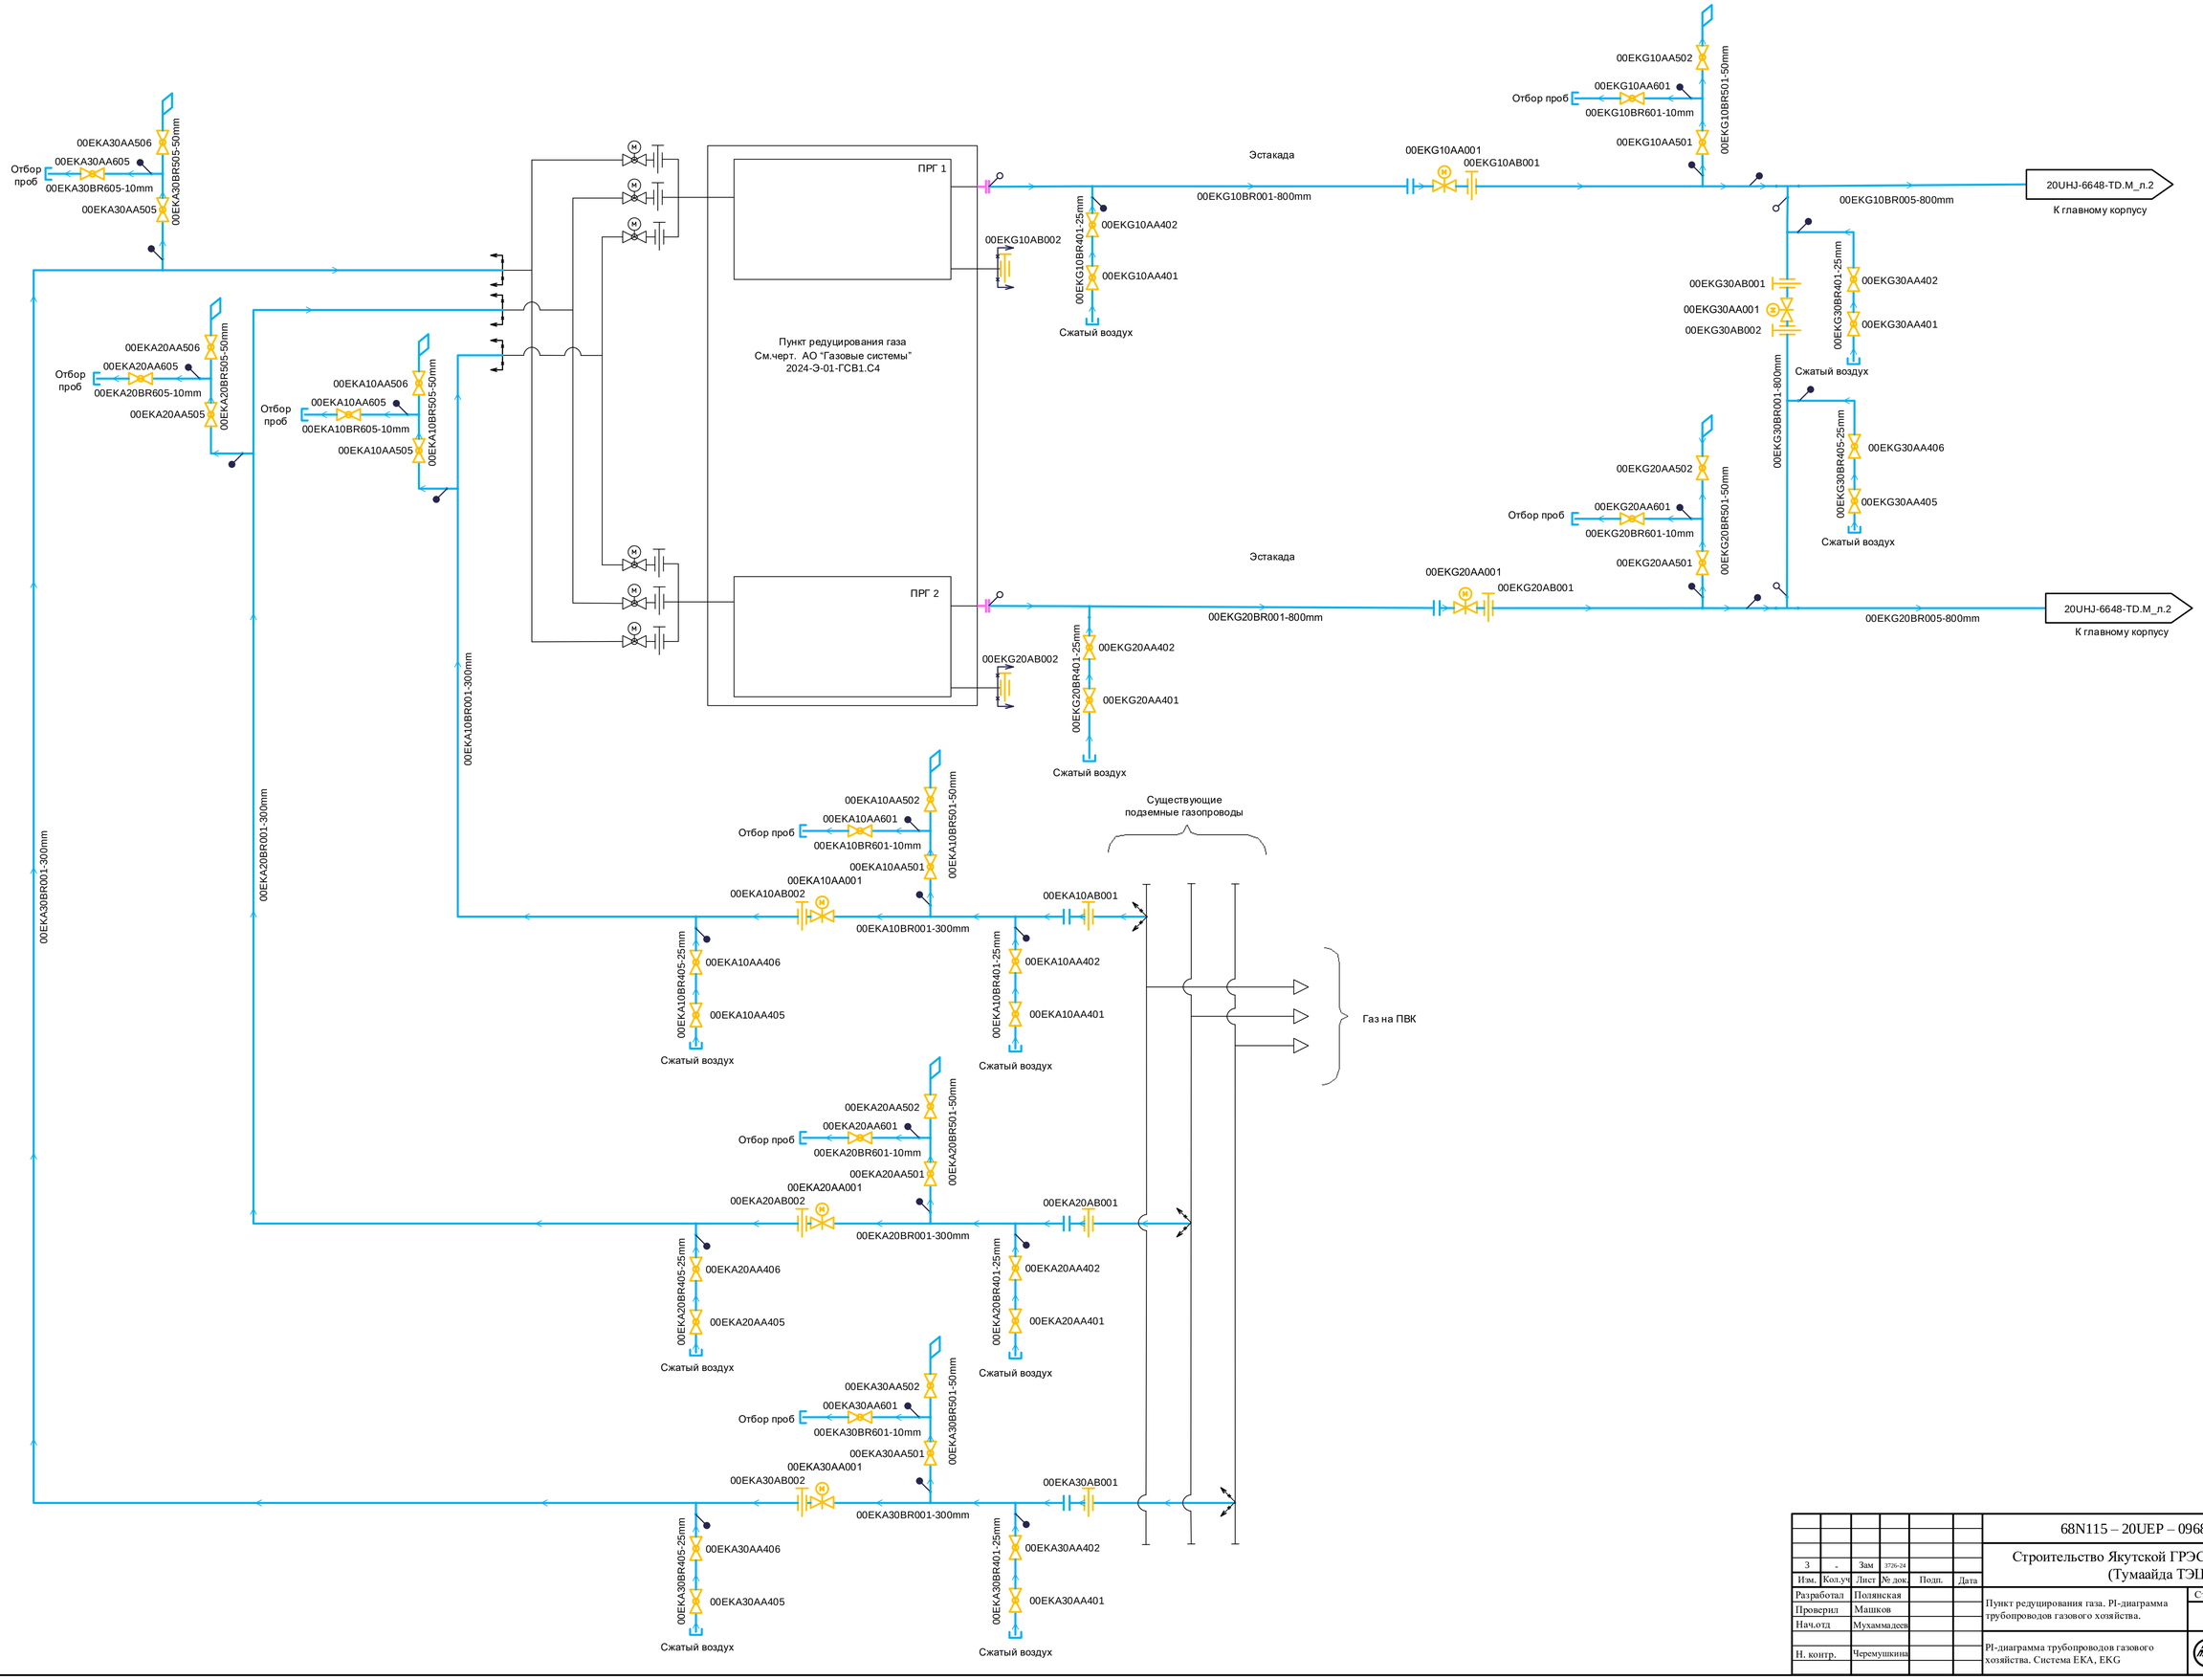

3	-	Зам	3726-24			68N115 – 20UEP – 0968 – TD.M
Изм.	Кол.уч	Лист	№ док.	Подп.	Дата	Строительство Якутской ГРЭС-2 (2-я очередь) (Тумаайда ТЭЦ)
Разработал		Полянская				Пункт редуцирования газа. PI-диаграмма трубопроводов газового хозяйства.
Проверил		Машков				Стадия: Р; Лист: 2; Листов:
Нач.отд		Мухаммадеев				
Н. контр.		Черемушкина				PI-диаграмма трубопроводов газового хозяйства. Система EKA, EKG
						АКЦИОНЕРНОЕ ОБЩЕСТВО ИНСТИТУТ ТЕПЛОЭЛЕКТРОПРОЕКТ г. МОСКВА

Согласовано
ОАСУ Савенкова

Взам. инв. №
Подпись и дата
Инв. № подл.

Формат А1