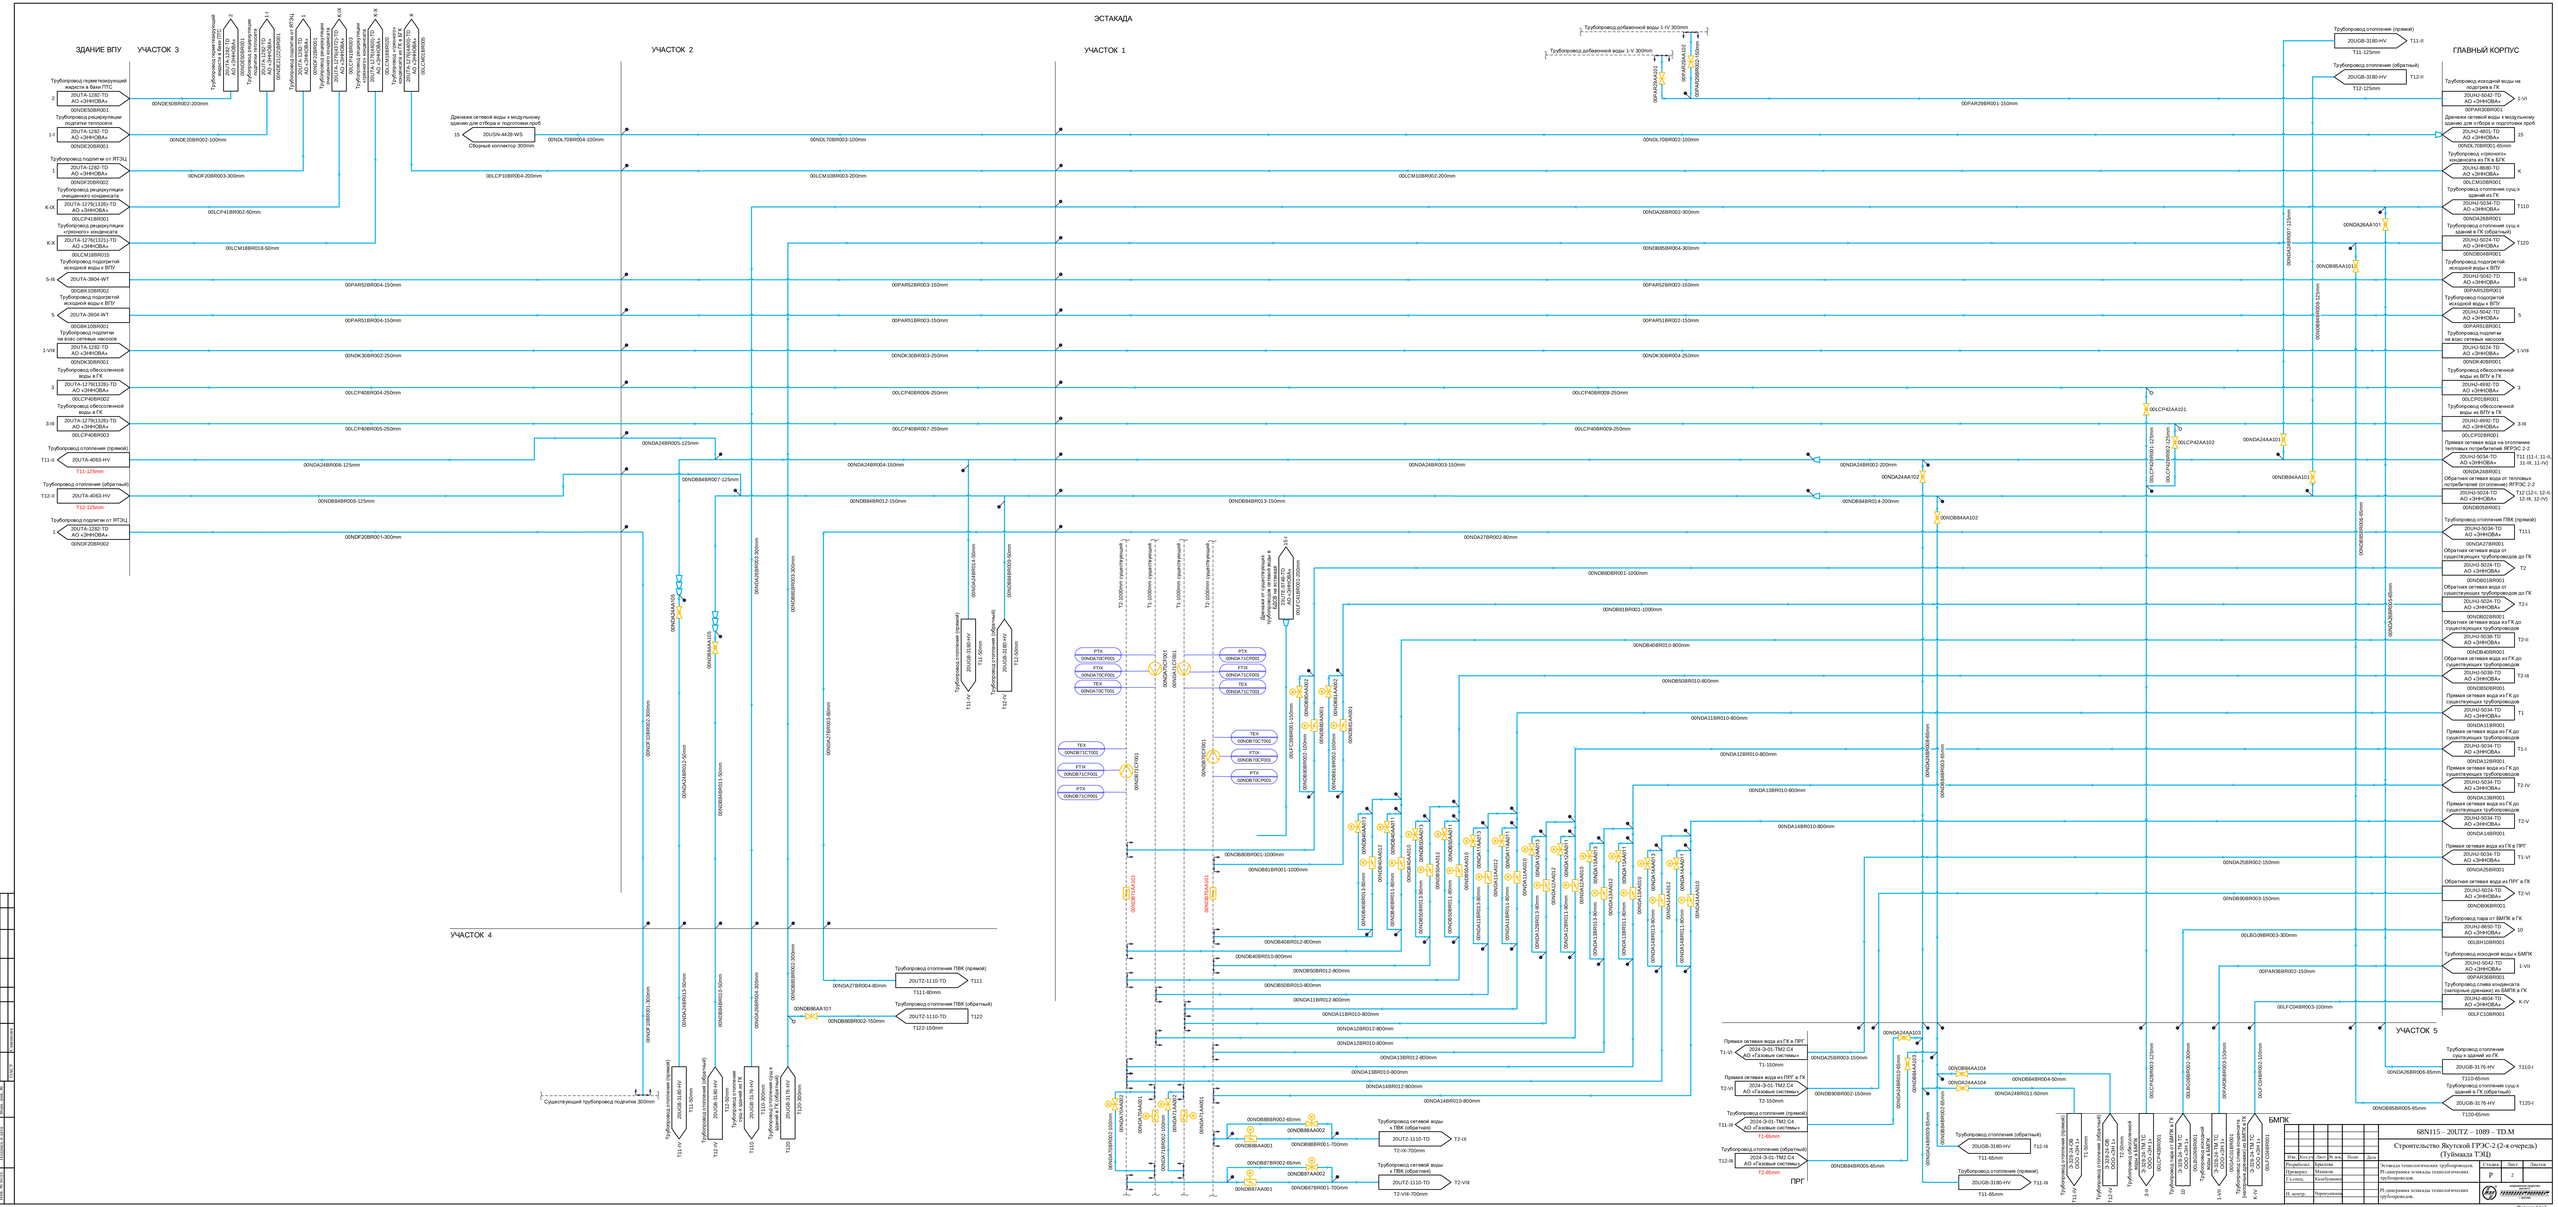
ЭСТАКАДА
ЗДАНИЕ ВПУ
УЧАСТОК 3
УЧАСТОК 2
УЧАСТОК 1
ГЛАВНЫЙ КОРПУС
УЧАСТОК 4
УЧАСТОК 5
БМПК
ПРГ
Трубопровод добавочной воды 1-IV 300мм
Трубопровод отопления (прямой)
Трубопровод отопления (обратный)
Трубопровод исходной воды на подогрев в ГК
Дренажи сетевой воды к модульному зданию для отбора и подготовки проб
Трубопровод «грязного» конденсата из ГК в БГК
Трубопровод отопления сушк к зданий из ГК
Трубопровод отопления сушк к зданий в ГК (обратный)
Трубопровод подпиткой исходной воды в ВПУ
Трубопровод подпитки исходной воды в ВПУ
Трубопровод подпитки на взвс сетевых насосов
Трубопровод обессоленной воды из ВПУ в ГК
Трубопровод обессоленной воды в ВПУ в ГК
Прямая сетевая вода на отопление тепловых потребителей ЛЕРТОС 2-2
Обратная сетевая вода от тепловых потребителей (отопление) ЛЕРТОС 2-2
Трубопровод отопления ПВК (прямой)
Обратная сетевая вода от существующих трубопроводов до ГК
Обратная сетевая вода от существующих трубопроводов до ГК
Обратная сетевая вода из ГК до существующих трубопроводов
Обратная сетевая вода из ГК до существующих трубопроводов
Прямая сетевая вода из ГК до существующих трубопроводов
Прямая сетевая вода из ГК до существующих трубопроводов
Прямая сетевая вода из ГК до существующих трубопроводов
Прямая сетевая вода из ГК до существующих трубопроводов
Прямая сетевая вода из ГК в ПРГ
Обратная сетевая вода из ПРГ в ГК
Трубопровод пара от БМПК в ГК
Трубопровод исходной воды в БМПК
Трубопровод слива конденсата (напорные дренажи) из БМПК в ГК
Трубопровод отопления сушк зданий из ГК
Трубопровод отопления сушк зданий из ГК (обратный)
Существующие трубопроводы подпитки 300мм
68N115 – 20UTZ – 1089 – ТВ.М
Строительство Якутской ТЭЦ-2 (2-я очередь)
(Тувинская ТЭЦ)
Стадия
Лист
Листов
Р
2
Организация