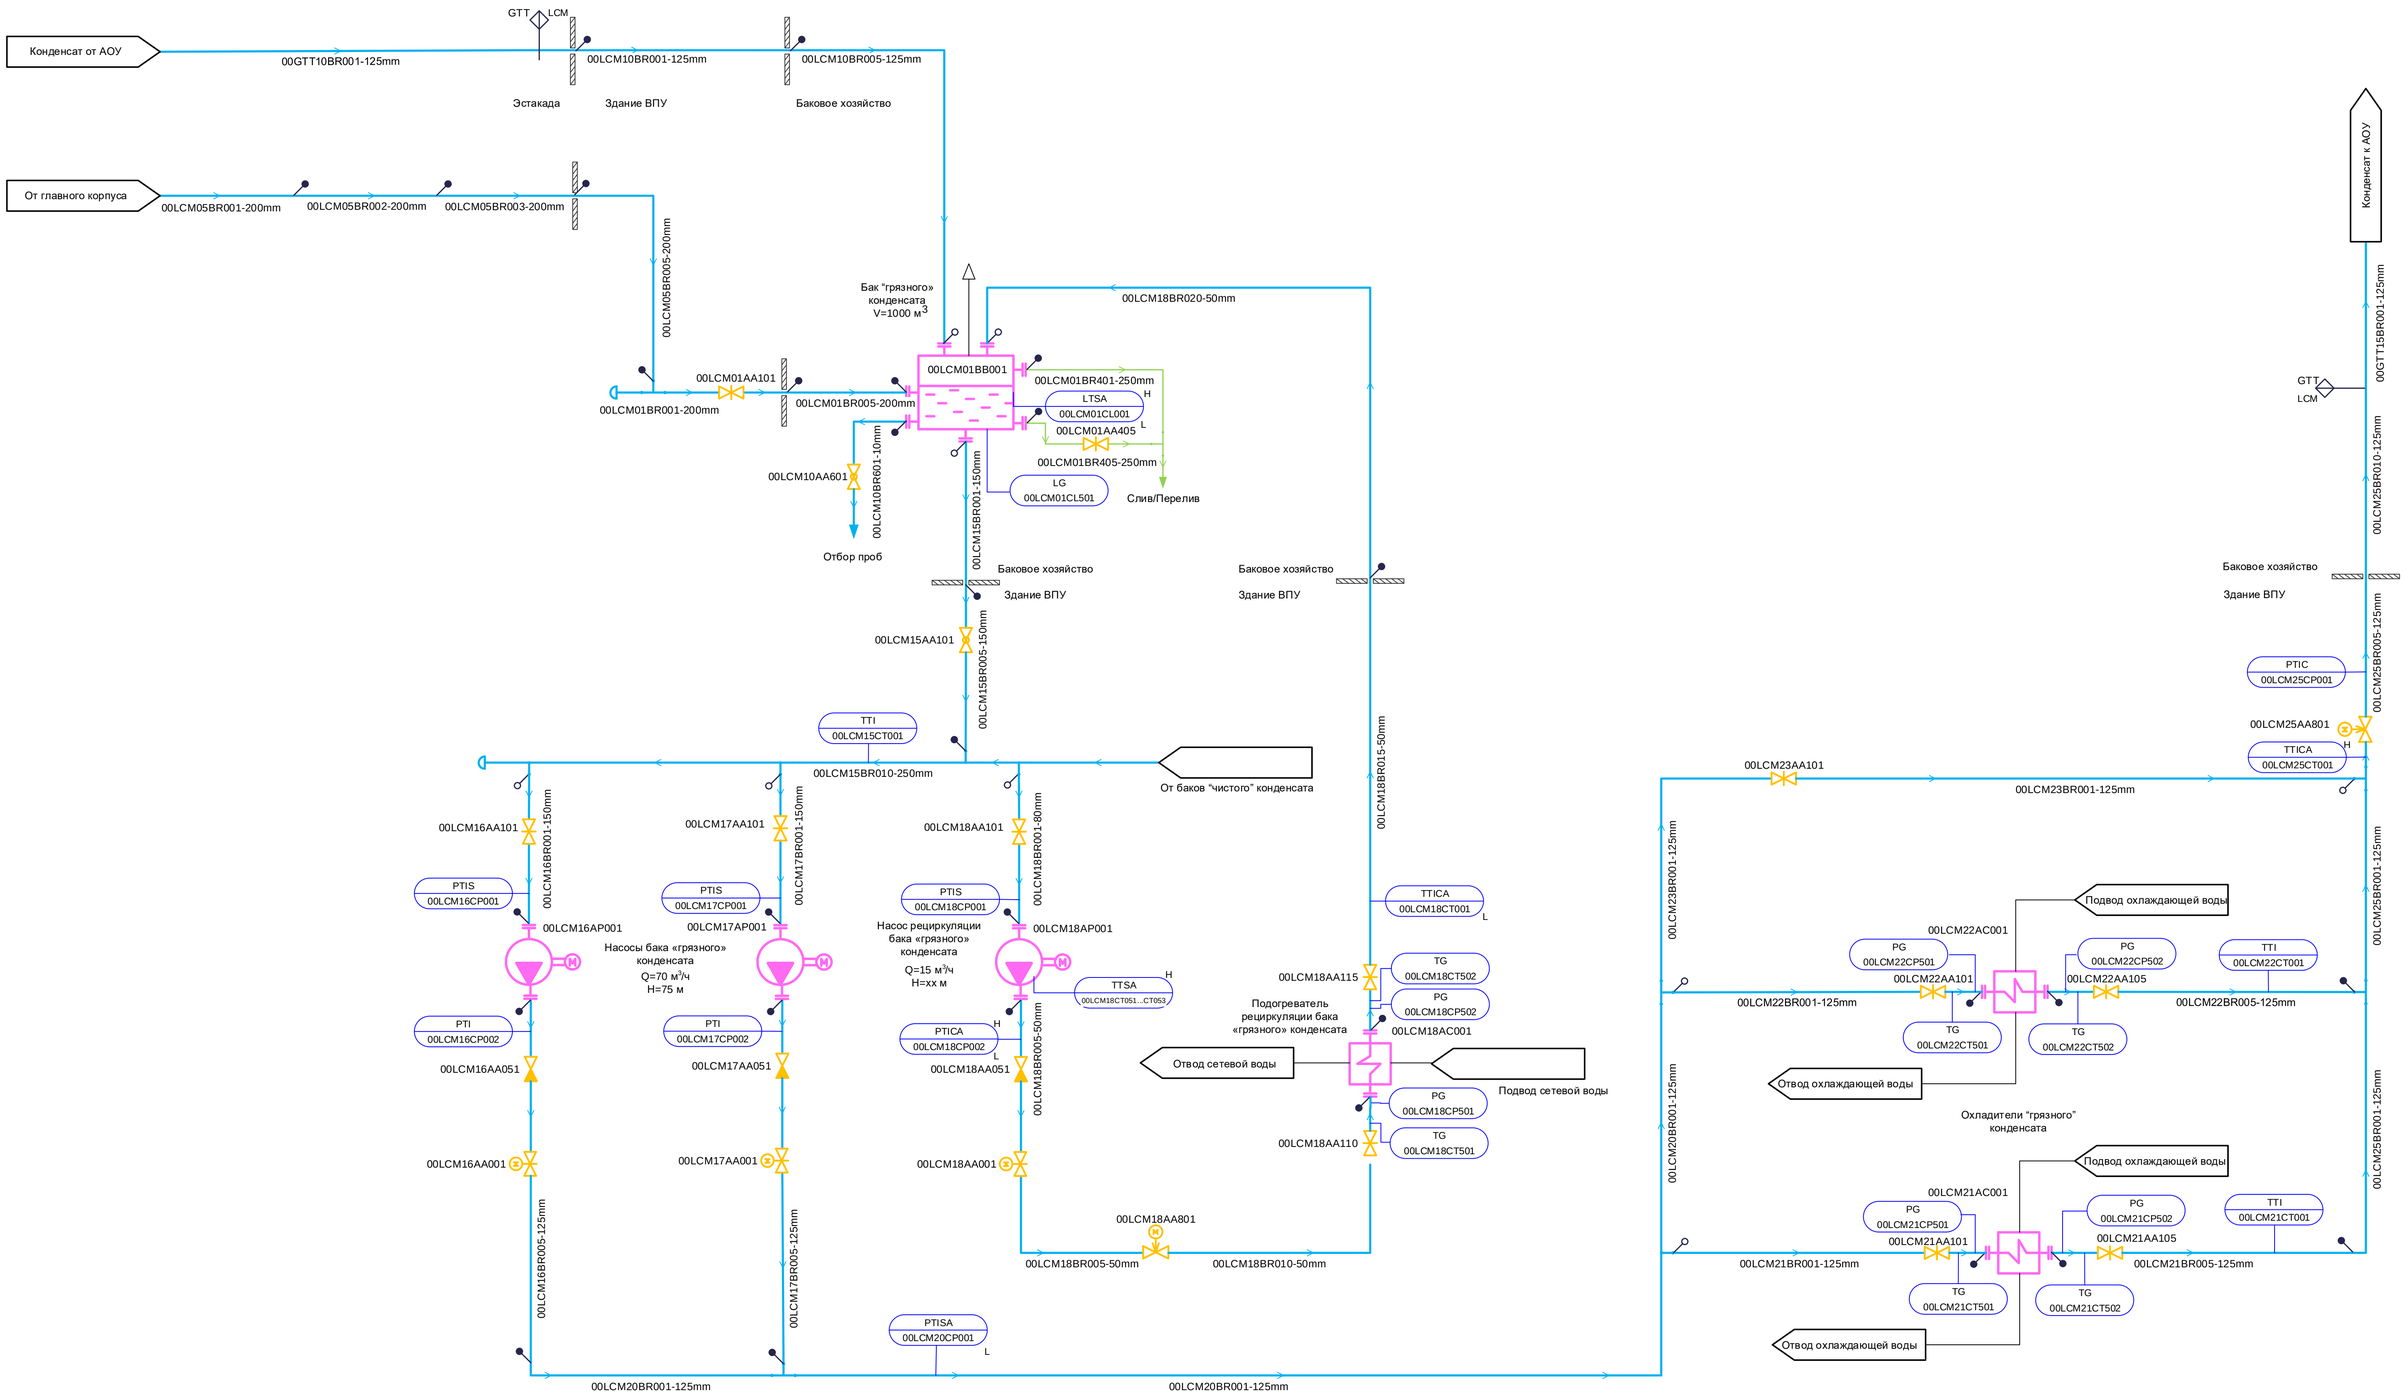

Примечания:

1. Возможна корректировка PI-Диаграммы после полдучения ИД от поставщиков оборудования.
2. Дренажи и воздушники будут добавлены после выполнения рабочей документации.
3. Возможна корректировка PI-диаграммы в части КИПиА после получения ИД от поставщиков насосных агрегатов.
4. PI-диаграмма разработана в качестве задания АО «ЭНОВА» для выпуска рабочей документации.

Изм.	Кол.уч	Лист	№ док.	Подп.	Дата	68N115 – 21UTE – 1276 – TD.M			
						Строительство Якутской ГРЭС-2 (2-я очередь) (Тумаайда ТЭЦ)			
Разработал		Полянская				Бак грязного конденсата (1000 м3) PI-диаграмма трубопроводов "грязного" конденсата	Стадия	Лист	Листов
Проверил		Калабушкина					Р	2	
Н. контр.		Черемушкина				PI-диаграмма трубопроводов "грязного" конденсата. Система LCM	АКЦИОНЕРНОЕ ОБЩЕСТВО ИНСТИТУТ ТЕПЛОЭЛЕКТРОПРОЕКТ г. МОСКВА		

Формат А1

Согласовано

ОЛСУ Савенкова

Взам. инв. №

Подпись и дата

Инв. № подл.