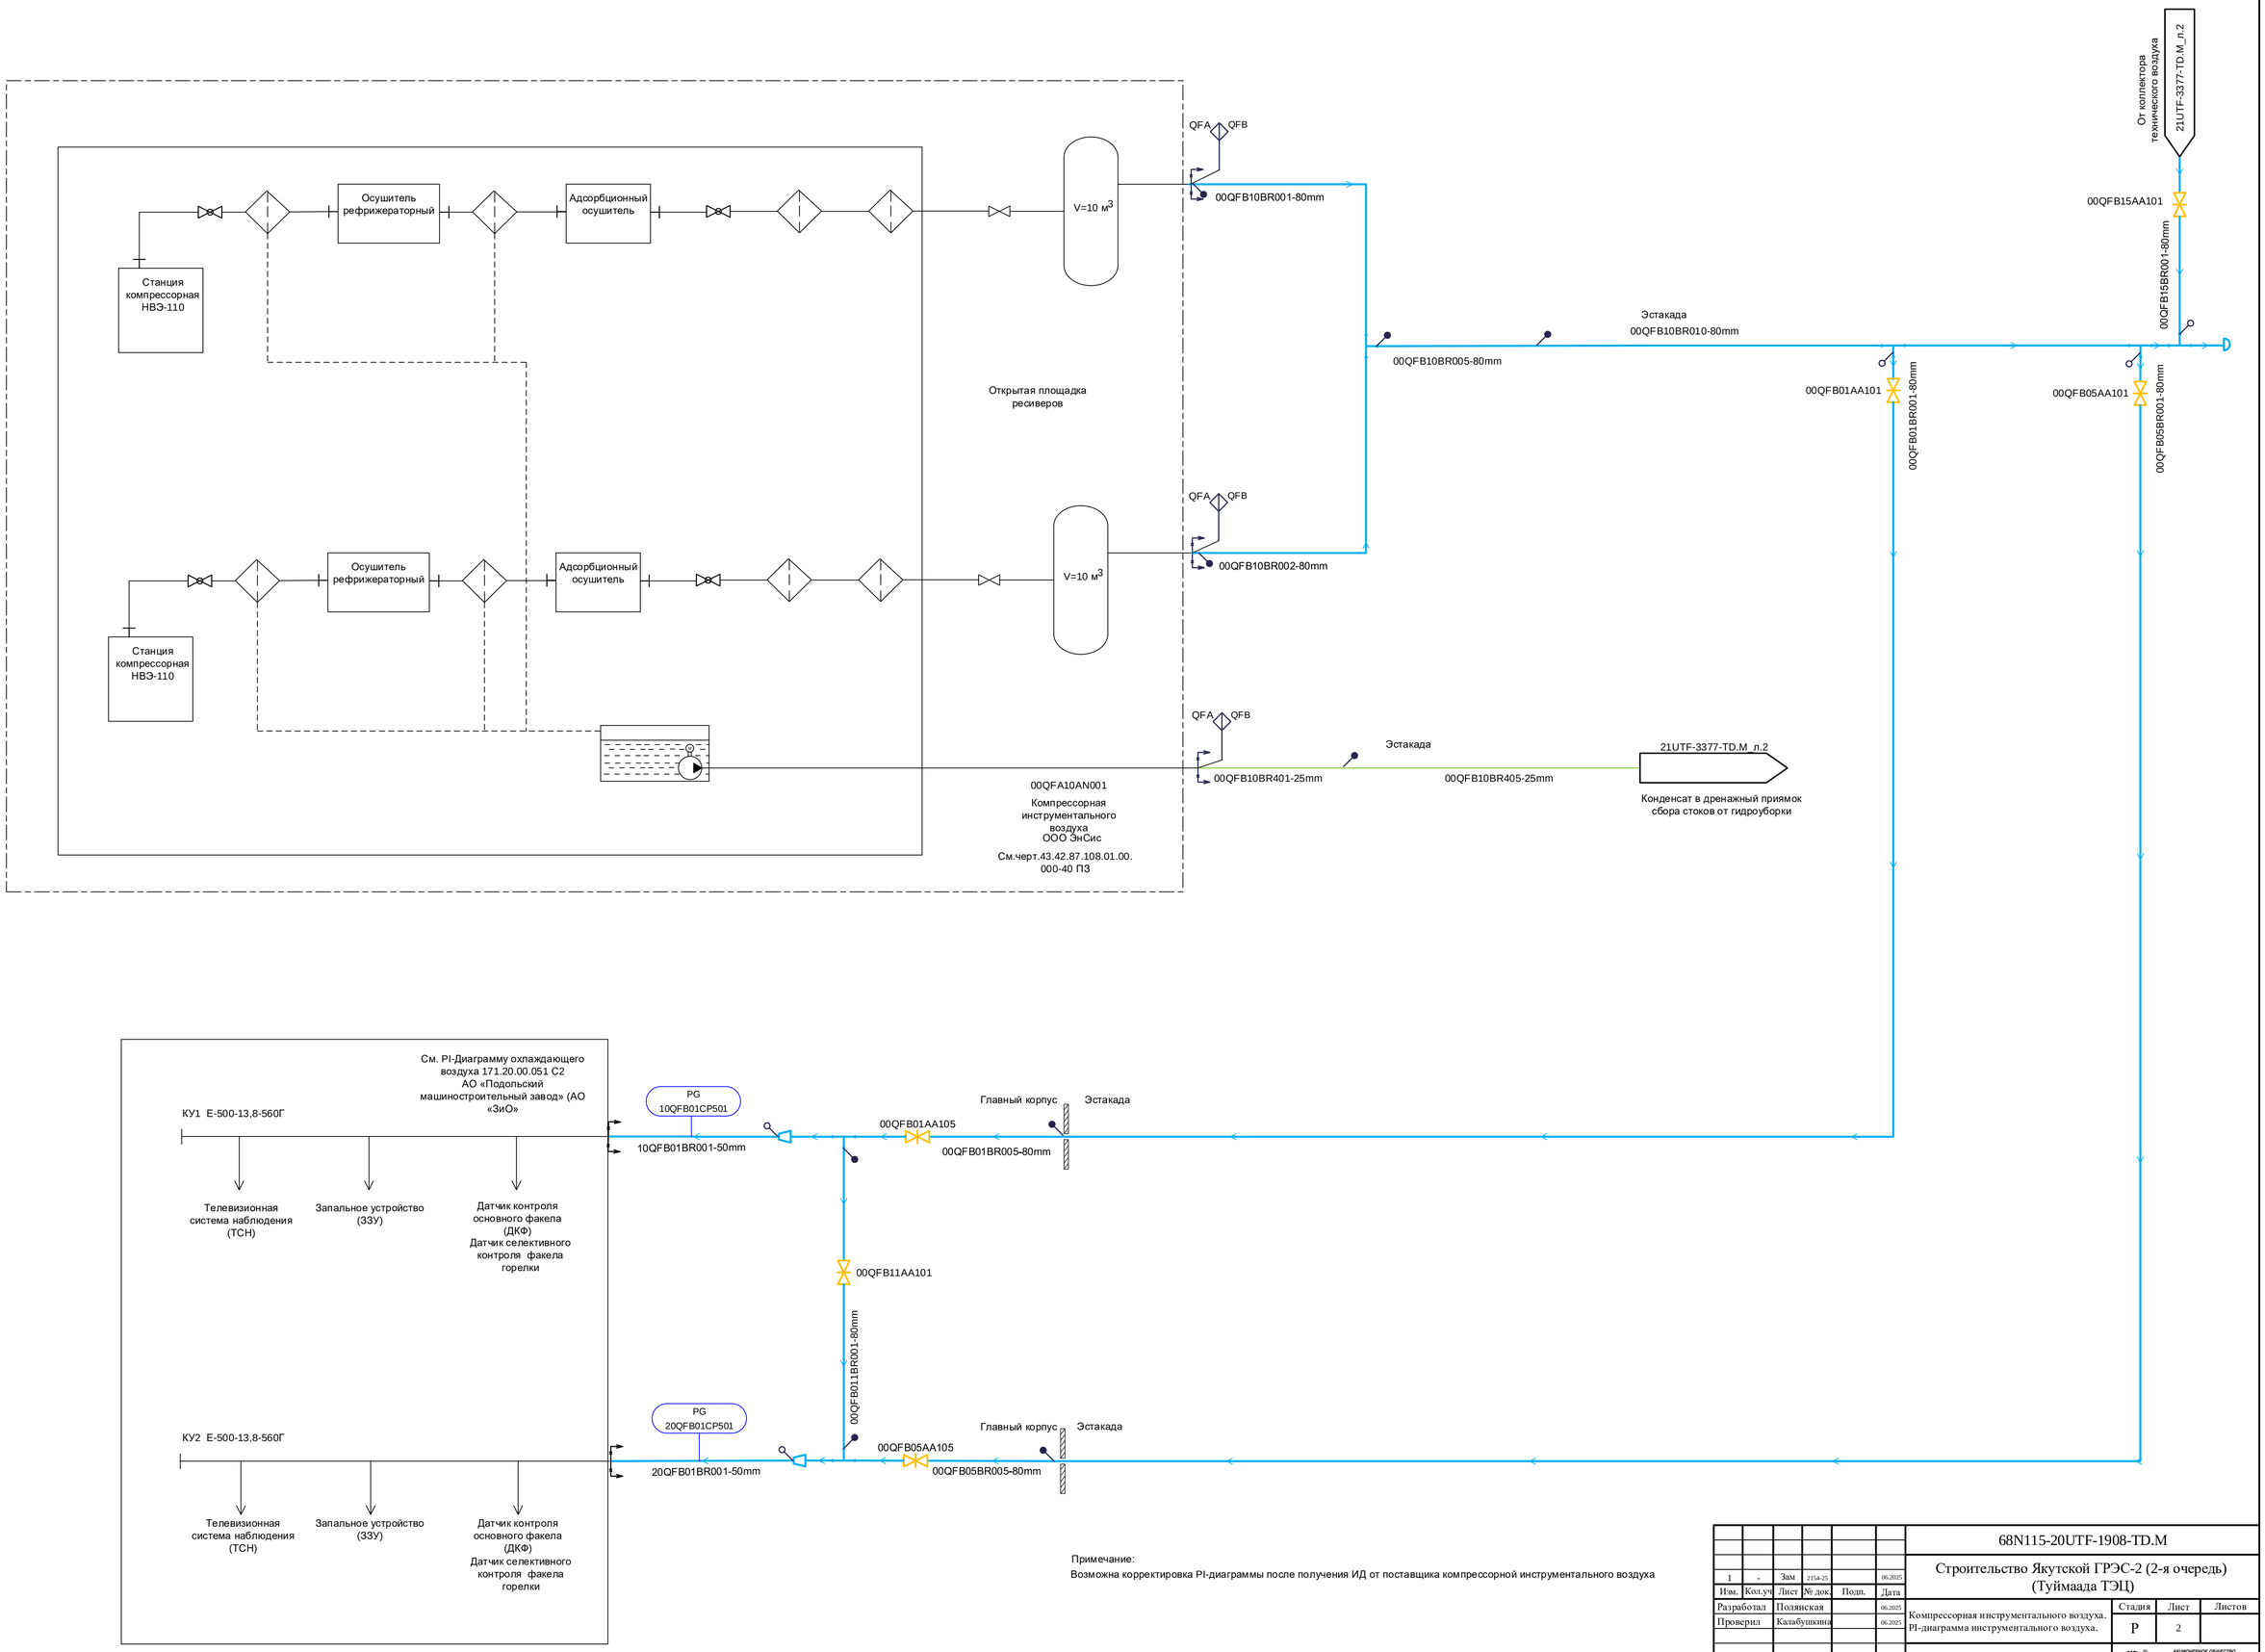

Примечание:
Возможна корректировка PI-диаграммы после получения ИД от поставщика компрессорной инструментального воздуха

1	-	Зам	2154-25		06.2025	68N115-20UTF-1908-TD.M
Изм.	Кол.уч	Лист	№ док.	Подп.	Дата	Строительство Якутской ГРЭС-2 (2-я очередь) (Туймаада ТЭЦ)
Разработал		Полянская			06.2025	Компрессорная инструментального воздуха. PI-диаграмма инструментального воздуха.
Проверил		Калабушкина			06.2025	Стадия: Р; Лист: 2; Листов:
Н. контр.		Черемушкина				PI-диаграмма инструментального воздуха. Система QFB

АКЦИОНЕРНОЕ ОБЩЕСТВО ИНСТИТУТ ТЕПЛОЭЛЕКТРОПРОЕКТ г. МОСКВА

Согласовано
ОАСУ Савенкова
Взам. инв. №
Подпись и дата
Инв. № подл.

Формат А1