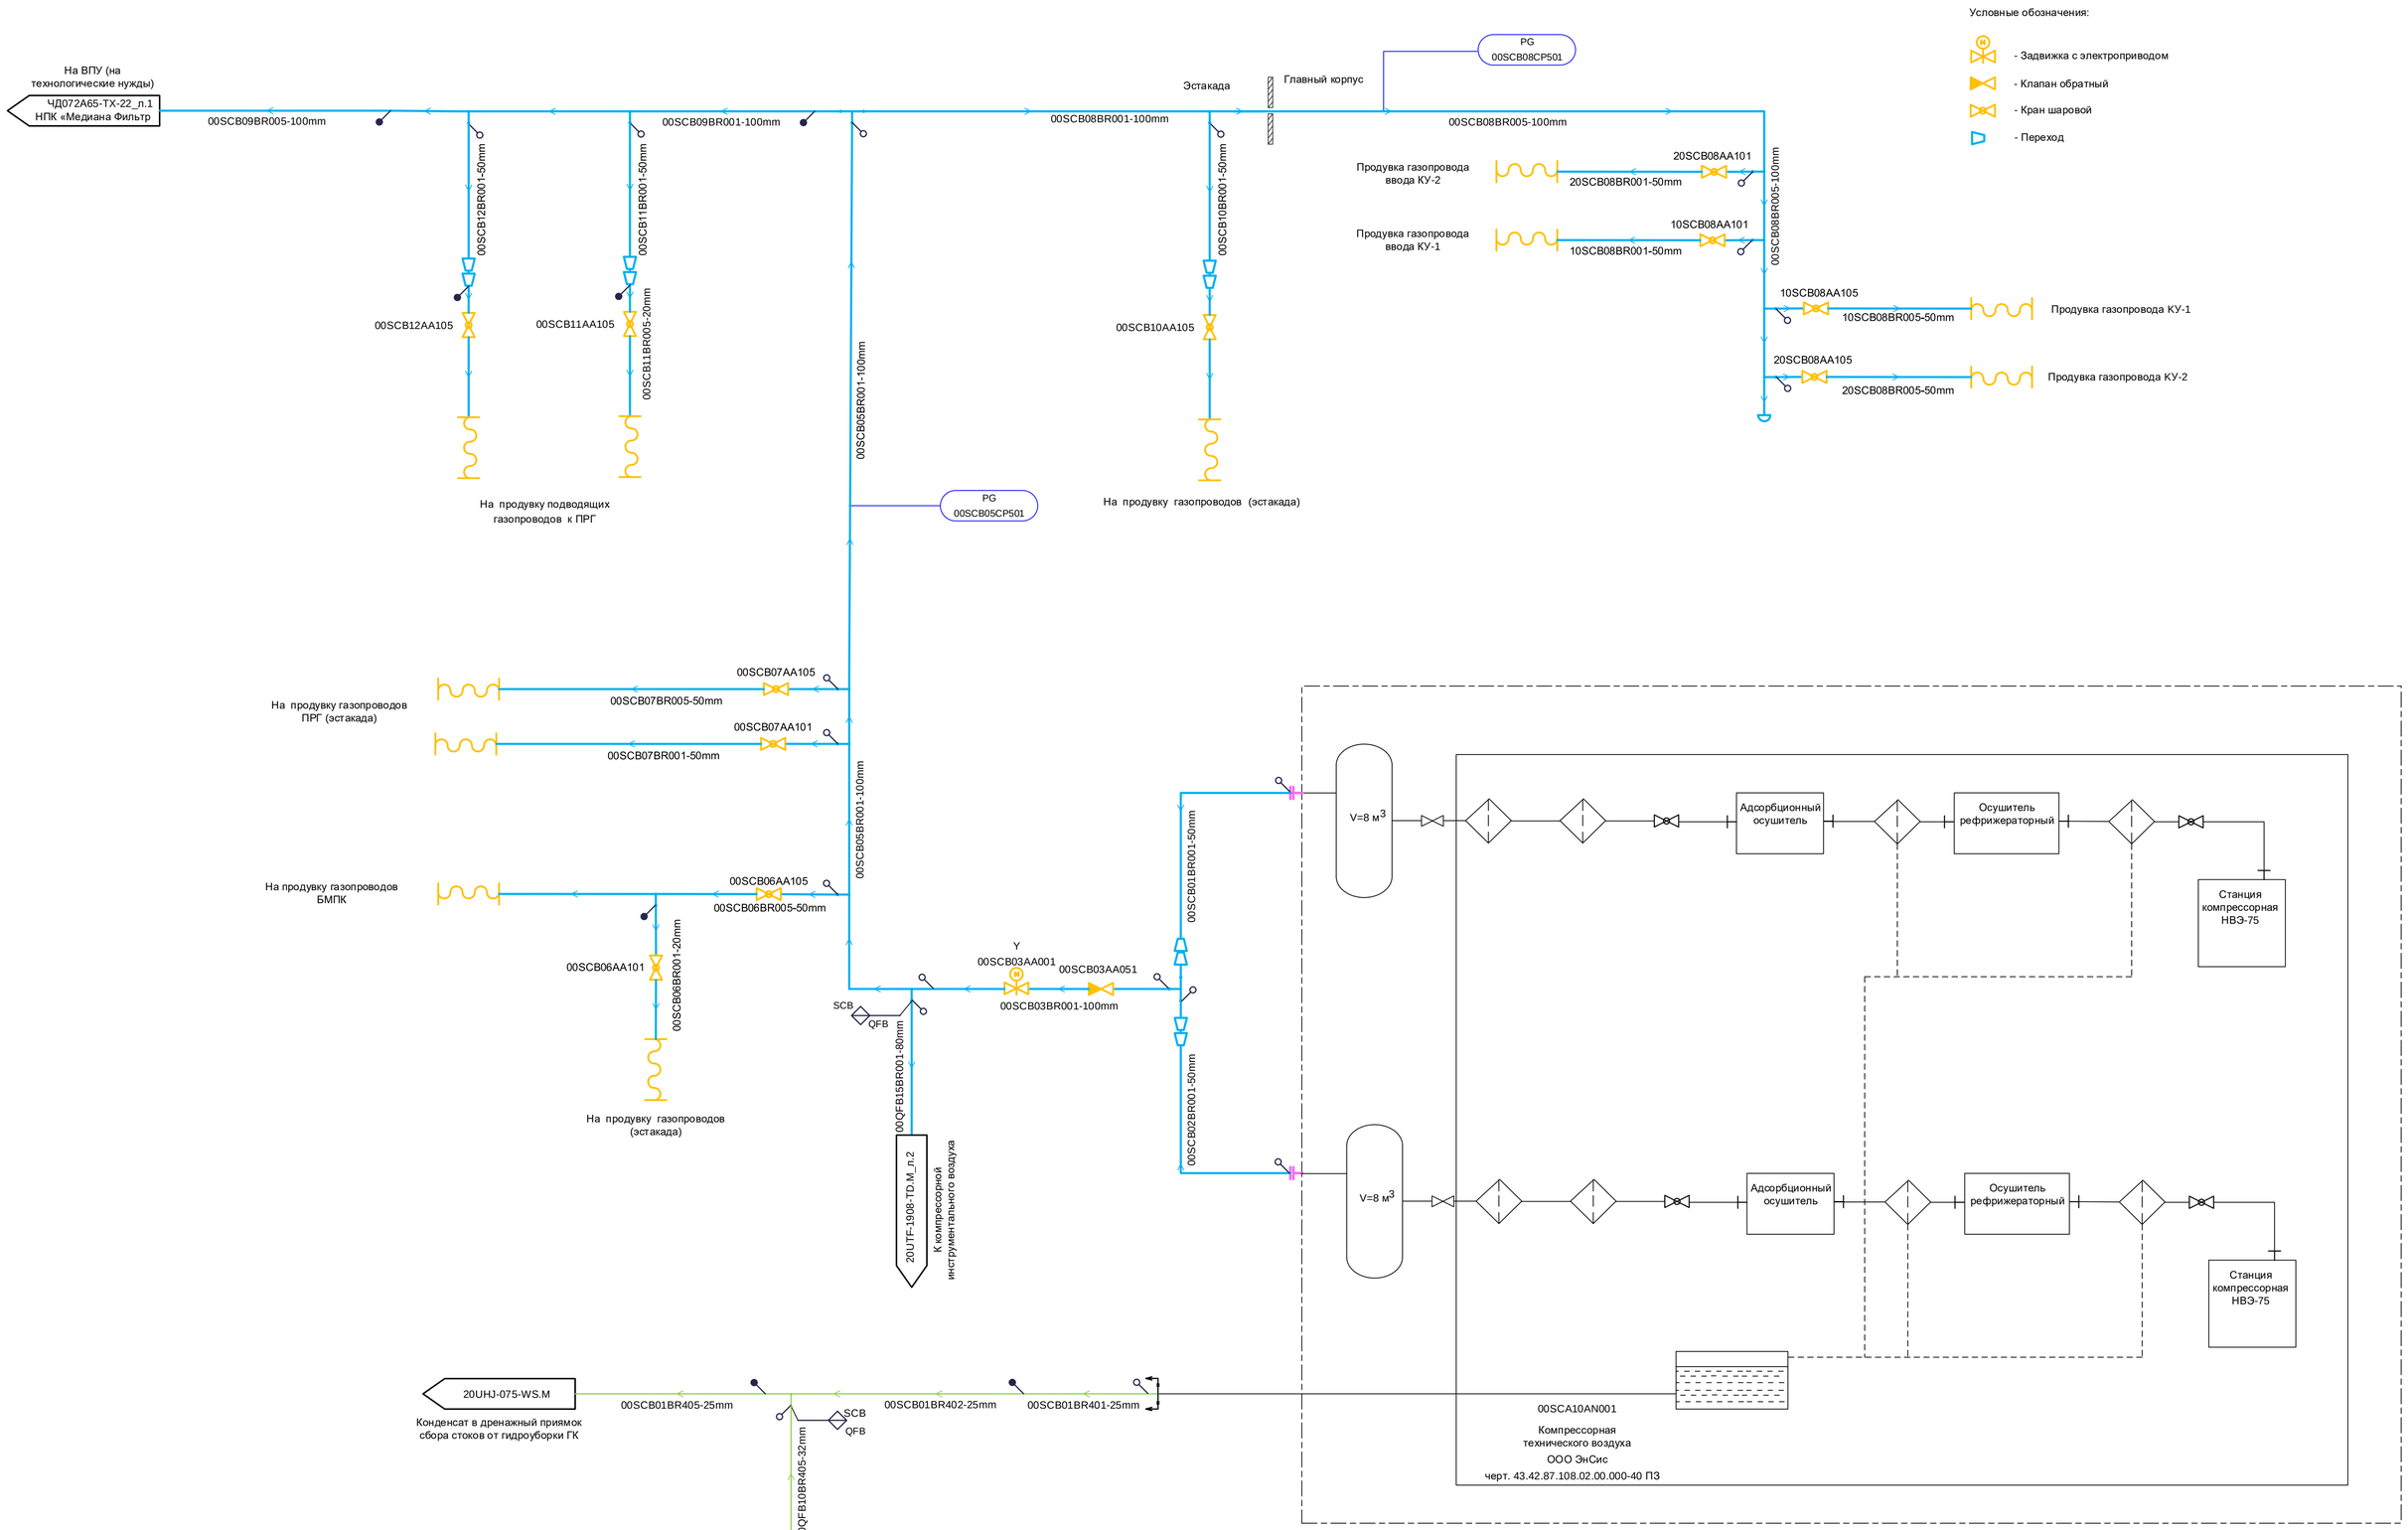

1	-	Зам	2376-25		11.2025	68N115 – 21UTF – 3377 – TD.M
Изм.	Кол.уч	Лист	№ док.	Подп.	Дата	Строительство Якутской ГРЭС-2 (2-я очередь) (Туймаада ТЭЦ)
Разработал		Полянская				Компрессорная технического воздуха. PI-диаграмма трубопроводов технического сжатого воздуха.
Проверил		Калабушкина				Стадия: Р; Лист: 2; Листов:
Н. контр.		Черемушкина				PI-диаграмма трубопроводов технического сжатого воздуха. Система SCB
						АКЦИОНЕРНОЕ ОБЩЕСТВО ИНСТИТУТ ТЕПЛОЭЛЕКТРОПРОЕКТ г. МОСКВА

Согласовано
ОАСУ Савицкая
Взам. инв. №
Подпись и дата
Инв. № подл.

Формат А1