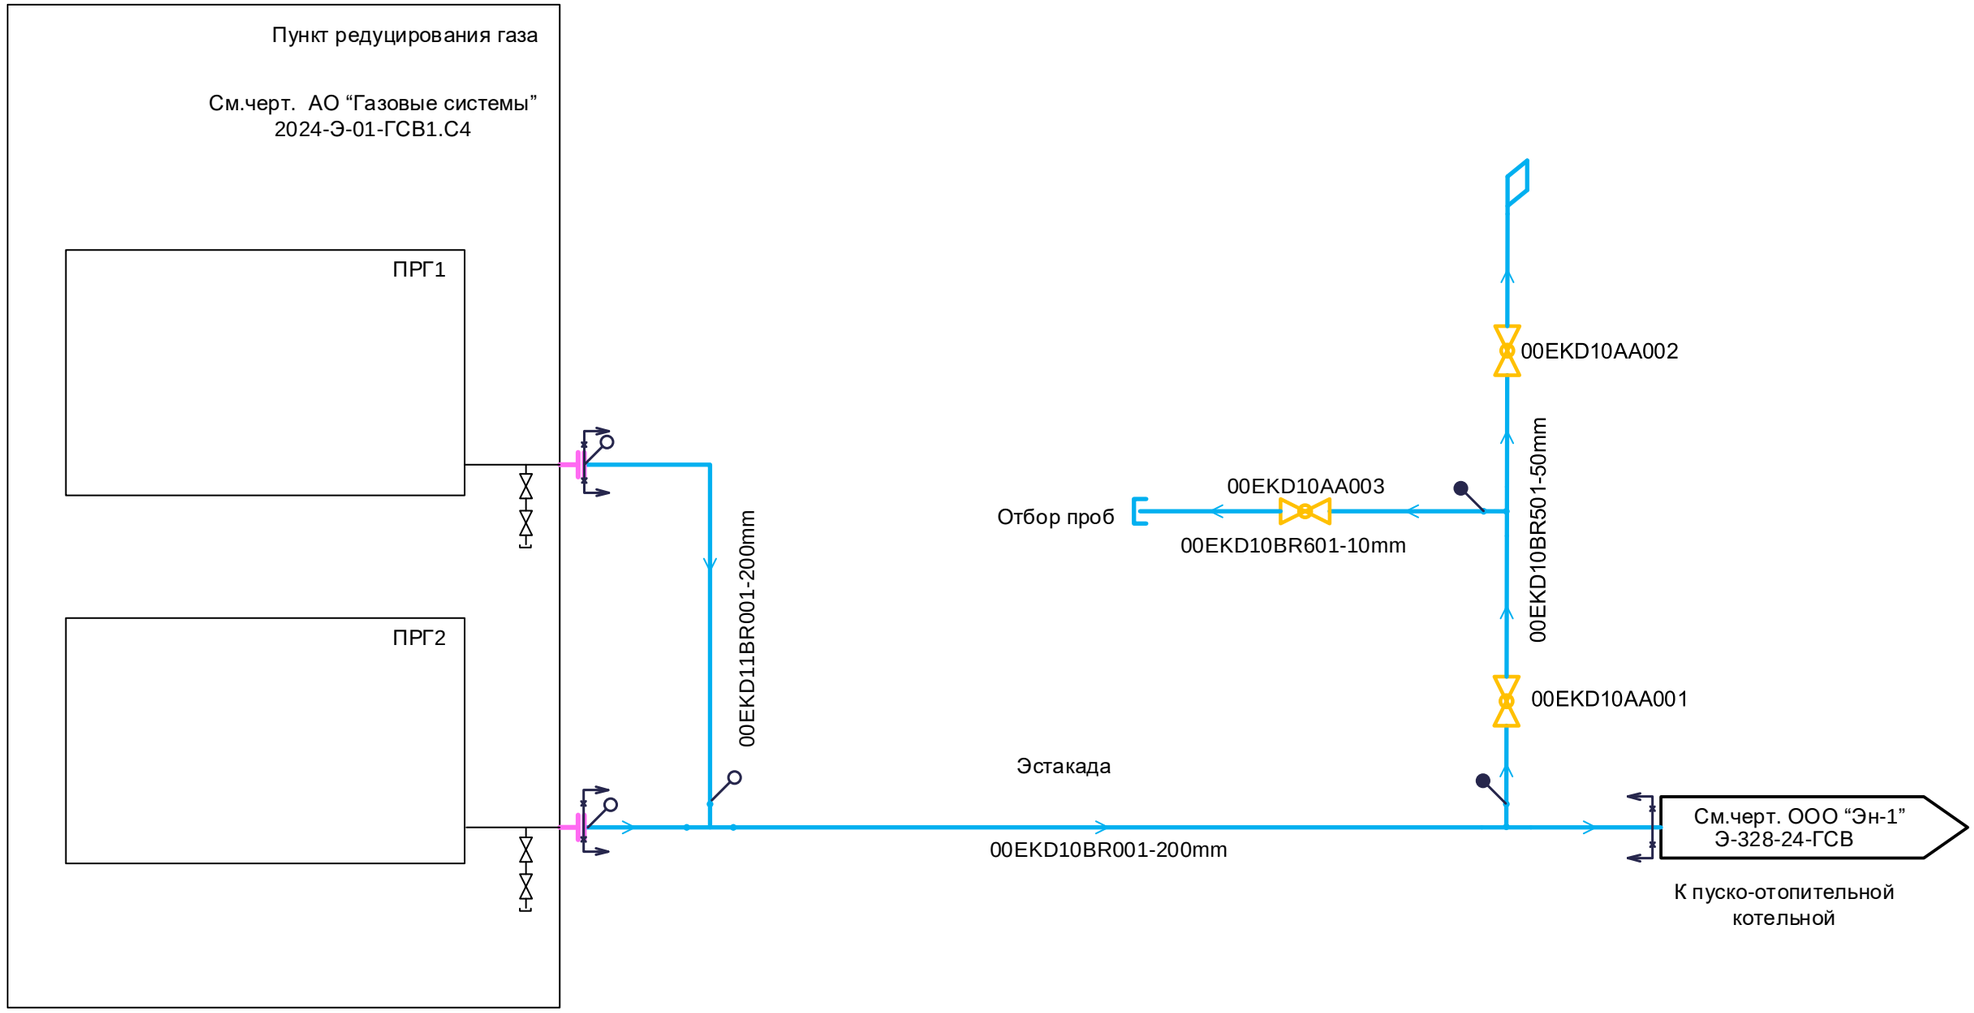


Согласовано

Савенкова

ОАСУ

Взам. инв. №

Подпись и дата

Инв. № подл.

| | | | | | | |
|---|---|---|---|---|---|---|
| 1 | - | Зам | 2092-24 | | | |
| Изм. | Кол.уч | Лист | № док. | Подп. | Дата | |
| Разработал | | Полянская | | | | |
| Проверил | | Машков | | | | |
| Нач.отд | | Мухаммадеев | | | | |
| Н. контр. | | Черемушкина | | | | |

68N115 – 20UTH – 4244 – TD.M

Строительство Якутской ГРЭС-2(2-я очередь)
(Туймаада ТЭЦ)

Пусковая котельная. PI-Диаграмма газопроводов к котлам пуско-отопительной котельной.

| Стадия | Лист | Листов |
|---|---|---|
| Р | 2 | |

PI-диаграмма газопроводов к котлам пуско-отопительной котельной. Система EKD

АКЦИОНЕРНОЕ ОБЩЕСТВО ИНСТИТУТ ТЕПЛОЭЛЕКТРОПРОЕКТ Г. МОСКВА

Формат А3