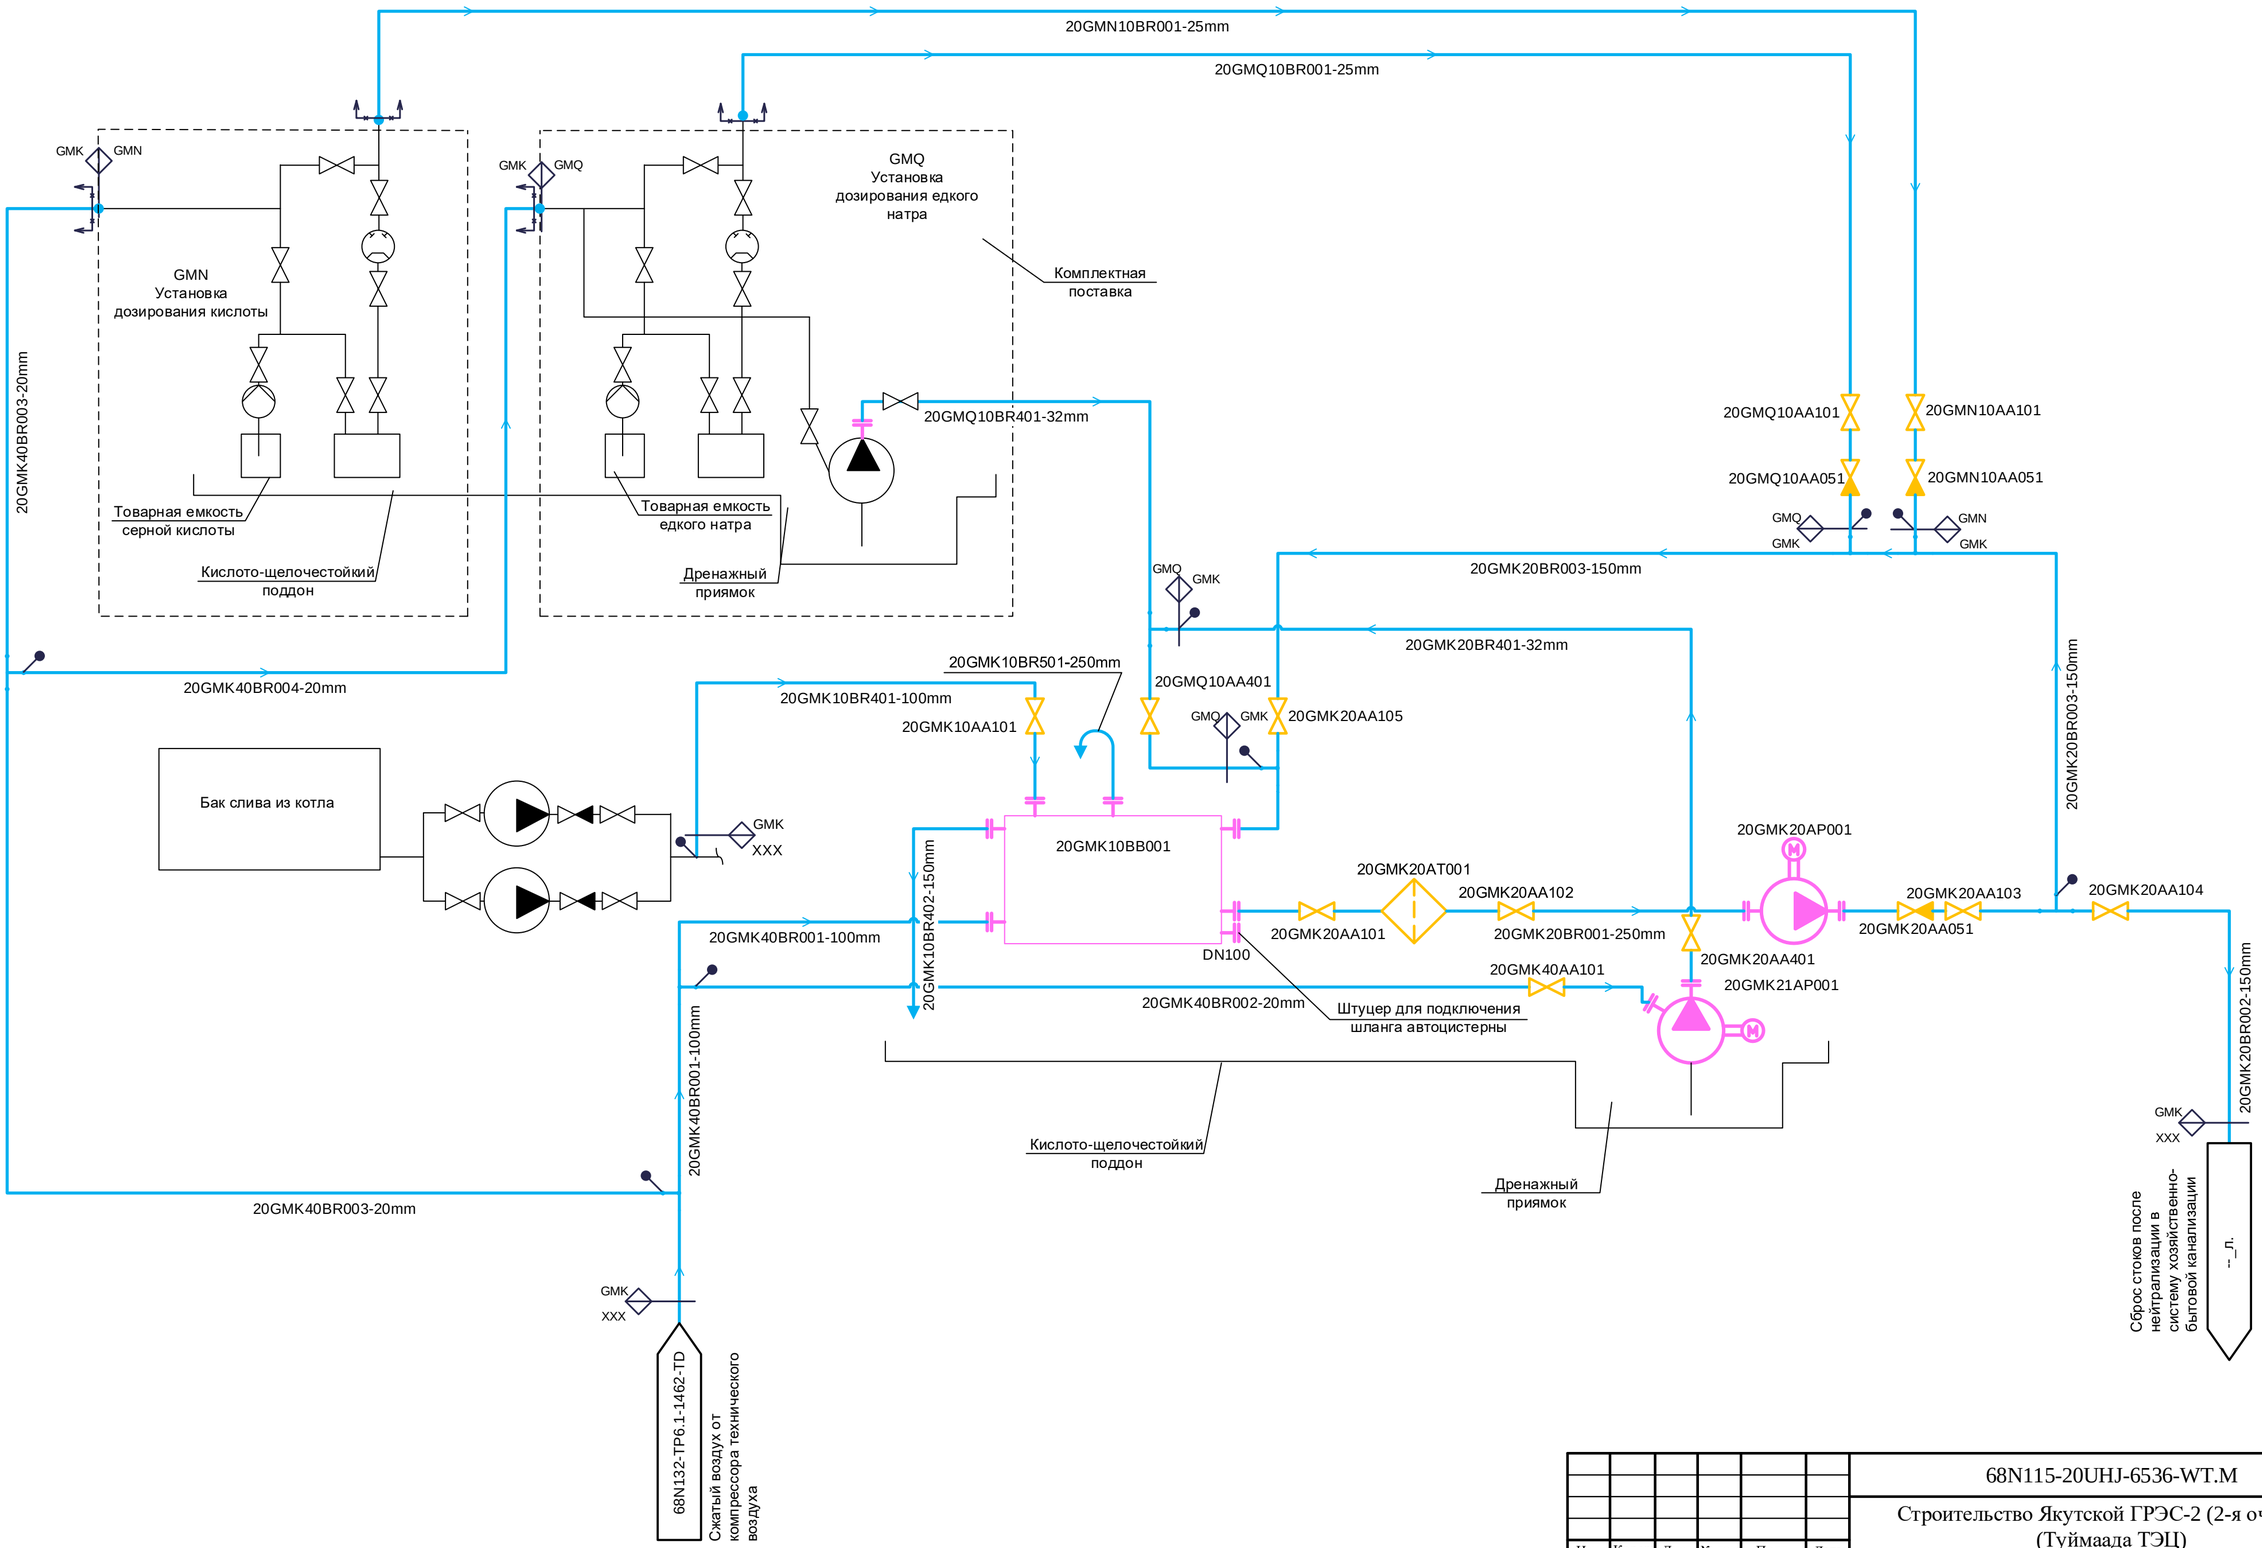

Изм.	Кол.уч	Лист	№ док.	Подп.	Дата	68N115-20UHJ-6536-WT.M
						Строительство Якутской ГРЭС-2 (2-я очередь) (Туймаада ТЭЦ)
Разработал		Растопчина				Главный корпус. PI-диаграмма установки нейтрализации химпромывок оборудования.
Проверил		Рудь				
Н. контр.		Астраханцев				PI-диаграмма установки нейтрализации химпромывок оборудования. Система GMK, GMN, GMQ

Стадия	Лист	Листов
Р	2	

АКЦИОНЕРНОЕ ОБЩЕСТВО ИНСТИТУТ ТЕПЛОЭЛЕКТРОПРОЕКТ Г. МОСКВА

Согласовано

Взам. инв. №

Подпись и дата

Инв. № подл.

Формат А2