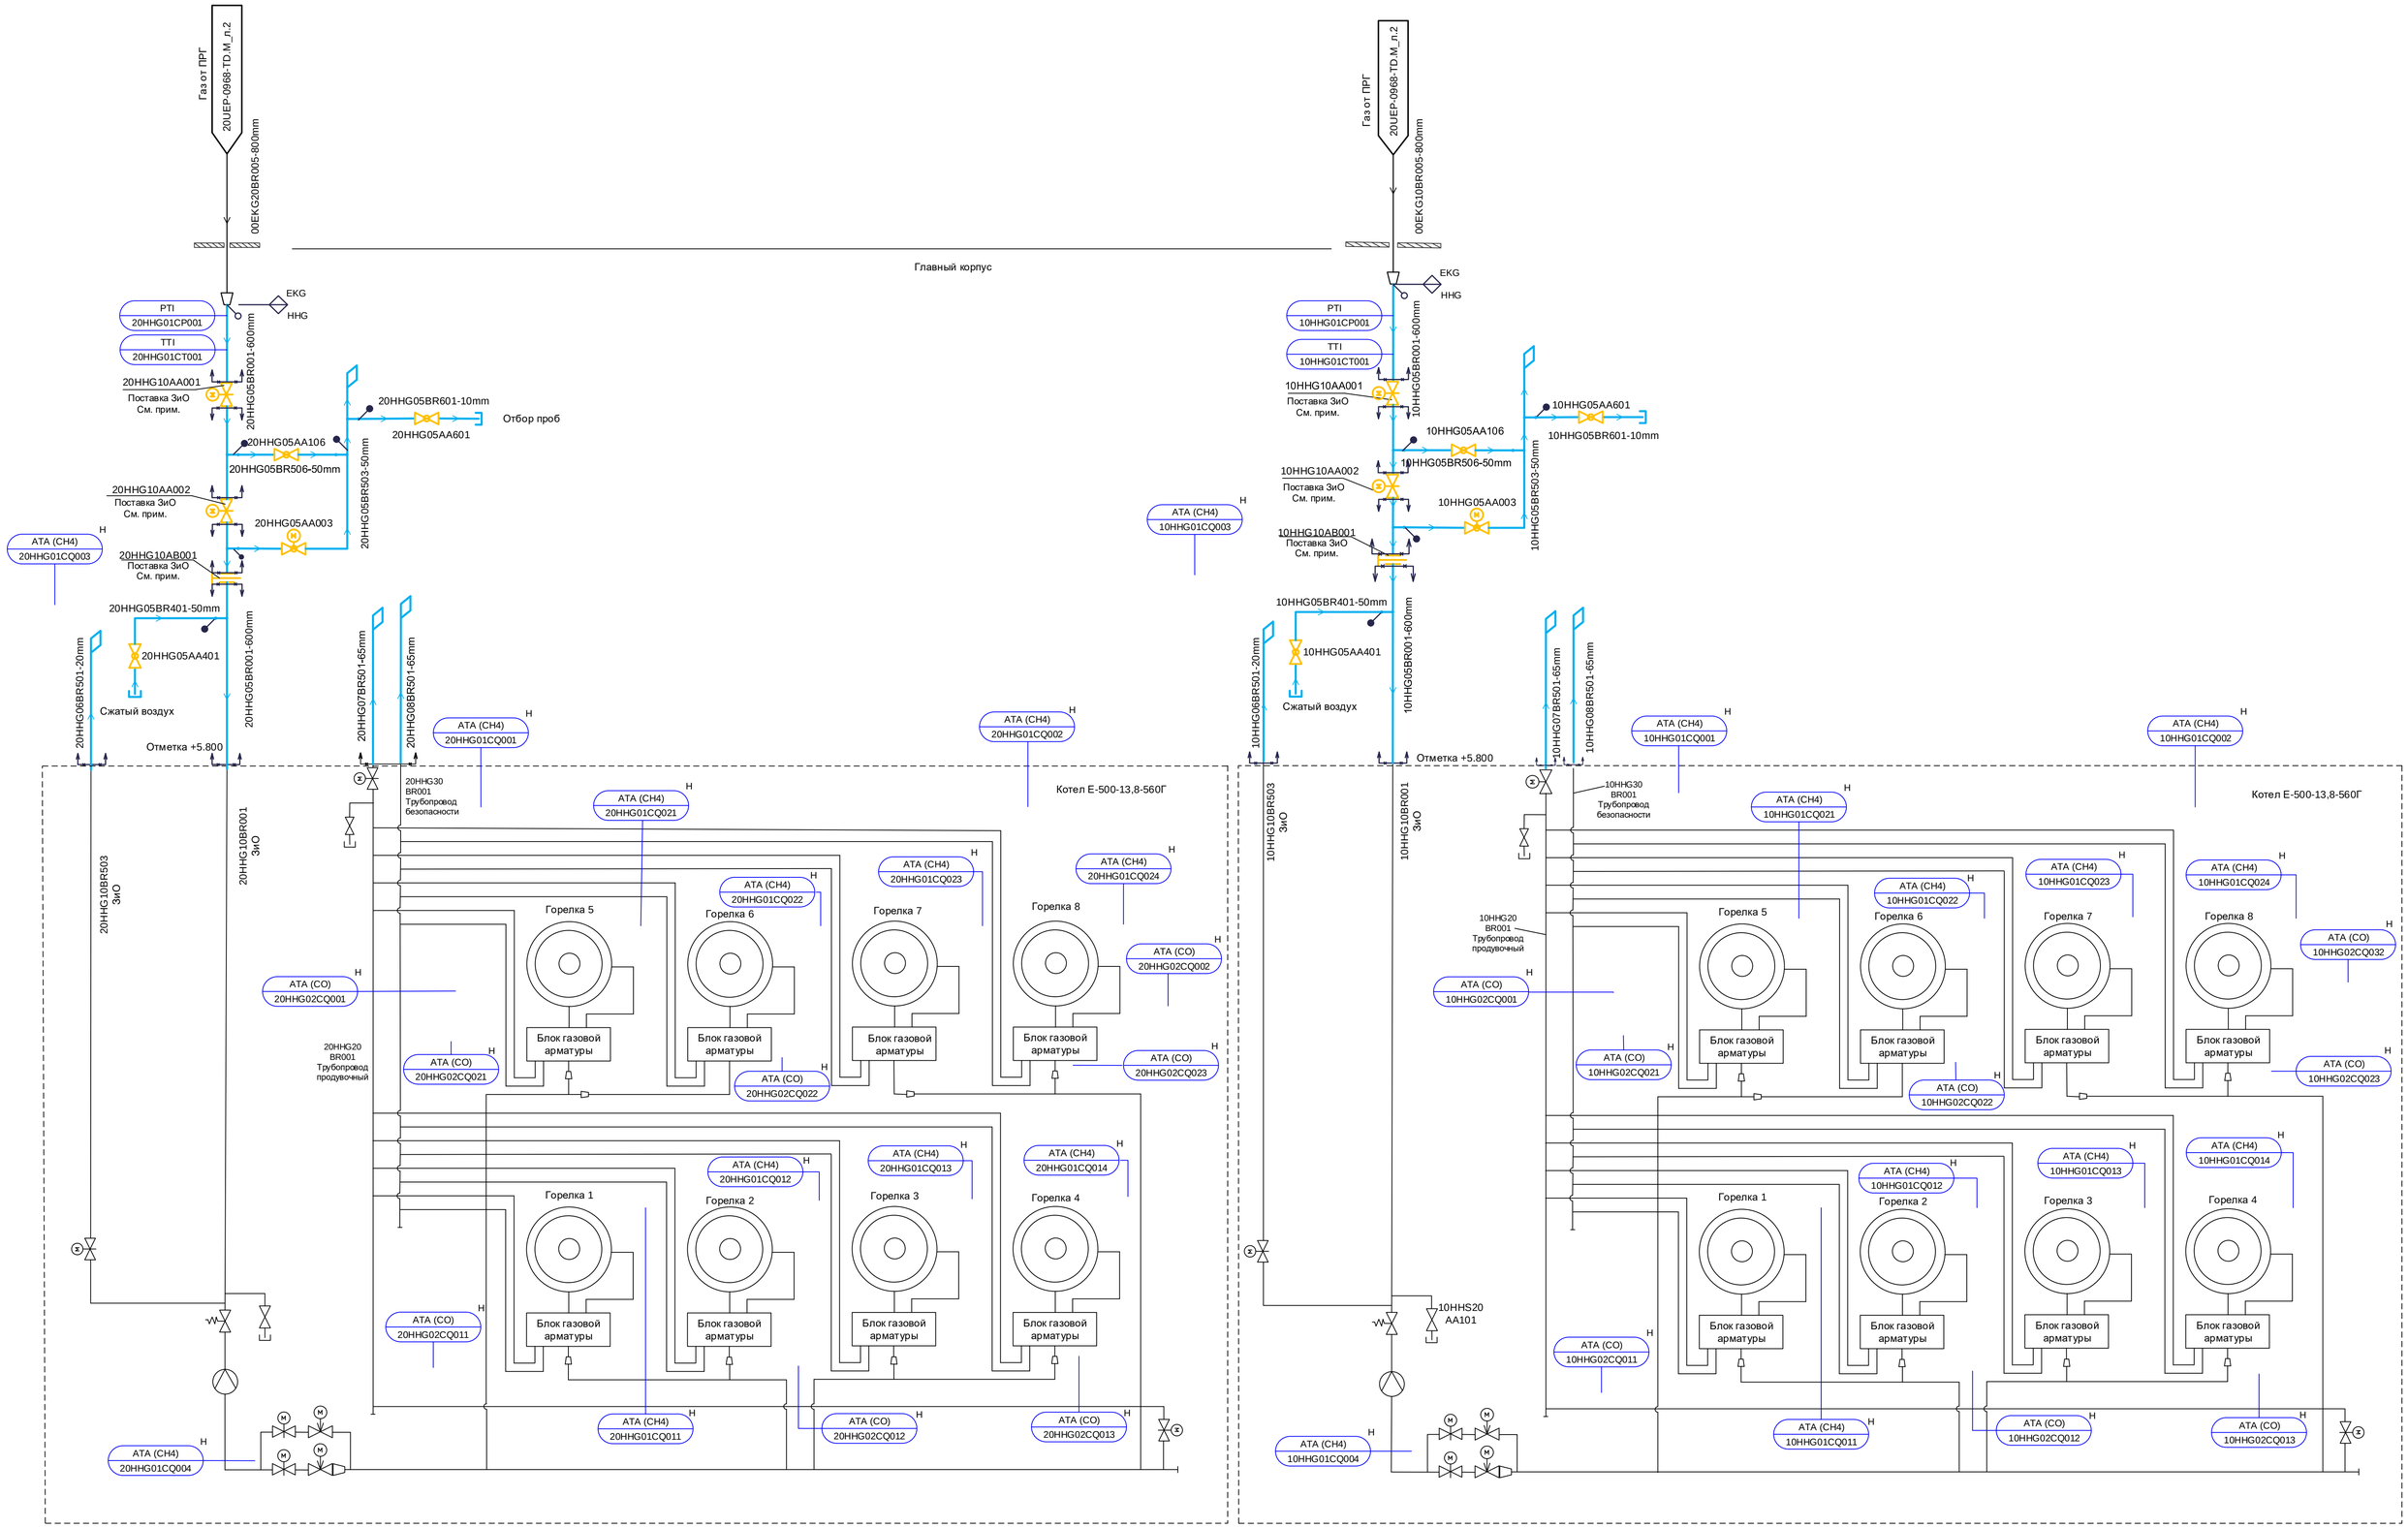

1. Арматура 10HHG10AA001, 10HHG10AA002, заглушка поворотная 10HHG10AB001 в поставке АО «ЗиО» поставляются вместе с оборудованием котла (см. документацию 171.20.384 Д АО «ЗиО») и устанавливаются на газопроводе 10HHG05BR001 DN600 к паровому котлу №1 в границах проектирования АО «Институт Теплоэлектропроект».
Аналогично для парового котла №2.
2. PI-Диаграмму газопроводов в пределах котла см. документ 171.20.00.023С2 АО «ЗиО».

						68N115 – 20UHJ – 6648 – TD.M		
3	-	Зам	2083-25		06.25	Строительство Якутской ГРЭС-2 (2-я очередь) Туймаада ТЭЦ		
Изм.	Кол.уч	Лист	№ док.	Подп.	Дата			
Разработал		Малеева			06.25	Главный корпус. PI-диаграмма газопроводов к паровым котлам	Стадия	Лист	Листов
Проверил		Машков					Р	2	
Нач.отдела		Мухаммадеев							
Н. контр.		Черемушкина				PI-диаграмма газопроводов к паровым котлам.	АКЦИОНЕРНОЕ ОБЩЕСТВО ИНСТИТУТ ТЕПЛОЭЛЕКТРОПРОЕКТ г. МОСКВА		

Согласовано

ОАСУ

Формат А1