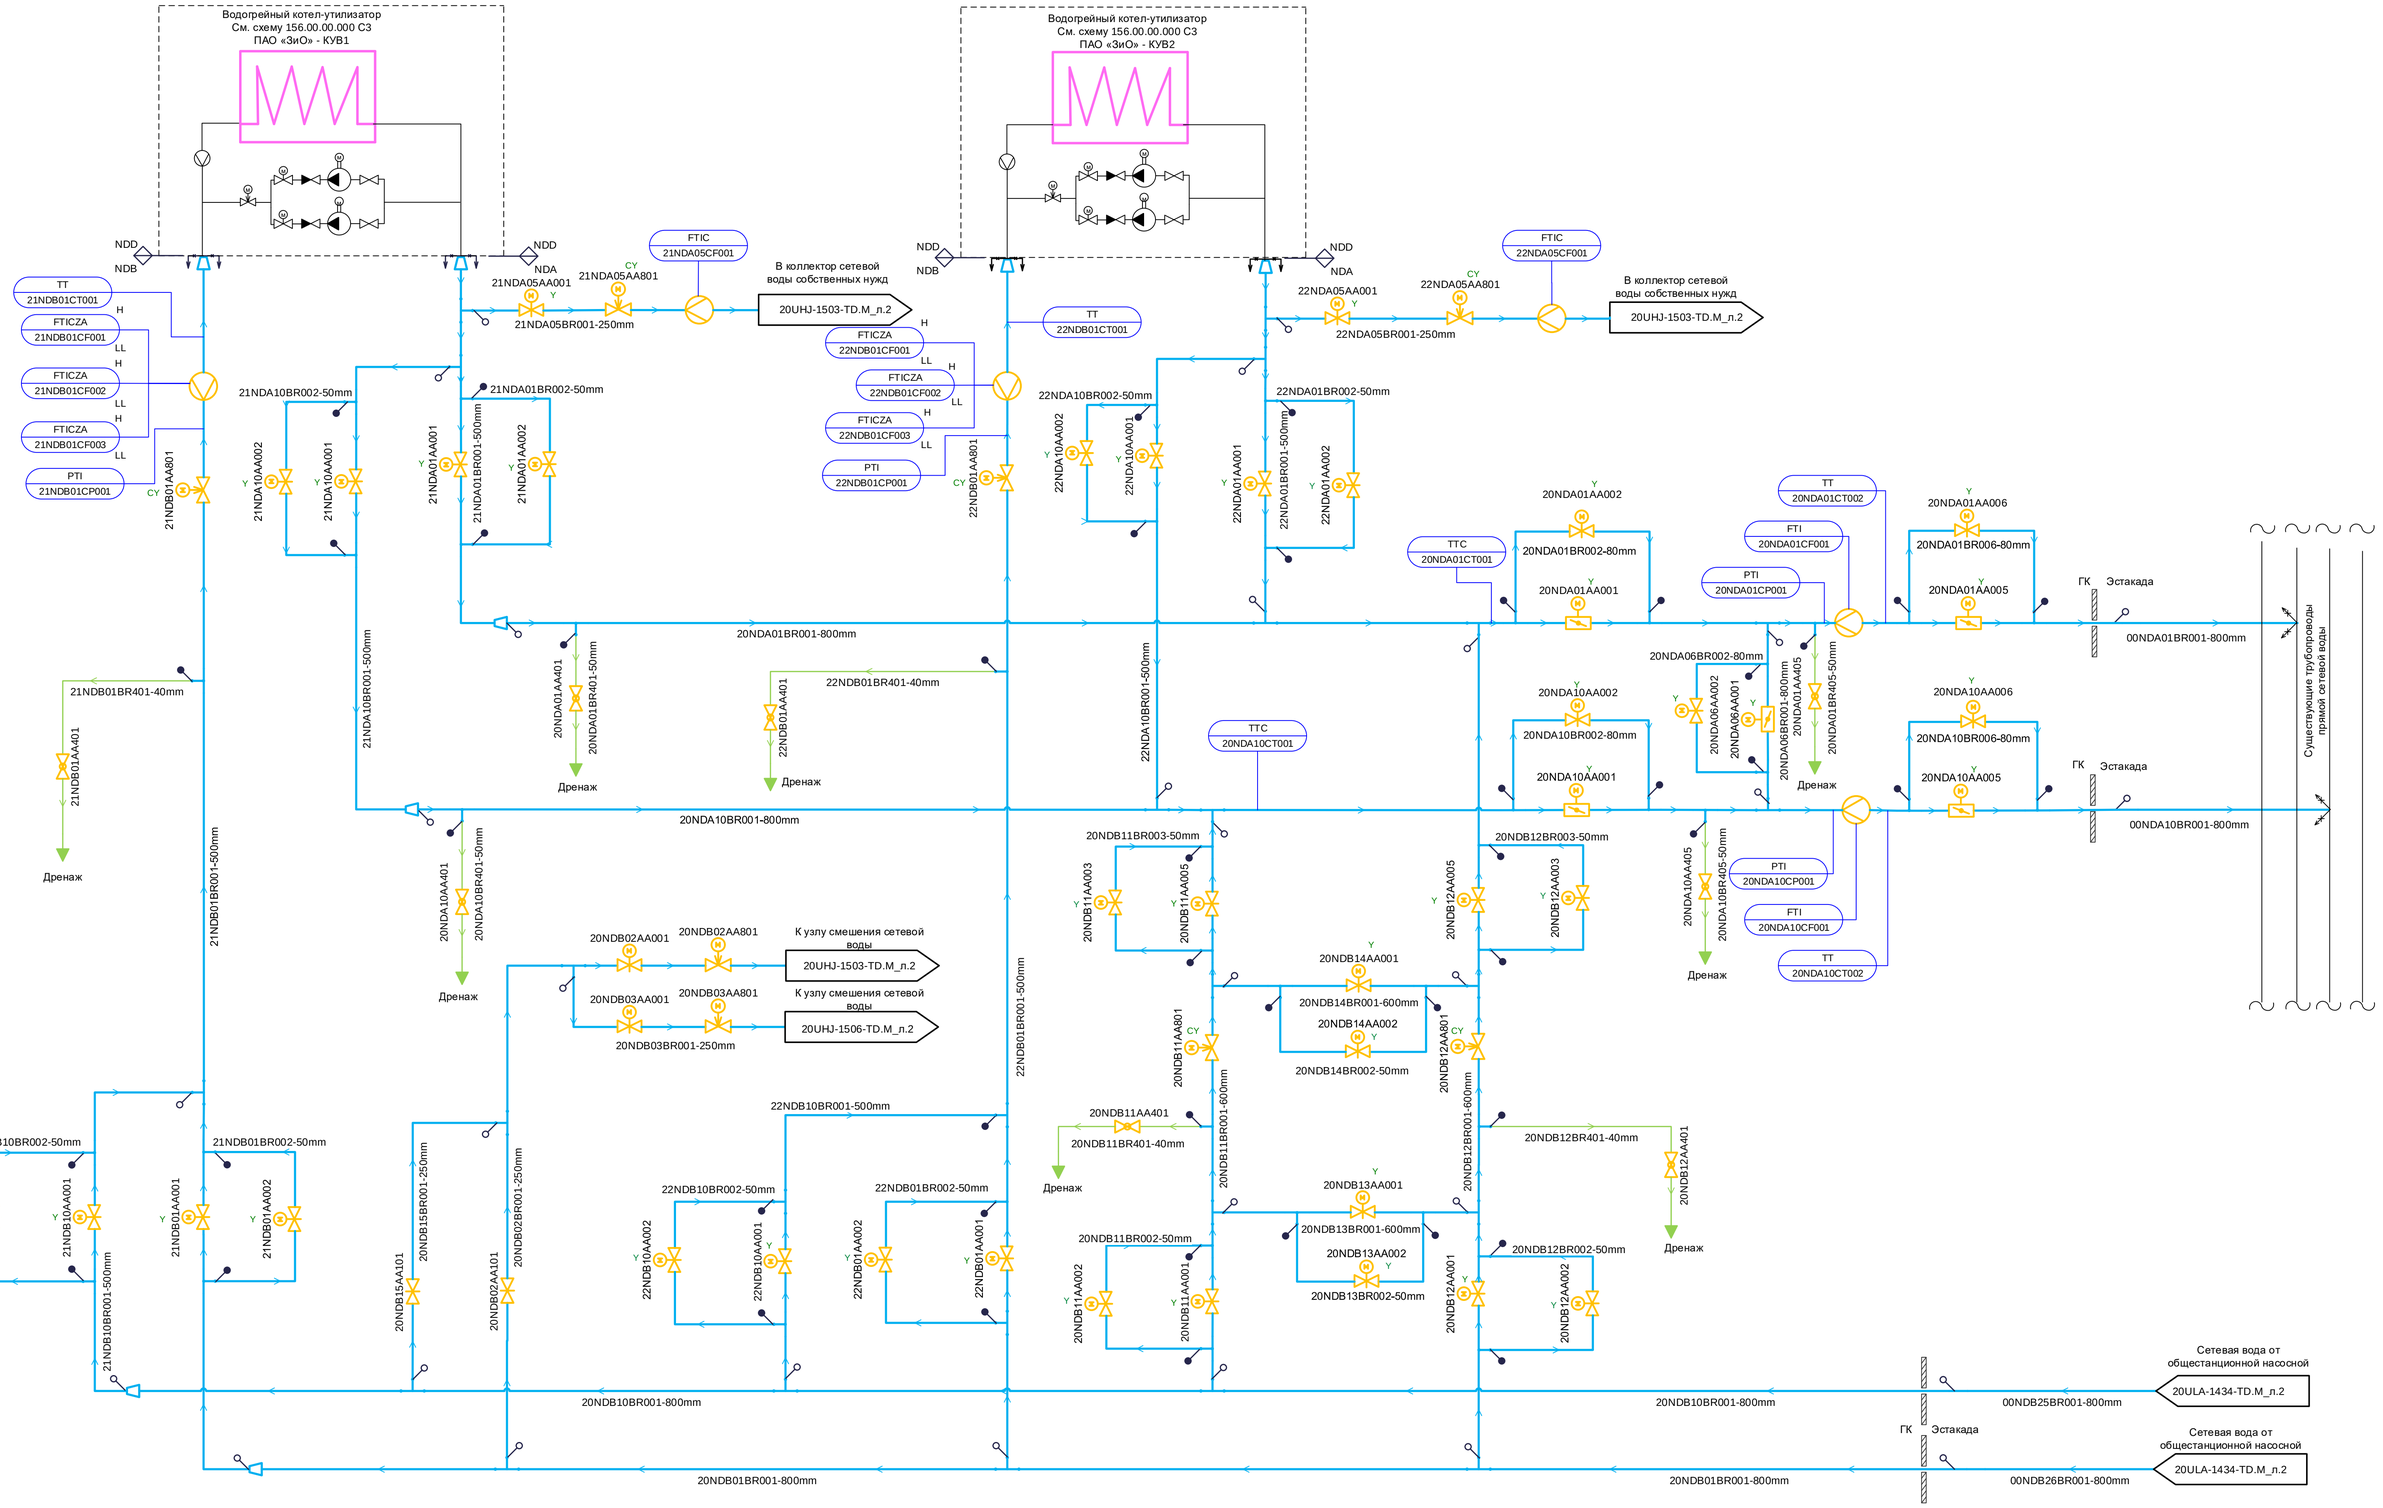

Изм.	Кол.уч	Лист	№ док.	Подп.	Дата	68N115 – 20UHJ – 1431 – TD.M
						Строительство Якутской ГРЭС-2 (2-я очередь)
Разработал		Демина				Главный корпус. PI-диаграмма трубопроводов сетевой воды ГК
Проверил		Пак				Стадия: Р; Лист: 2; Листов:
Н. контр.		Астраханцев				PI-диаграмма трубопроводов сетевой воды ГК. Система NDA, NDB

АКЦИОНЕРНОЕ ОБЩЕСТВО ИНСТИТУТ ТЕПЛОЭЛЕКТРОПРОЕКТ г. МОСКВА

Согласовано: ОАСУ Круговых

Взам. инв. №

Подпись и дата

Инв. № подл.

Формат А1