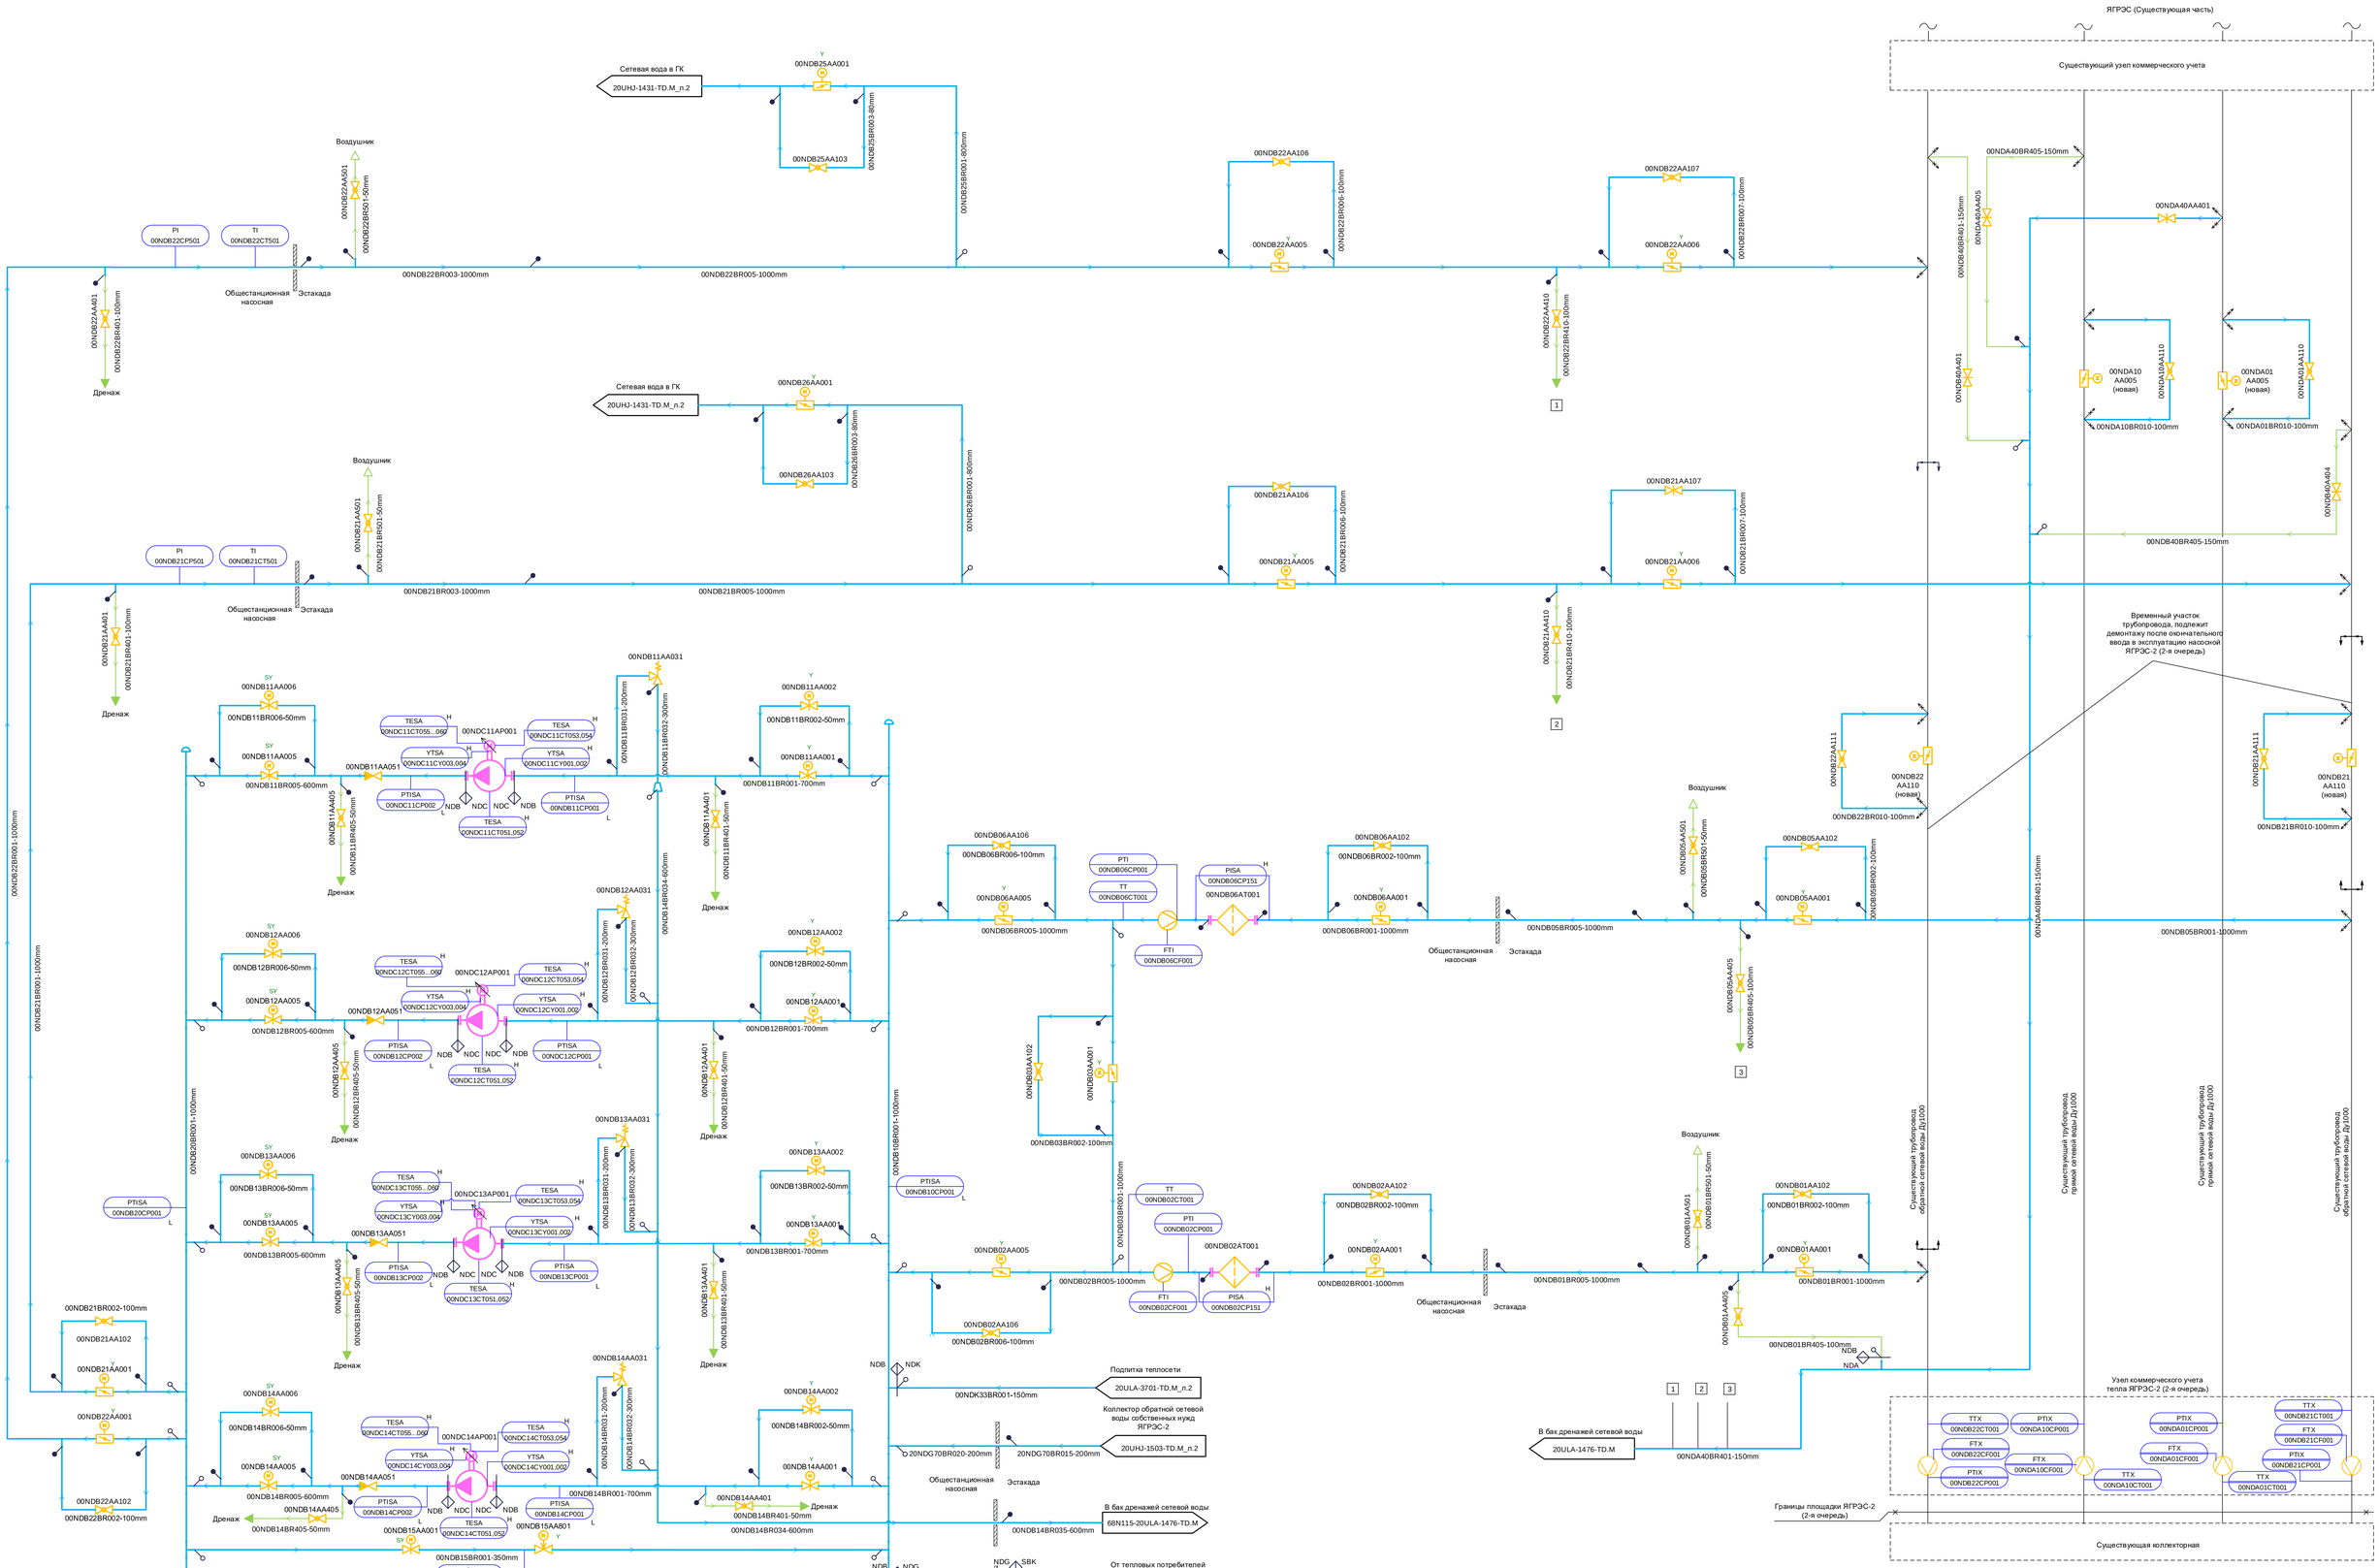

Обвязка насосов сетевой воды датчиками КИП и А может быть уточнена после получения ИД от Поставщика.

						68N115 – 20ULA – 1434 – TD.M	
						Строительство Якутской ГРЭС-2 (2-я очередь)	
Изм.	Кол.уч.	Лист	№ док.	Подп.	Дата		
Разработал		Демина				Общестанционная насосная. PI-диаграмма трубопроводов сетевой воды общестанционной насосной	Стадия: P; Лист: 2; Листов:
Проверил		Пак					
Н. контр.		Астраханцев				PI-диаграмма трубопроводов сетевой воды общестанционной насосной. Система NDA, NDB	АКЦИОНЕРНОЕ ОБЩЕСТВО «ТЕХЭНЕРГОПРОМ»

Согласовано

Взам. инв. №

Подпись и дата

Инв. № подл.

ОАКУ

Семенова

Формат А0