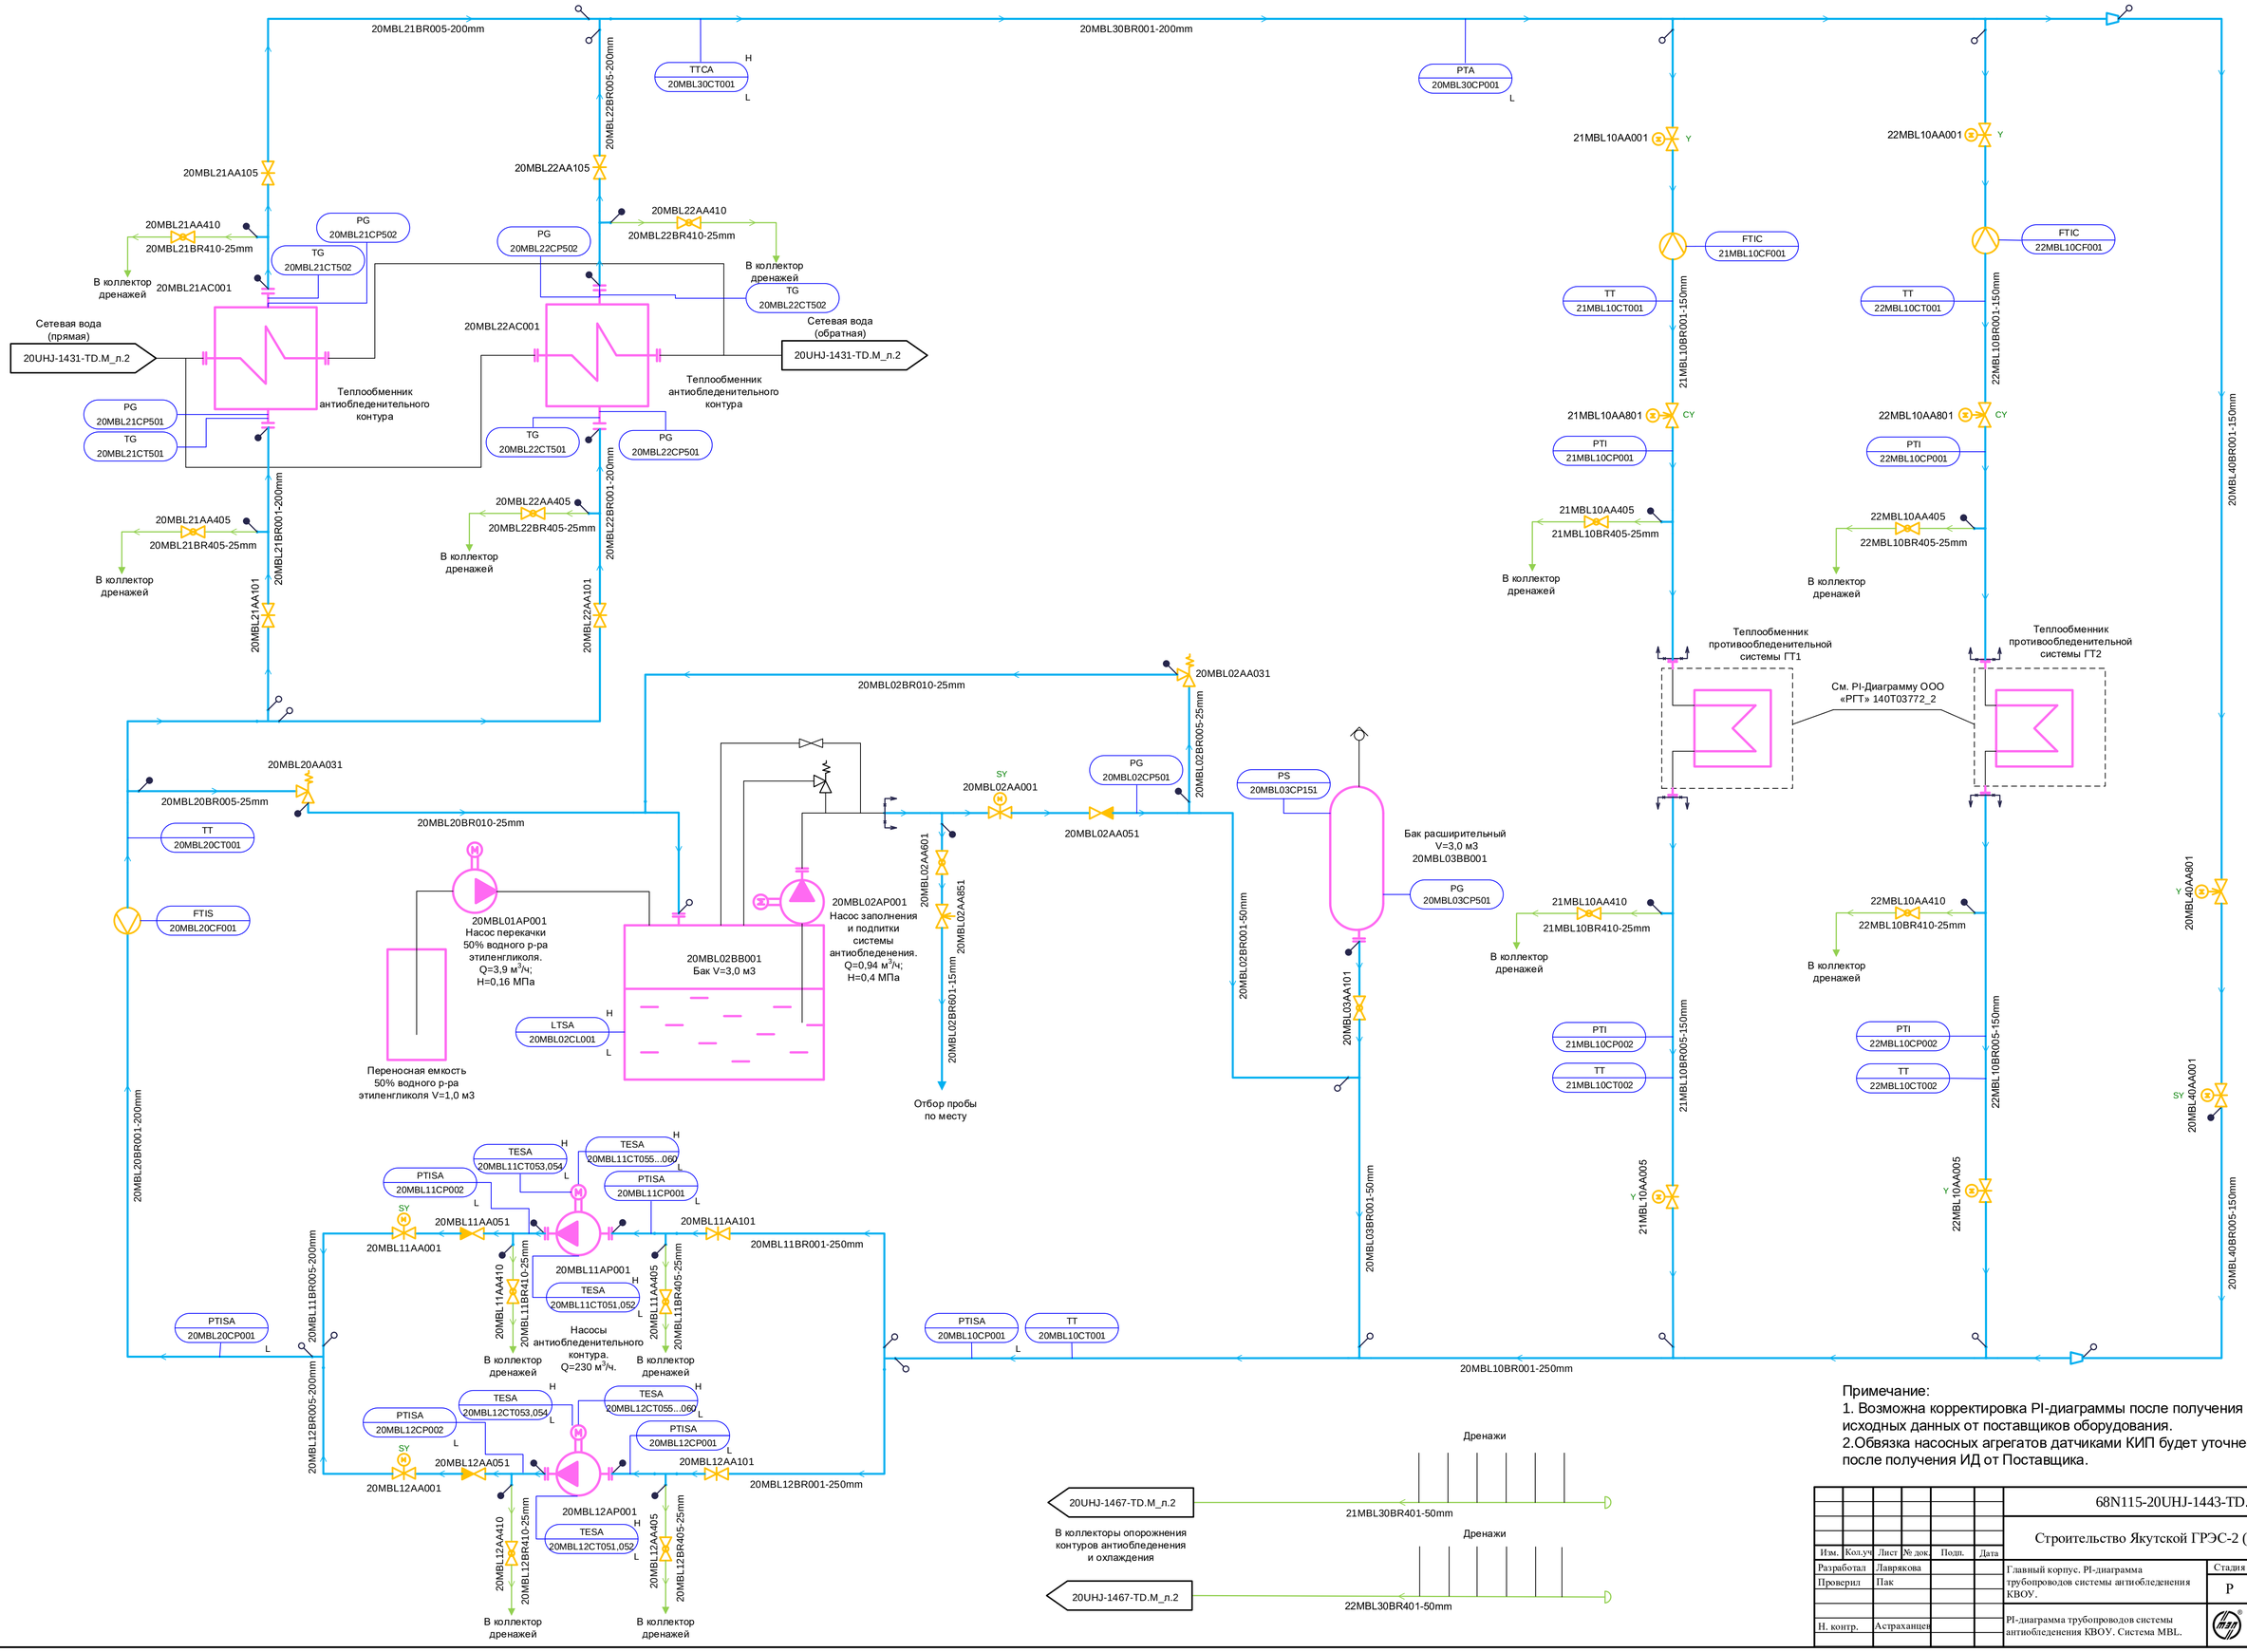

Примечание:
1. Возможна корректировка PI-диаграммы после получения исходных данных от поставщиков оборудования.
2.Обвязка насосных агрегатов датчиками КИП будет уточнена после получения ИД от Поставщика.

						68N115-20UHJ-1443-TD.M		
						Строительство Якутской ГРЭС-2 (2-я очередь)		
Изм.	Кол.уч	Лист	№ док.	Подп.	Дата			
Разработал		Лаврякова				Главный корпус, PI-диаграмма трубопроводов системы антиобледенения КВОУ.	Стадия	Лист	Листов
Проверил		Пак					Р	2	
Н. контр.		Астраханцев				PI-диаграмма трубопроводов системы антиобледенения КВОУ. Система MBL.	АКЦИОНЕРНОЕ ОБЩЕСТВО ИНСТИТУТ ТЕПЛОЭЛЕКТРОПРОЕКТ г. МОСКВА	

Согласовано
ОАСУ
Взам. инв. №
Подпись и дата
Инв. № подл.

Формат А1