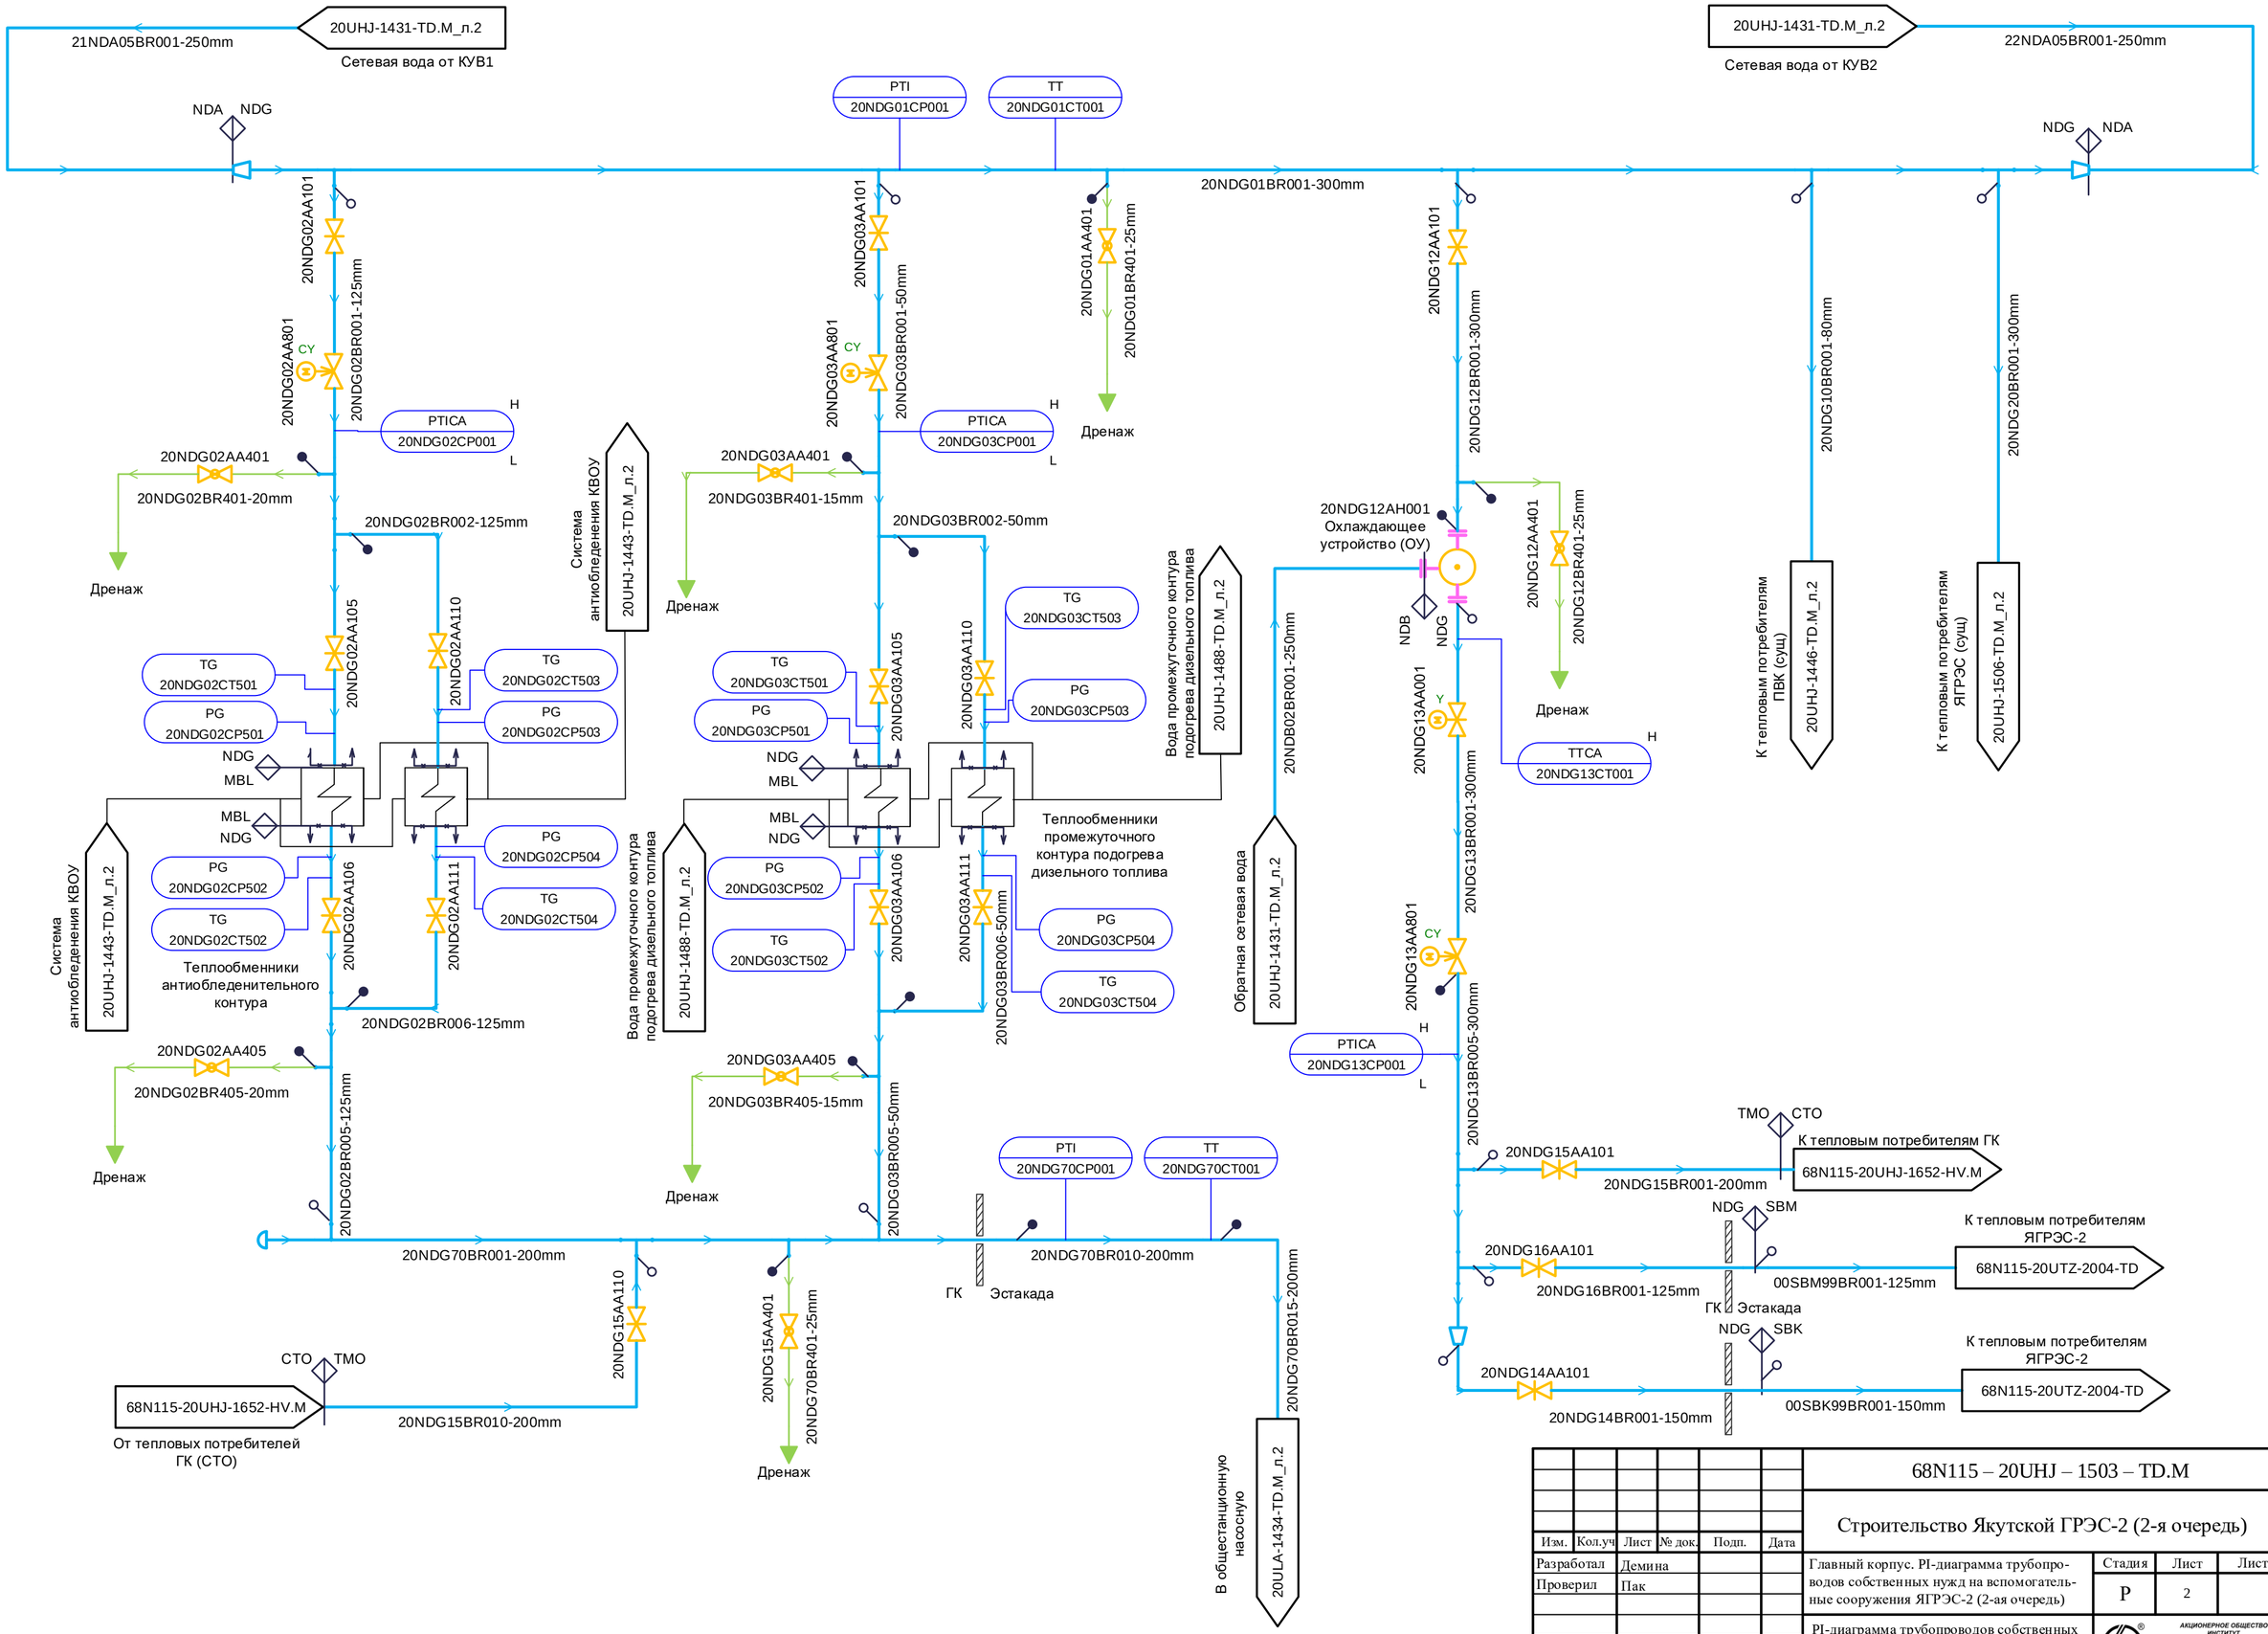

Изм.	Кол.уч	Лист	№ док.	Подп.	Дата
Разработал		Демина			
Проверил		Пак			
Н. контр.		Астраханцев			

68N115 – 20UHJ – 1503 – TD.M

Строительство Якутской ГРЭС-2 (2-я очередь)

Главный корпус. PI-диаграмма трубопроводов собственных нужд на вспомогательные сооружения ЯГРЭС-2 (2-ая очередь)

Стадия	Лист	Листов
Р	2	

PI-диаграмма трубопроводов собственных нужд на вспомогательные сооружения ЯГРЭС-2 (2-ая очередь). Система NDA, NDB

АКЦИОНЕРНОЕ ОБЩЕСТВО ИНСТИТУТ ТЕПЛОЭЛЕКТРОПРОЕКТ Г. МОСКВА

Согласовано

ОАСУ Круговых

Взам. инв. №

Подпись и дата

Инв. № подл.

Формат А2