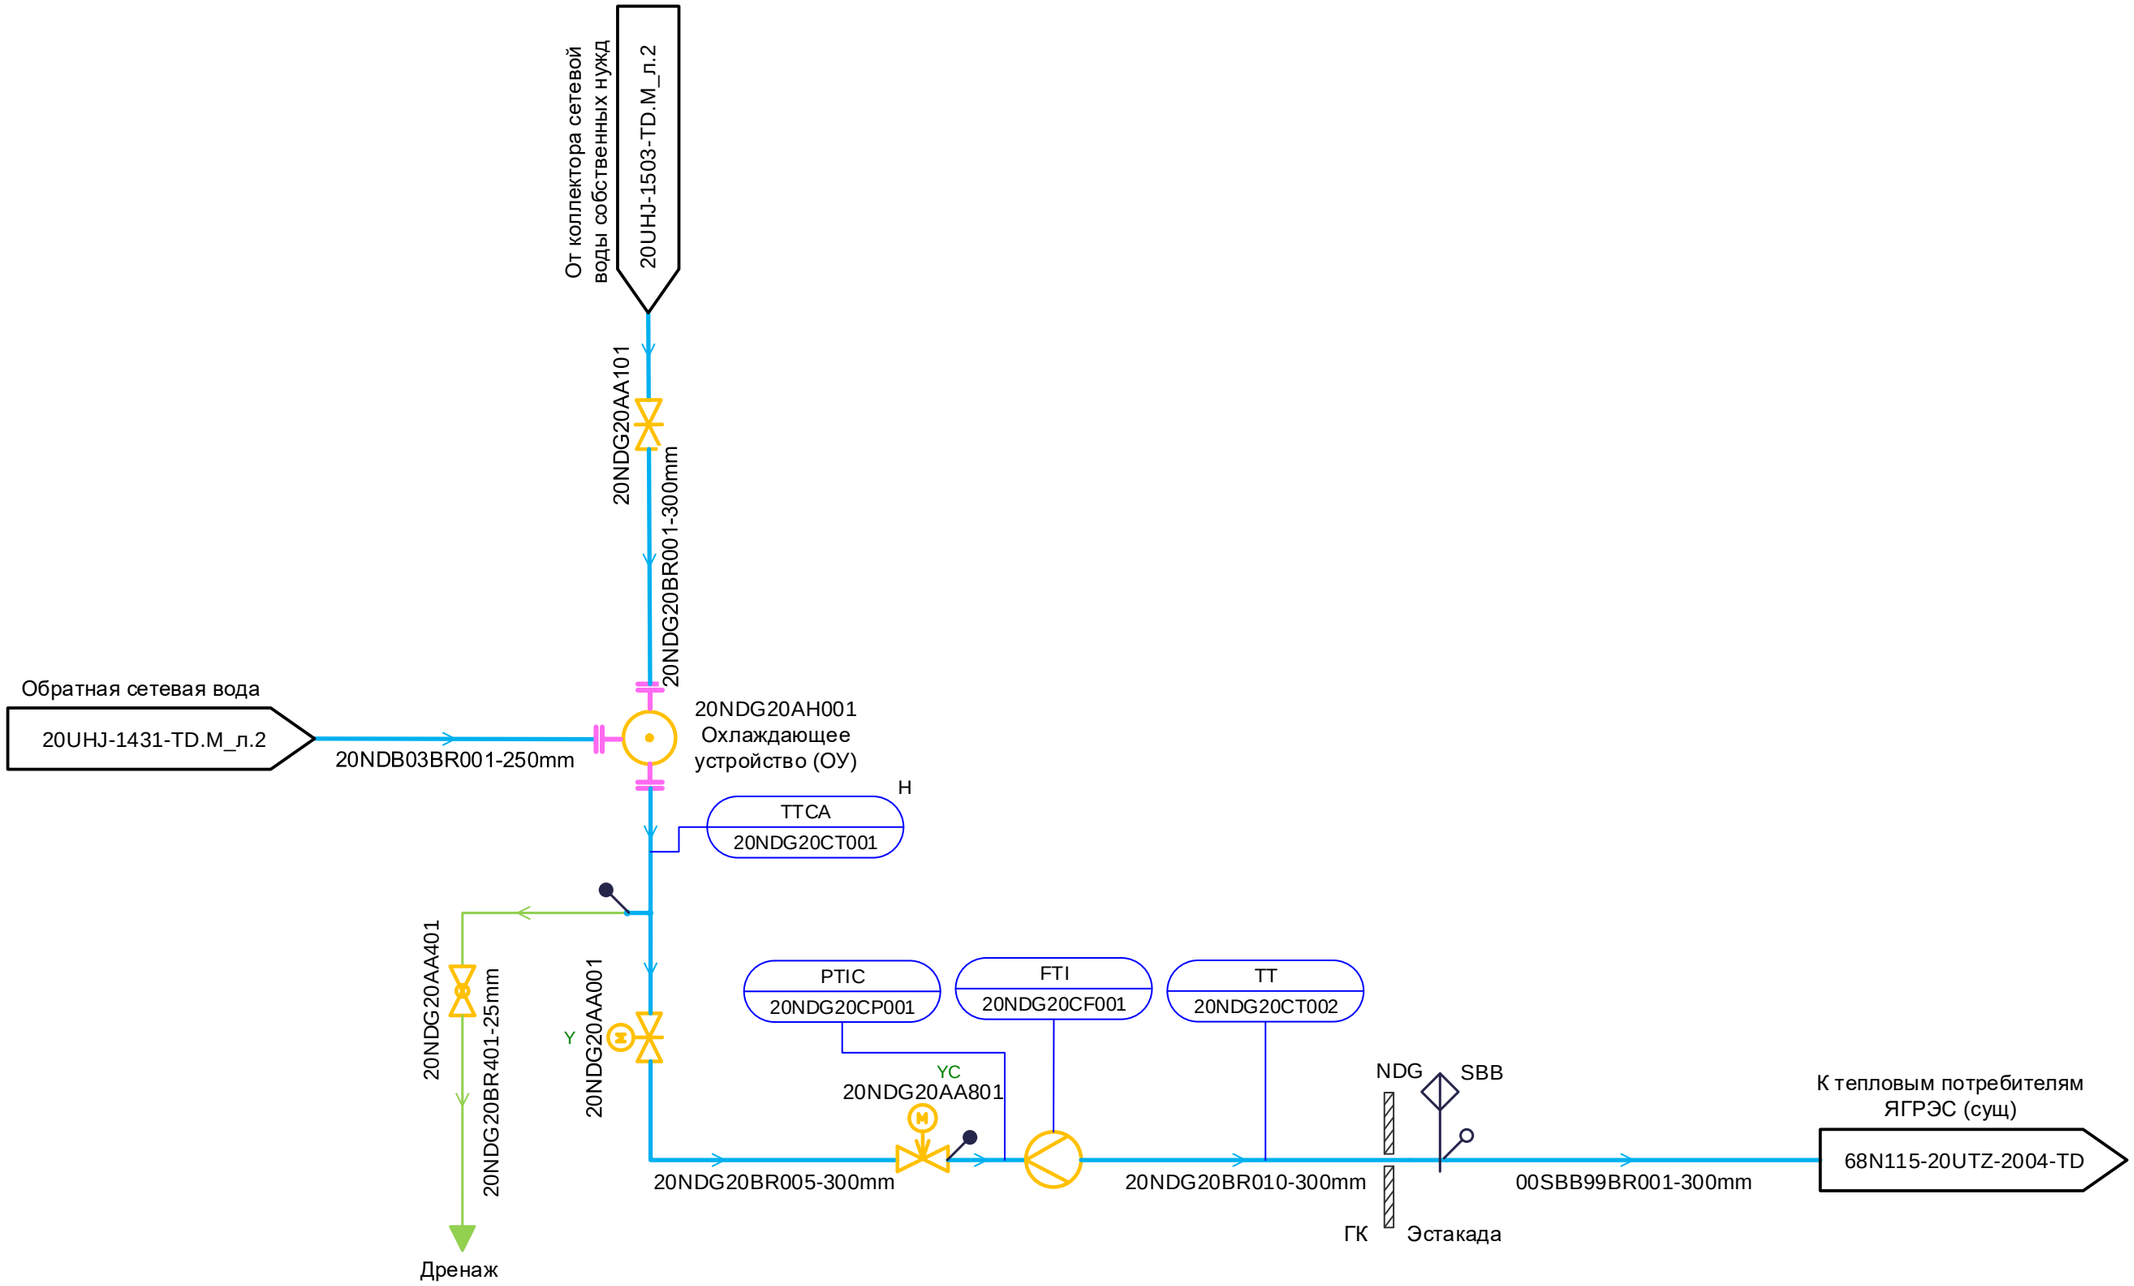

Примечание: Значение рабочего давления трубопровода сетевой воды к тепловым потребителям ЯГРЭС (сущ) может быть уточнено после получения информации от Заказчика.

Изм.	Кол.уч	Лист	№ док.	Подп.	Дата
Разработал		Демина			
Проверил		Пак			
Н. контр.		Астраханцев			

68N115 – 20UHJ – 1506 – TD.M

Строительство Якутской ГРЭС-2 (2-я очередь)

Главный корпус. PI-диаграмма трубопроводов собственных нужд на вспомогательные сооружения существующей ЯГРЭС

Стадия	Лист	Листов
Р	2	

PI-диаграмма трубопроводов собственных нужд на вспомогательные сооружения существующей ЯГРЭС. Система NDA, NDB

АКЦИОНЕРНОЕ ОБЩЕСТВО ИНСТИТУТ ТЕПЛОЭЛЕКТРОПРОЕКТ Г. МОСКВА

Согласовано

Круговых

ОАСУ

Взам. инв. №

Подпись и дата

Инв. № подл.

Формат А3