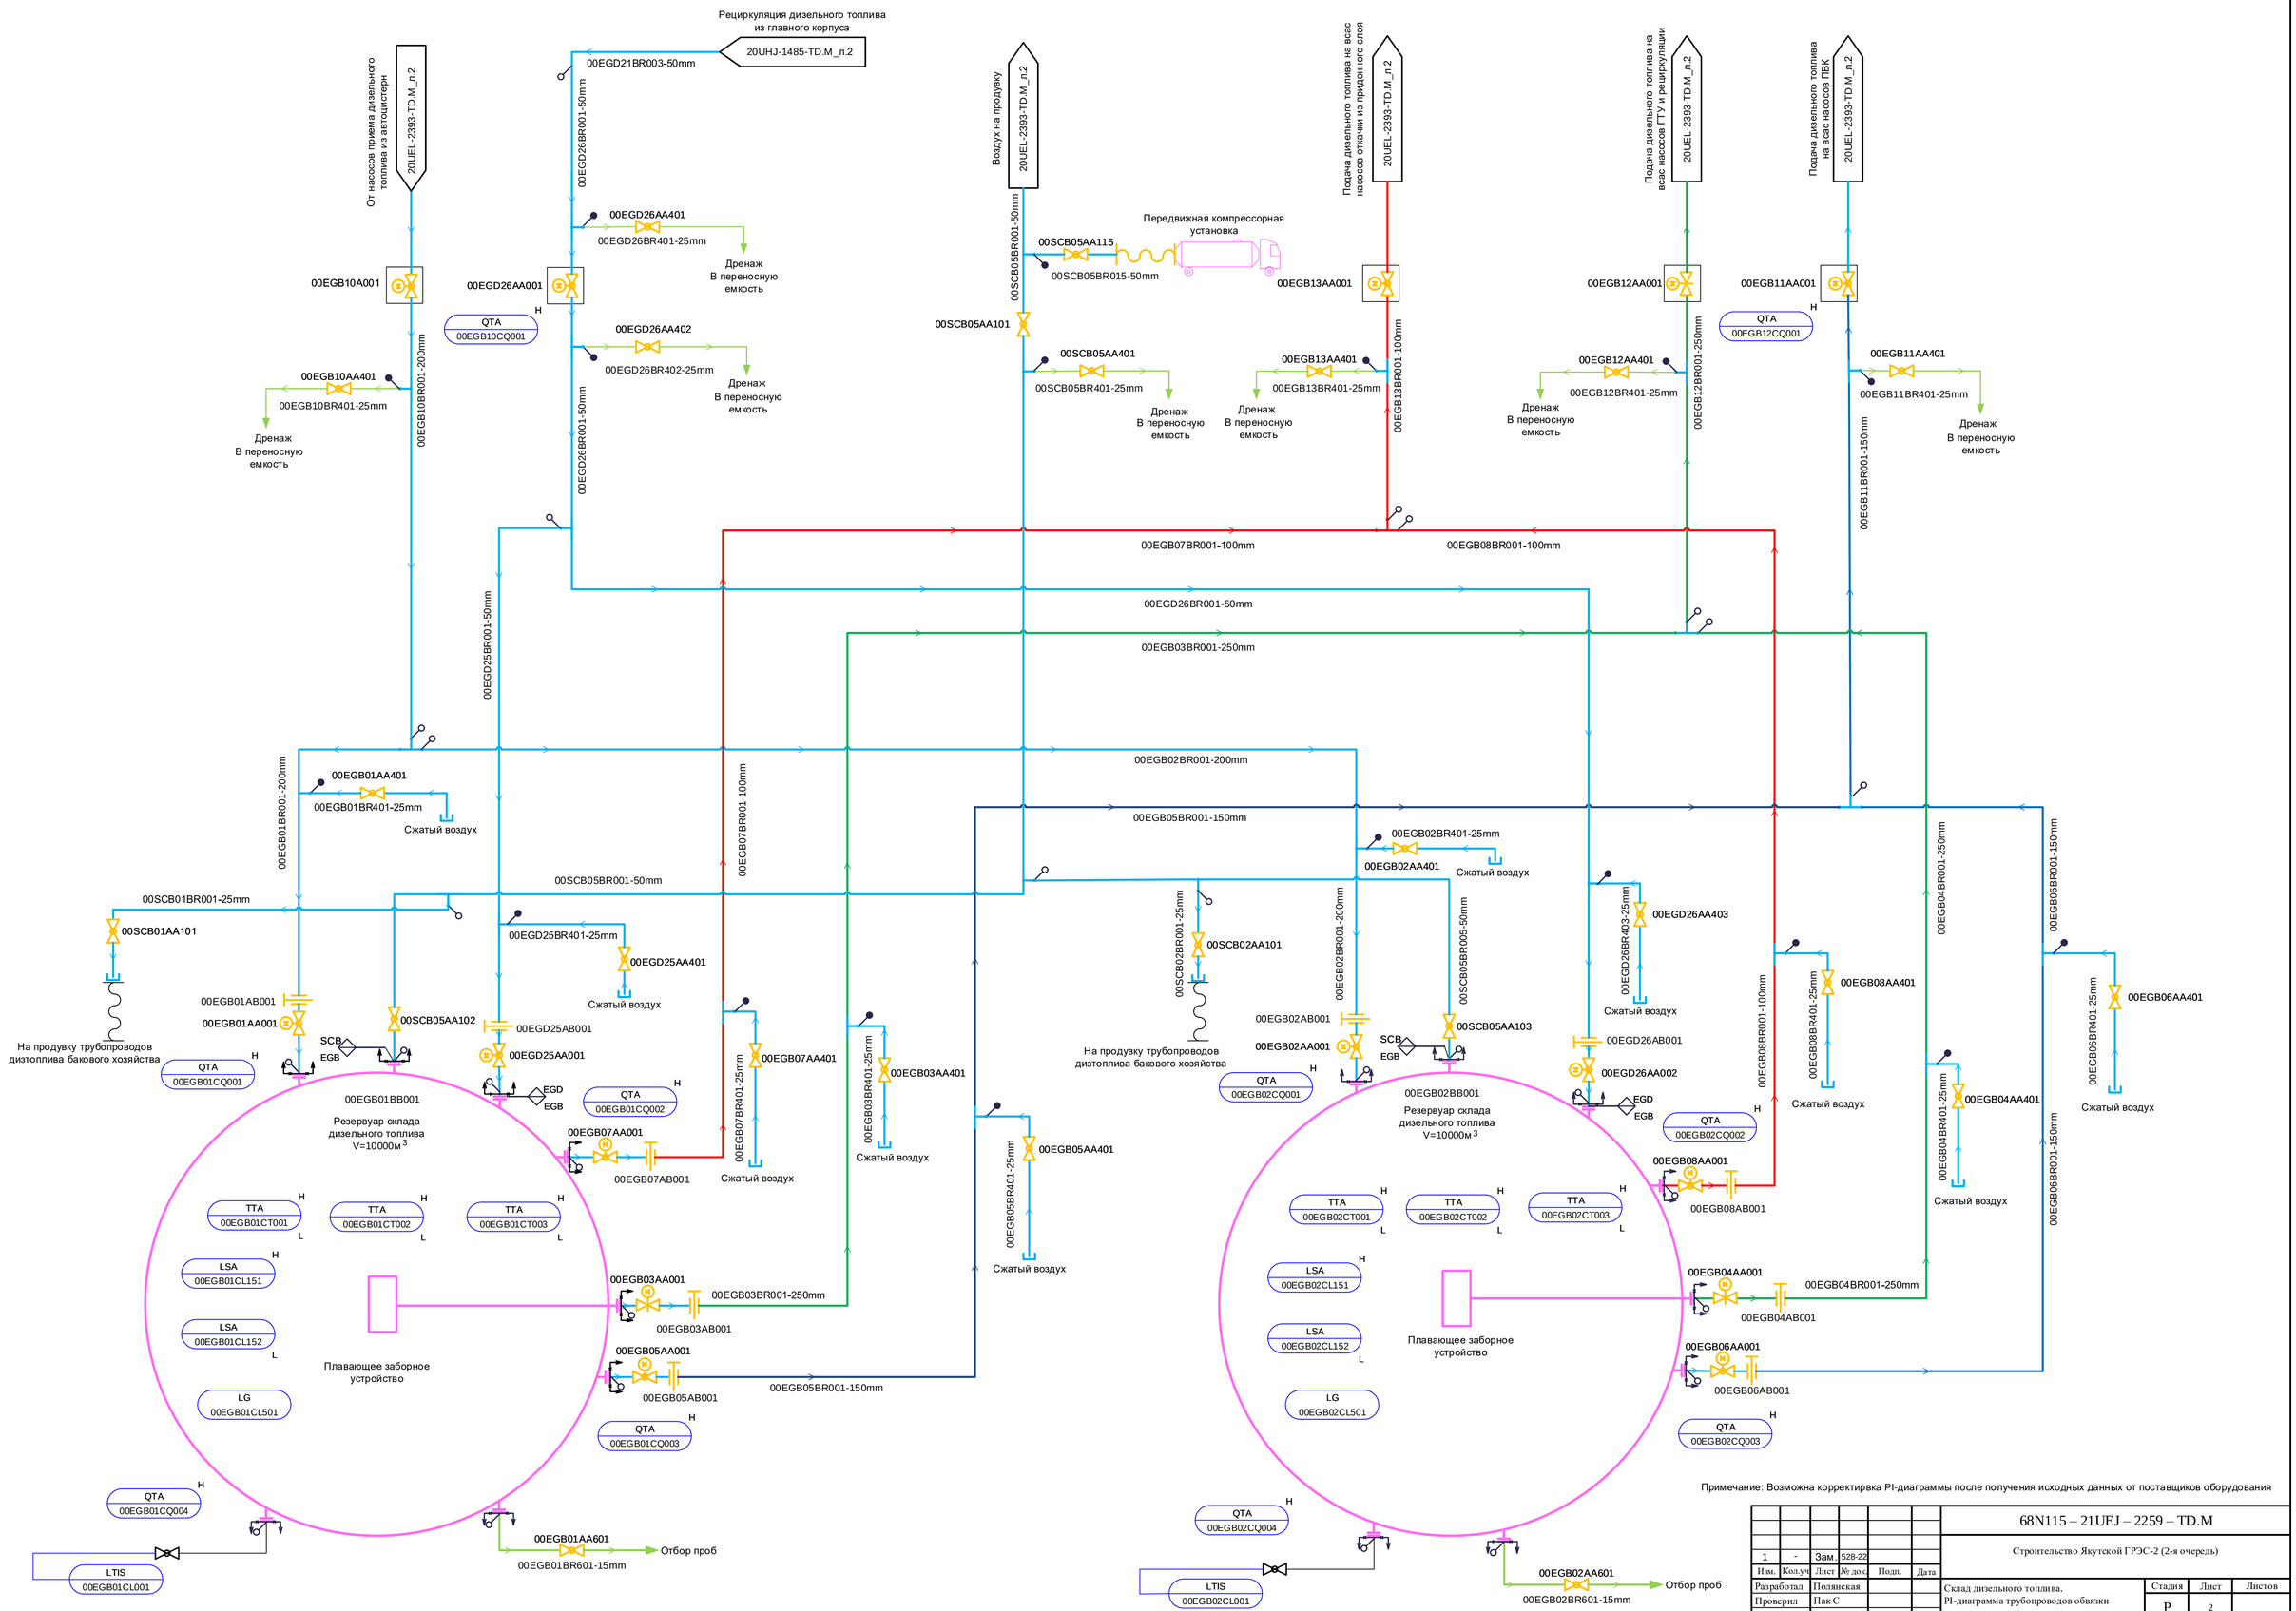

Примечание: Возможна корректировка PI-диаграммы после получения исходных данных от поставщиков оборудования

						68N115 – 21UEJ – 2259 – TD.M			
1	-	Зам.	528-22			Строительство Якутской ГРЭС-2 (2-я очередь)			
Изм.	Кол.уч	Лист	№ док.	Подп.	Дата				
Разработал	Полянская					Склад дизельного топлива. PI-диаграмма трубопроводов обвязки резервуаров склада дизельного топлива	Стадия	Лист	Листов
Проверил	Пак С						Р	2	
Н. контр.	Черемушкина					PI-диаграмма трубопроводов обвязки резервуаров склада дизельного топлива. Система EGA, EGB, SCB	АКЦИОНЕРНОЕ ОБЩЕСТВО ИНСТИТУТ ТЕПЛОЭЛЕКТРОПРОЕКТ г. МОСКВА		

Согласовано

ОАСУ Крутовых

Взам. инв. №

Подпись и дата

Инв. № подл.

Формат А1