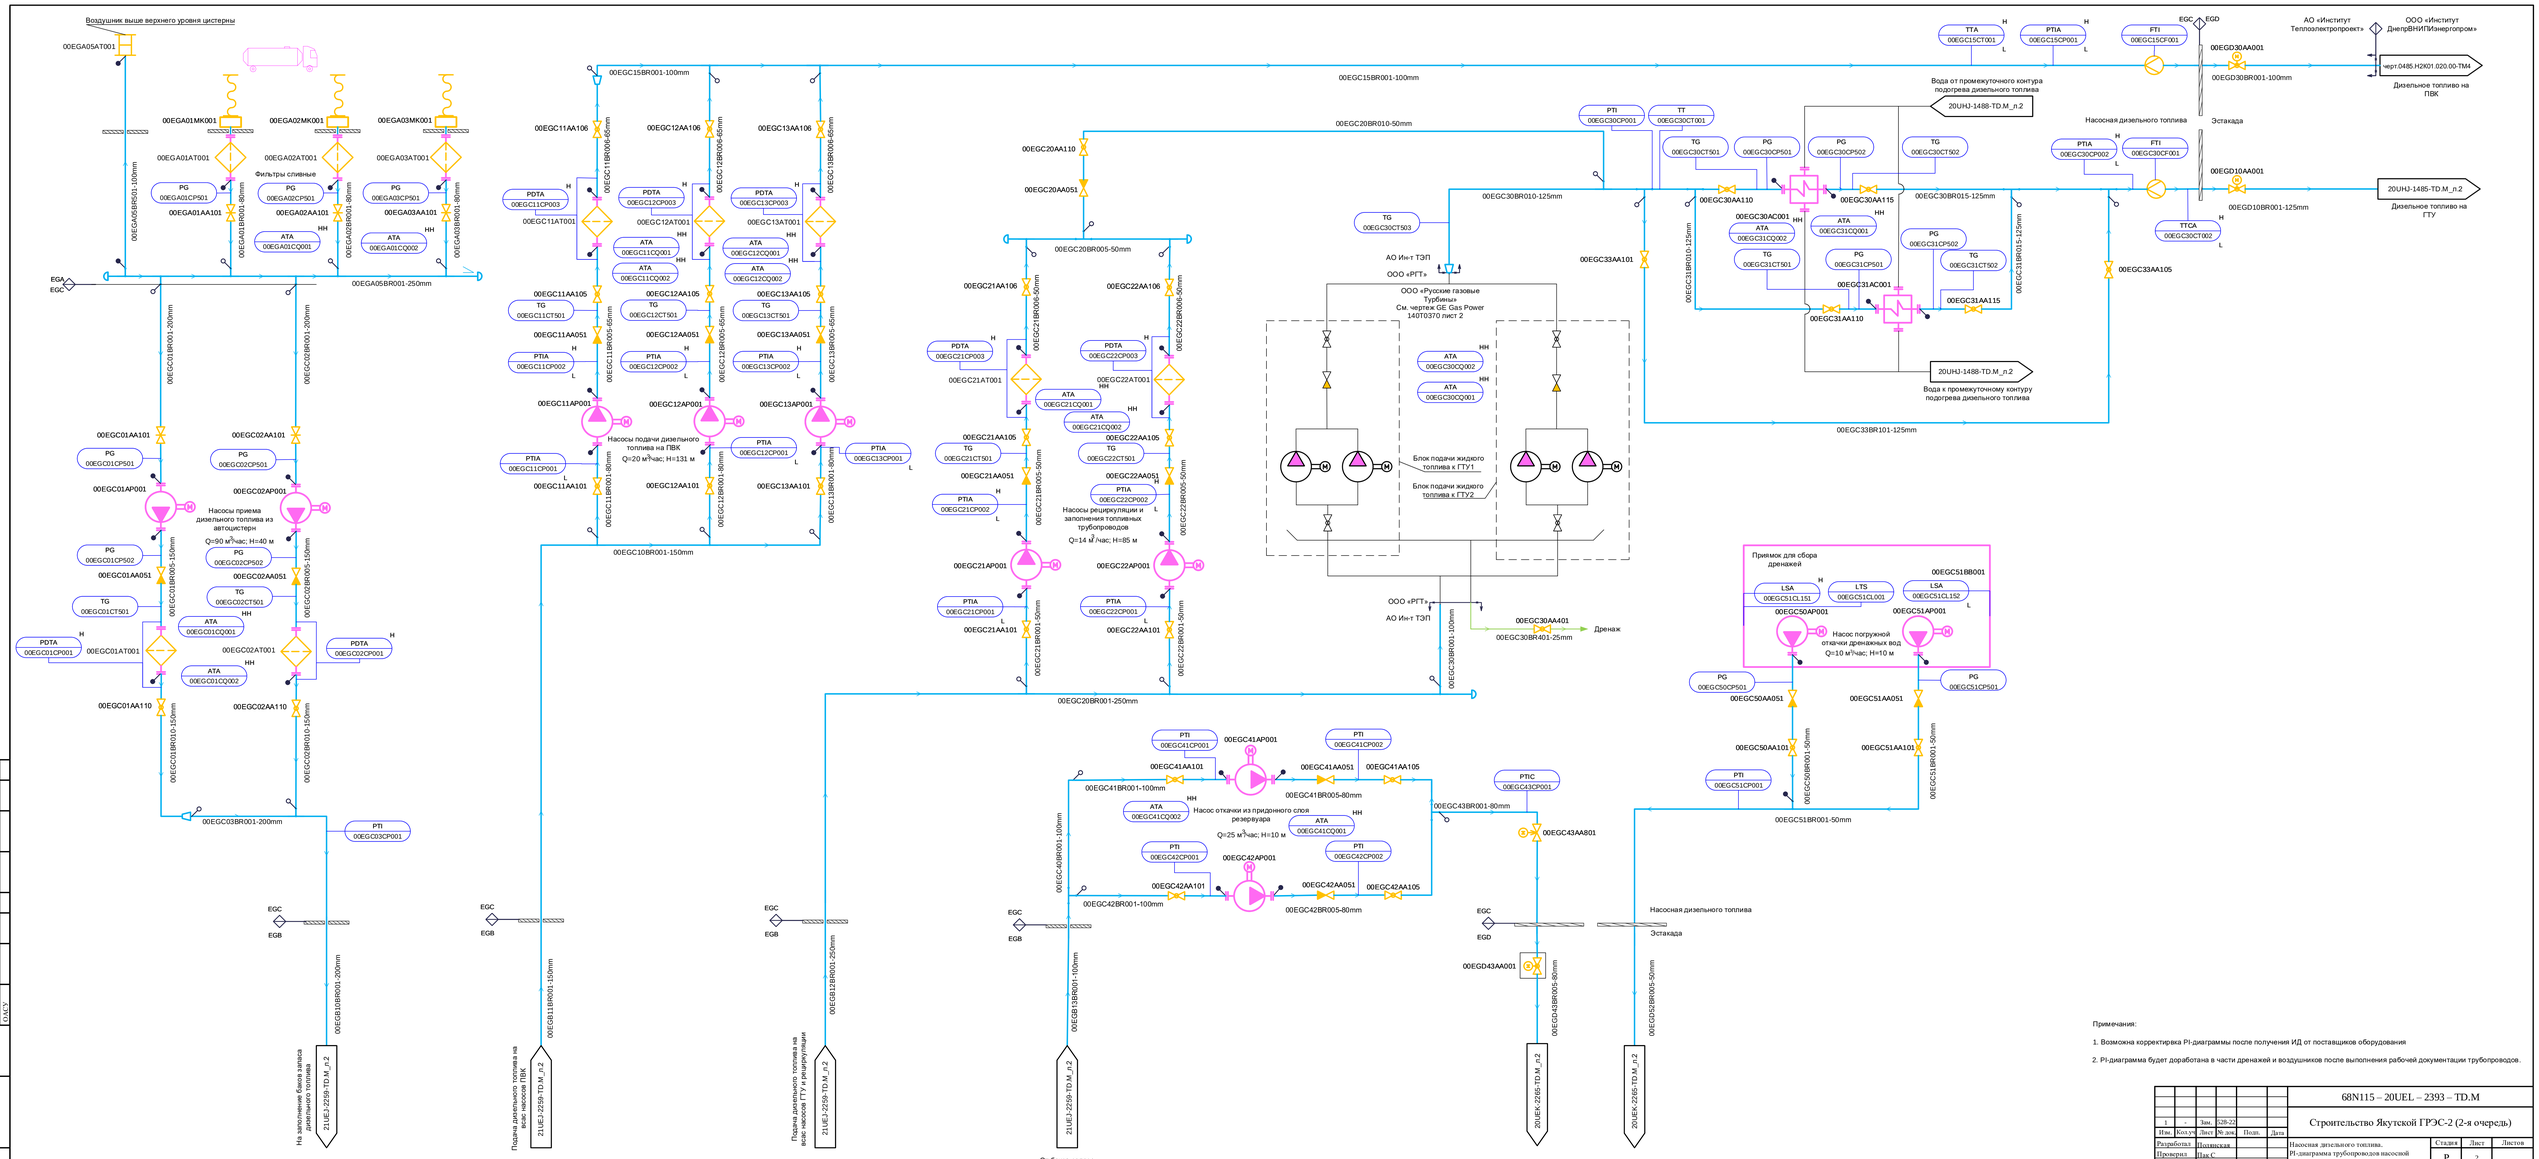

Примечания:

1. Возможна корректировка PI-диаграммы после получения ИД от поставщиков оборудования

2. PI-диаграмма будет доработана в части дренажей и воздушников после выполнения рабочей документации трубопроводов.

1	-	Зам.	528-22			68N115 – 20UEL – 2393 – TD.M	
Изм.	Кол.уч.	Лист	№ док.	Подп.	Дата	Строительство Якутской ГРЭС-2 (2-я очередь)	
Разработал		Подписная				Насосная дизельного топлива. PI-диаграмма трубопроводов насосной дизельного топлива.	Стадия: Р; Лист: 2; Листов:
Проверил		Нач.С					
Н. контр.		Астраханцев				PI-диаграмма трубопроводов насосной дизельного топлива. Система EGA, EGC	ТЕХНОЭКСПОРТ ГЕОТЕК

Согласовано

ОАО "Э"

Взам. инв. №

Подпись и дата

Инв. № подл.

Формат А2х3