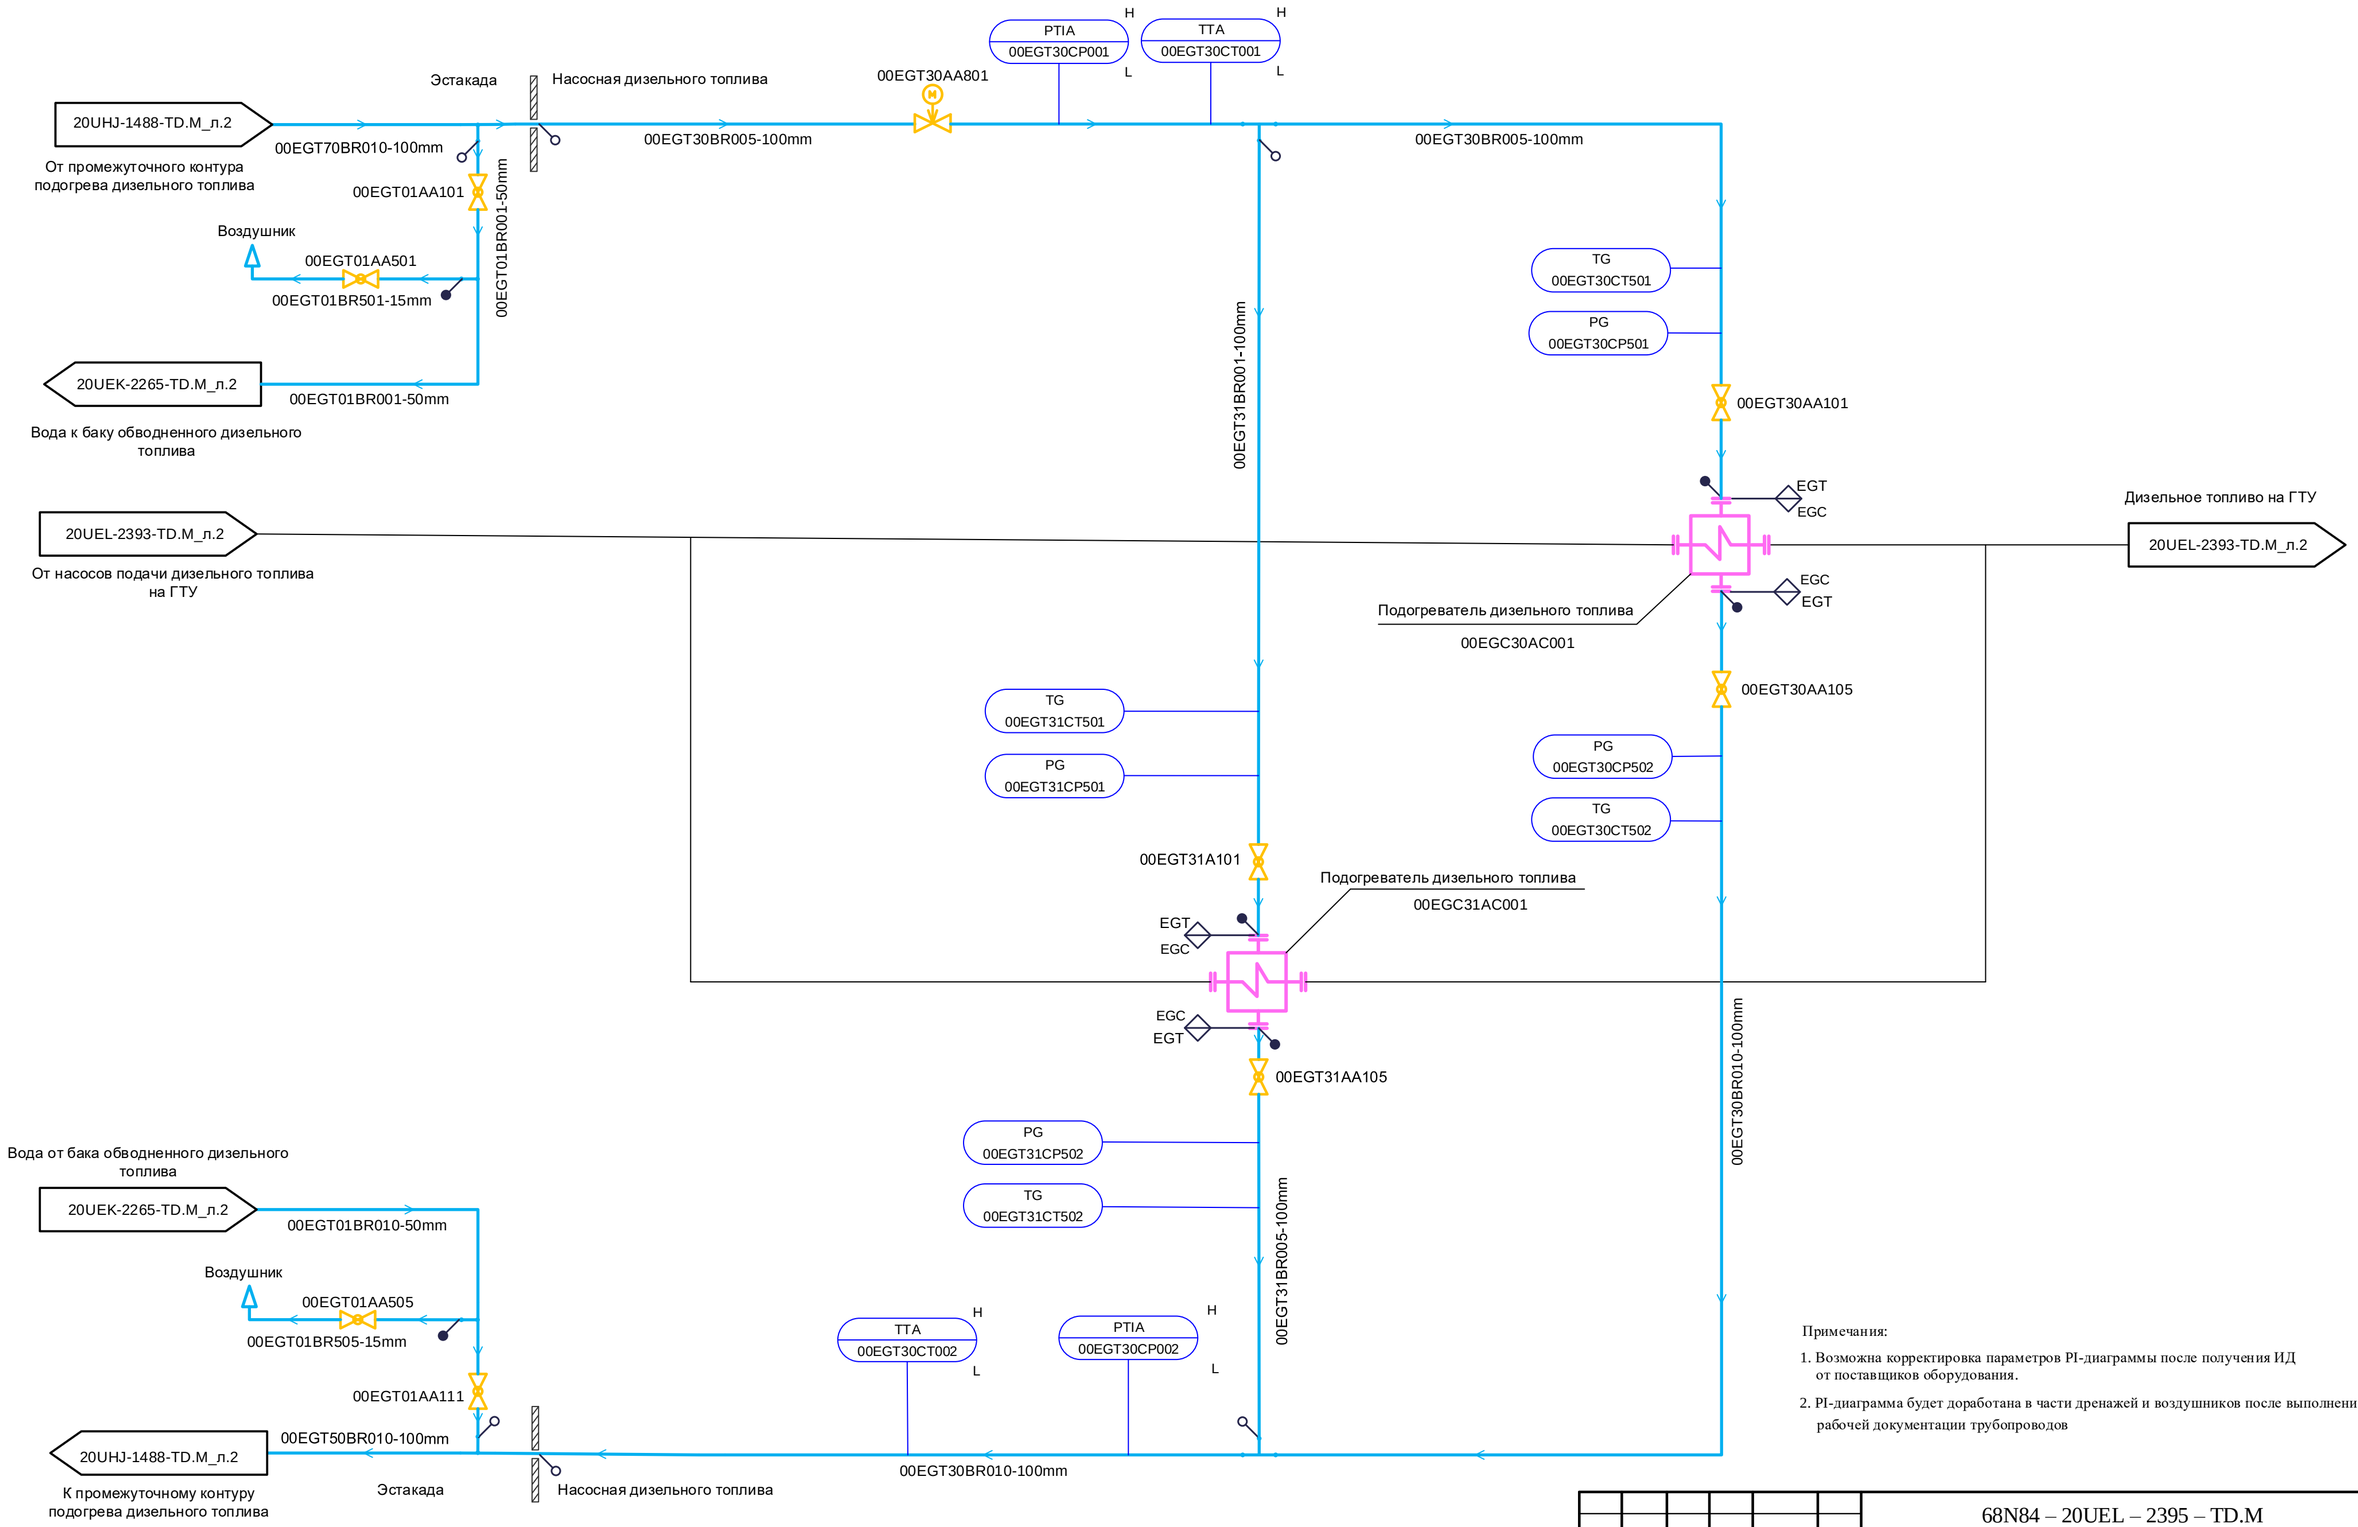

Примечания:

1. Возможна корректировка параметров PI-диаграммы после получения ИД от поставщиков оборудования.
2. PI-диаграмма будет доработана в части дренажей и воздушников после выполнения рабочей документации трубопроводов

1	-	Зам	528-22			
Изм.	Кол.уч	Лист	№ док.	Подп.	Дата	
Разработал		Полянская				
Проверил		Пак				
Н. контр.		Черемушкина				

68N84 – 20UEL – 2395 – TD.M

Строительство Якутской ГРЭС-2 (2-я очередь)

Насосная дизельного топлива. PI-диаграмма трубопроводов подогрева дизельного топлива.

Стадия	Лист	Листов
Р	2	

PI-диаграмма трубопроводов подогрева дизельного топлива. Система EGT.

АКЦИОНЕРНОЕ ОБЩЕСТВО ИНСТИТУТ ТЕПЛОЭЛЕКТРОПРОЕКТ Г. МОСКВА

Согласовано

Взам. инв. №

Подпись и дата

Инв. № подл.

Формат А2