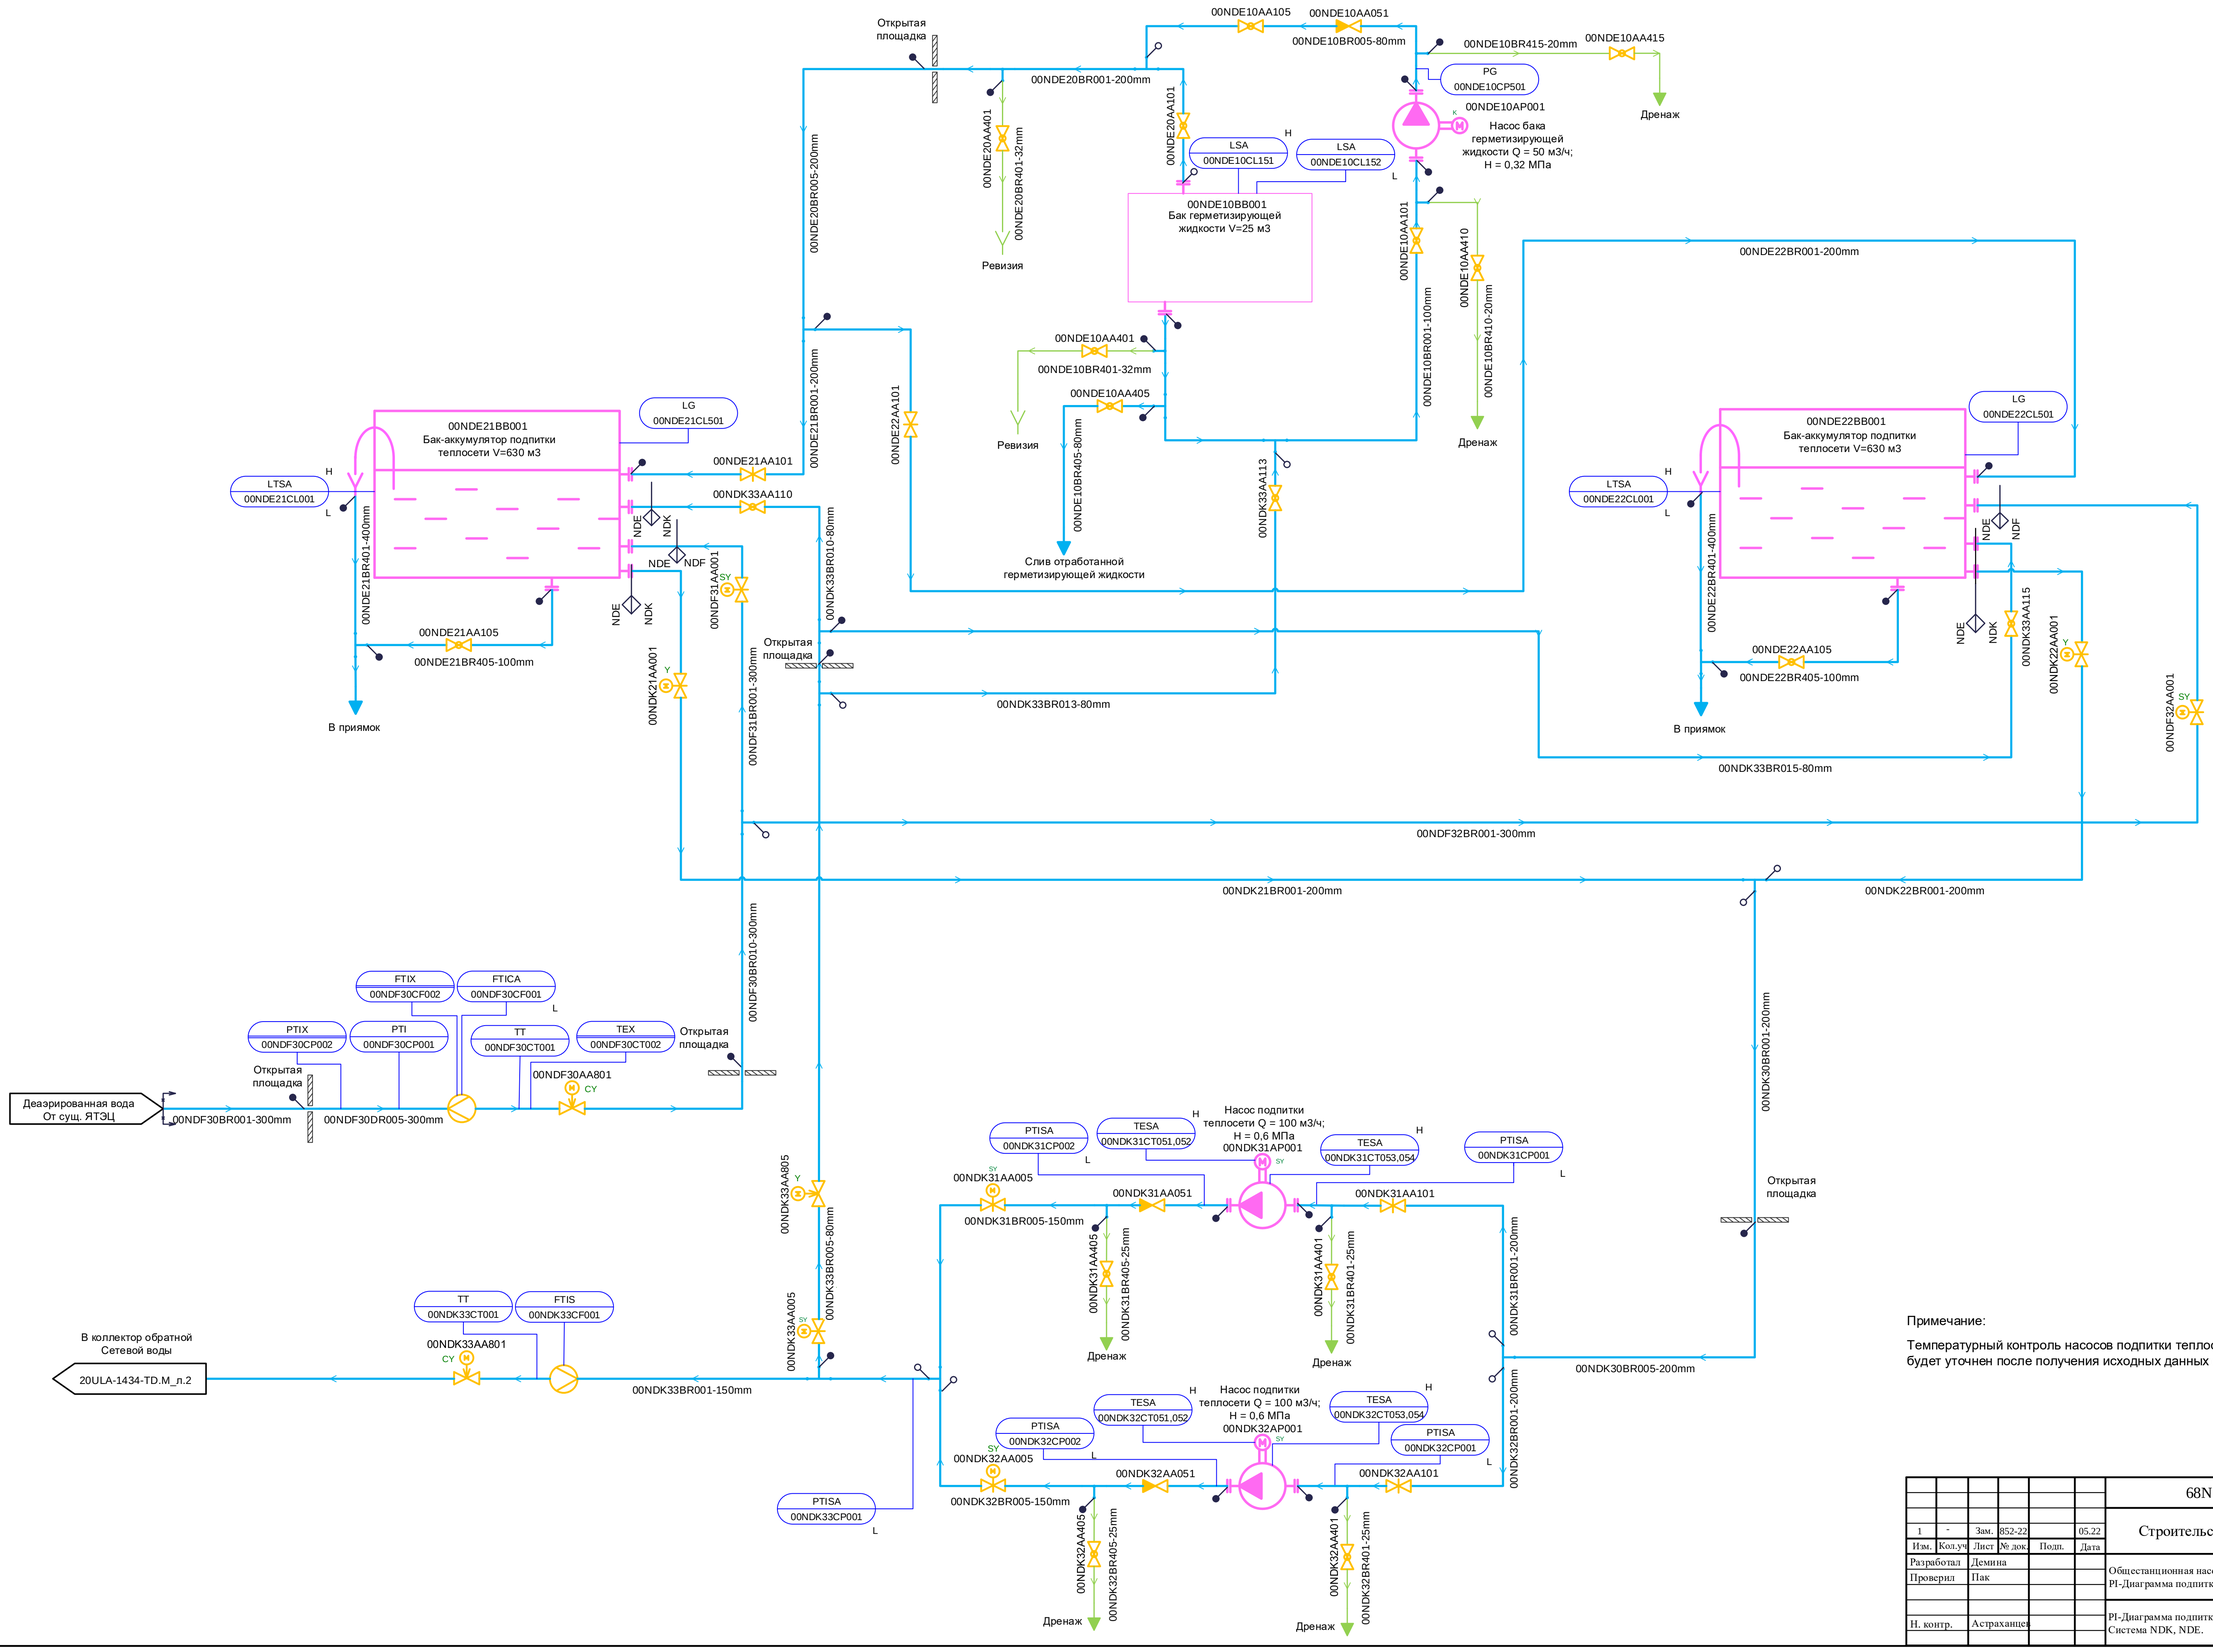

Примечание:

Температурный контроль насосов подпитки теплосети 00NDK31AP001 и 00NDK32AP001 будет уточнен после получения исходных данных от поставщика насосов.

1	-	Зам.	852-22		05.22	
Изм.	Кол.уч	Лист	№ док.	Подп.	Дата	

68N115 – 20ULA – 3701 – TD.M

Строительство Якутской ГРЭС-2 (2-я очередь)

Разработал	Демина		
Проверил	Пак		
Н. контр.	Астраханцев		

Общестанционная насосная.
PI-Диаграмма подпитки теплосети.

Стадия	Лист	Листов
Р	2	

PI-Диаграмма подпитки теплосети.
Система NDK, NDE.

АКЦИОНЕРНОЕ ОБЩЕСТВО ИНСТИТУТ ТЕПЛОЭЛЕКТРОПРОЕКТ г. МОСКВА

Согласовано

ОАСУ Кругловых

Взам. инв. №

Подпись и дата

Инв. № подл.

Формат А1