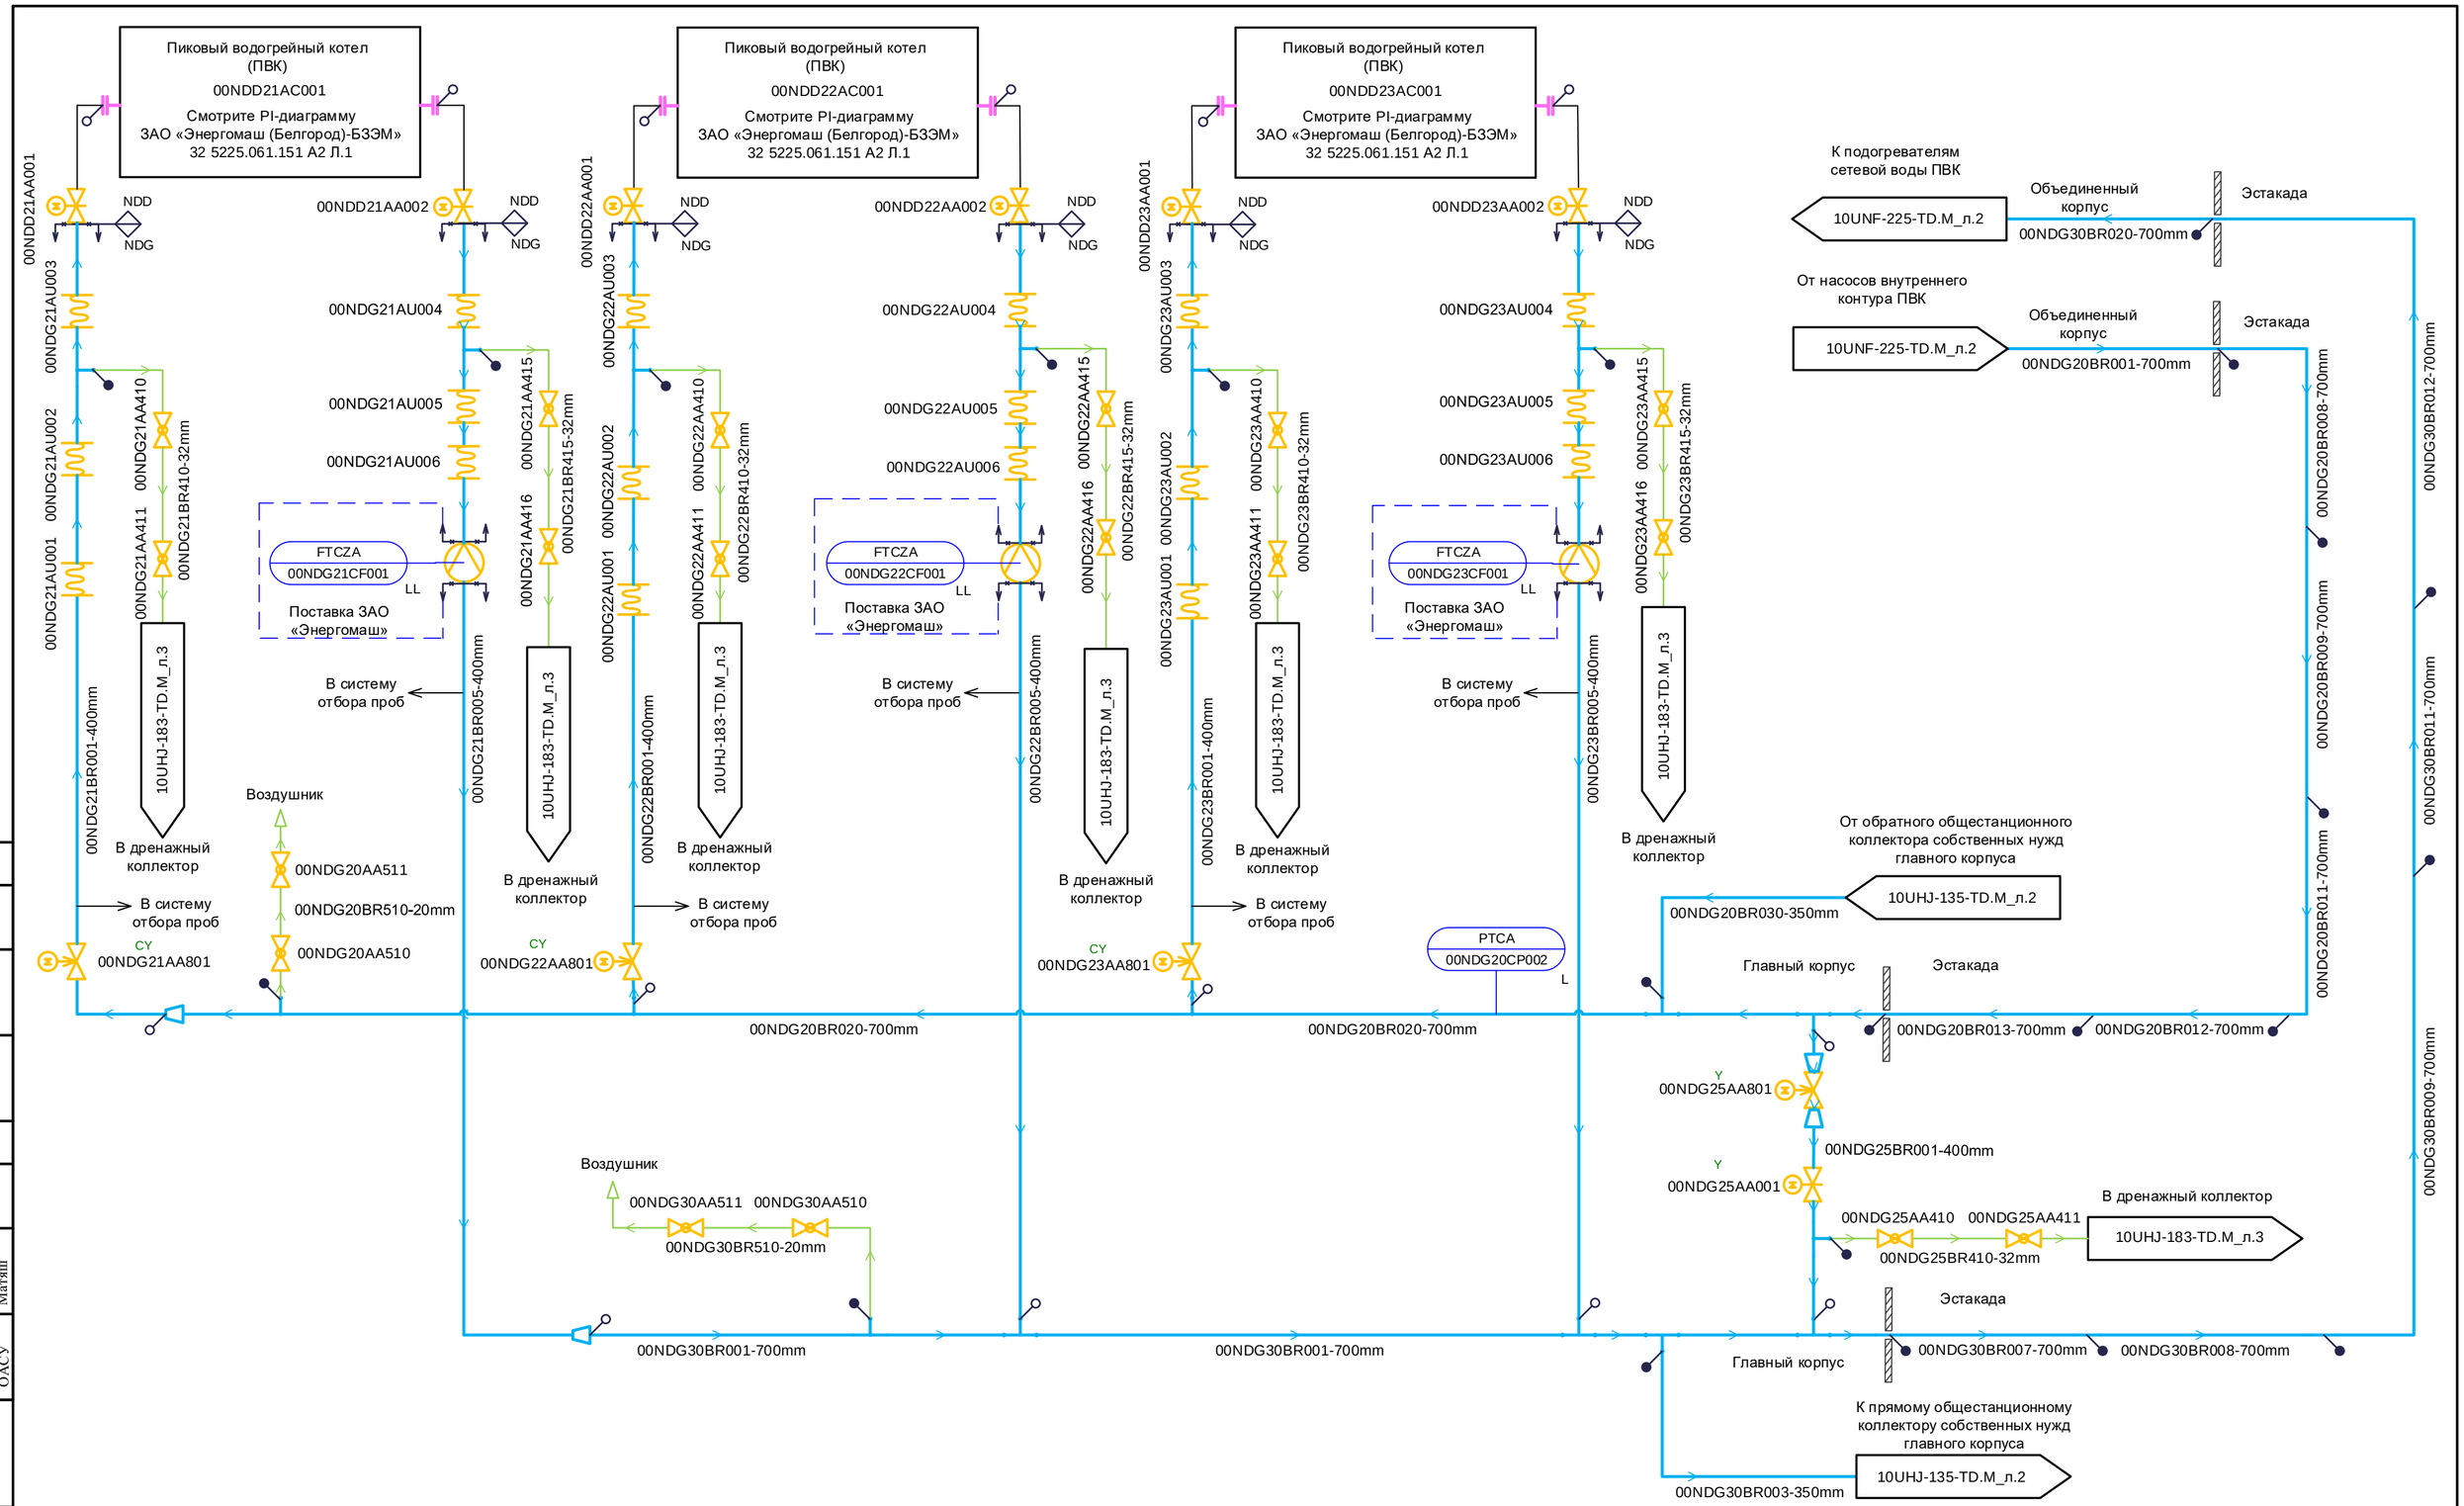

3	-	Зам.	409-15			68N1-10UHJ-101-TD.M
Изм.	Кол.уч	Лист	№ док.	Подп.	Дата	Строительство Якутской ГРЭС-2
Разработал		Калинкина				Главный корпус. PI-диаграмма трубопроводов воды внутреннего контура ПВК
Проверил		Бобров				Стадия: Р; Лист: 2; Листов:
Гл. спец.		Стацура				
Н. контр.		Астраханцев				PI-диаграмма трубопроводов воды внутреннего контура ПВК. Система NDC, NDD, NDG

АКЦИОНЕРНОЕ ОБЩЕСТВО ИНСТИТУТ ТЕПЛОЭЛЕКТРОПРОЕКТ Г. МОСКВА

Согласовано

ОАСУ Матяш

Взам. инв. №

Подпись и дата

Инв. № подл.

Формат А2