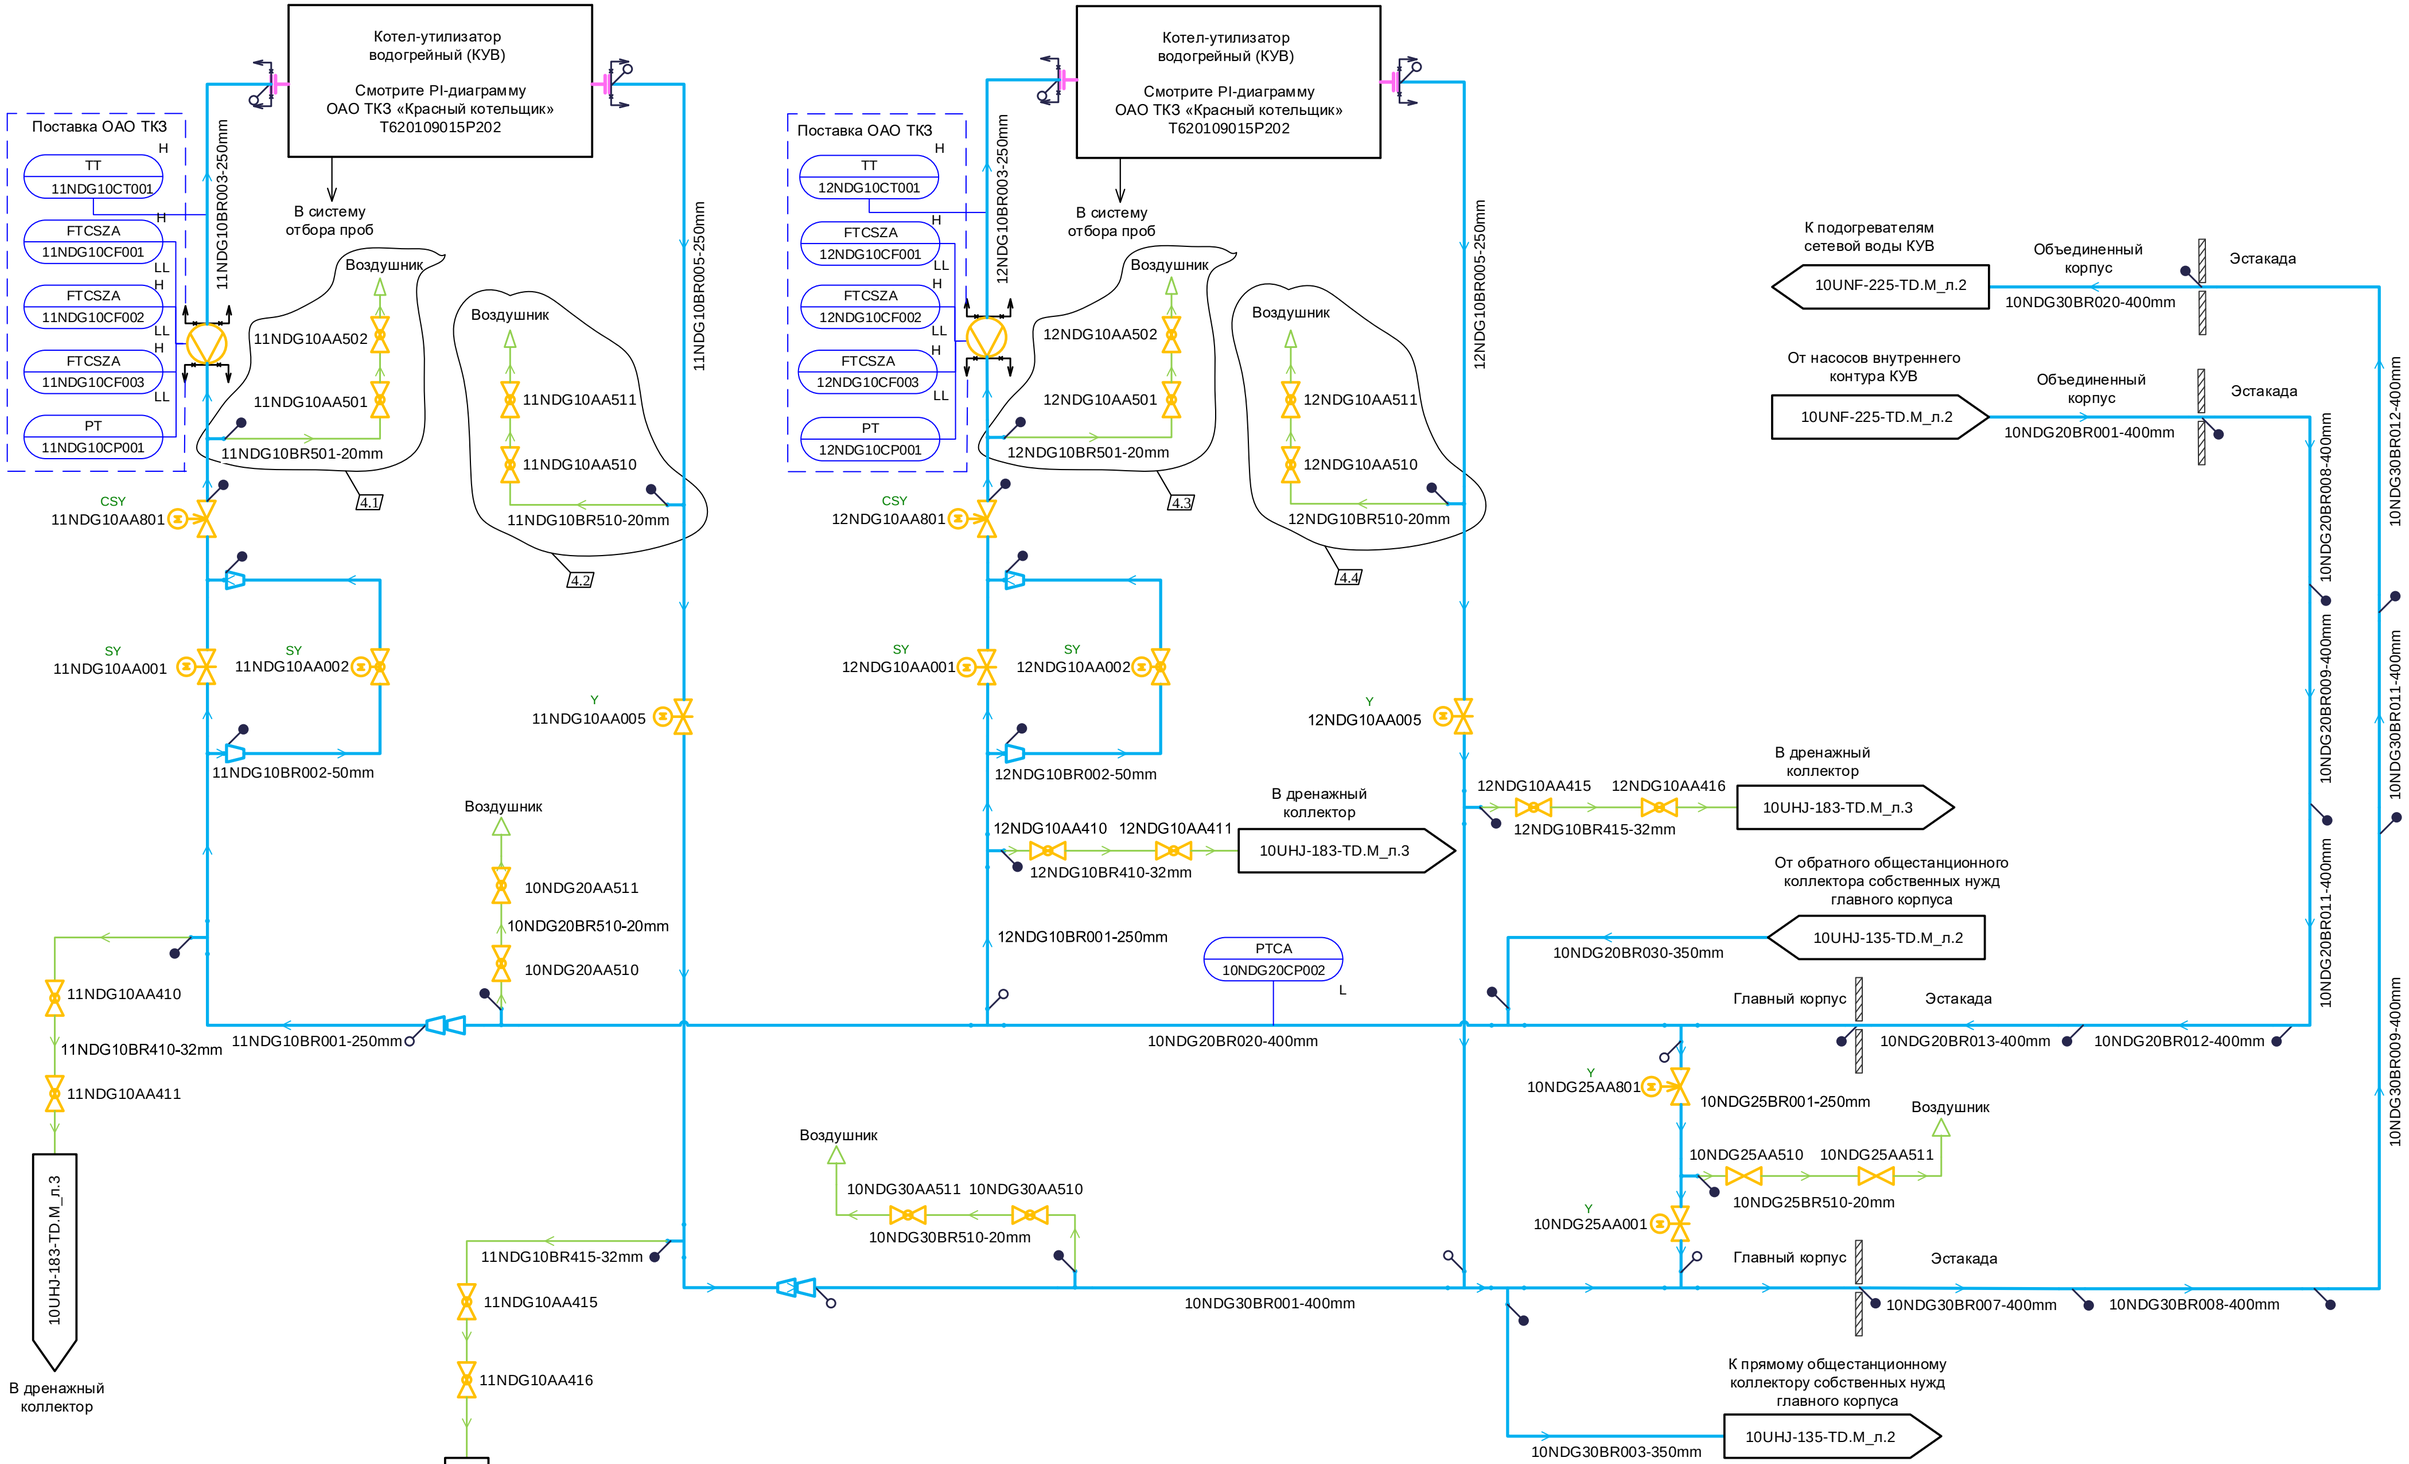

4	4	Зам.	844-16			
Изм.	Кол.уч	Лист	№ док.	Подп.	Дата	
Разработал		Калинкина				
Проверил		Бобров				
Гл. спец.		Стацура				
Н. контр.		Астраханцев				

68N1 – 10UHJ – 108 – TD.M

Строительство Якутской ГРЭС-2

Главный корпус. PI-диаграмма трубопроводов воды внутреннего контура КУВ энергоблока №1

Стадия	Лист	Листов
Р	2	

PI-диаграмма трубопроводов воды внутреннего контура КУВ энергоблока №1. Система NDG

АКЦИОНЕРНОЕ ОБЩЕСТВО ИНСТИТУТ ТЕПЛОЭЛЕКТРОПРОЕКТ Г. МОСКВА

Согласовано

ОАСУ Морозова

Взам. инв. №

Подпись и дата

Инв. № подл.

Формат А2