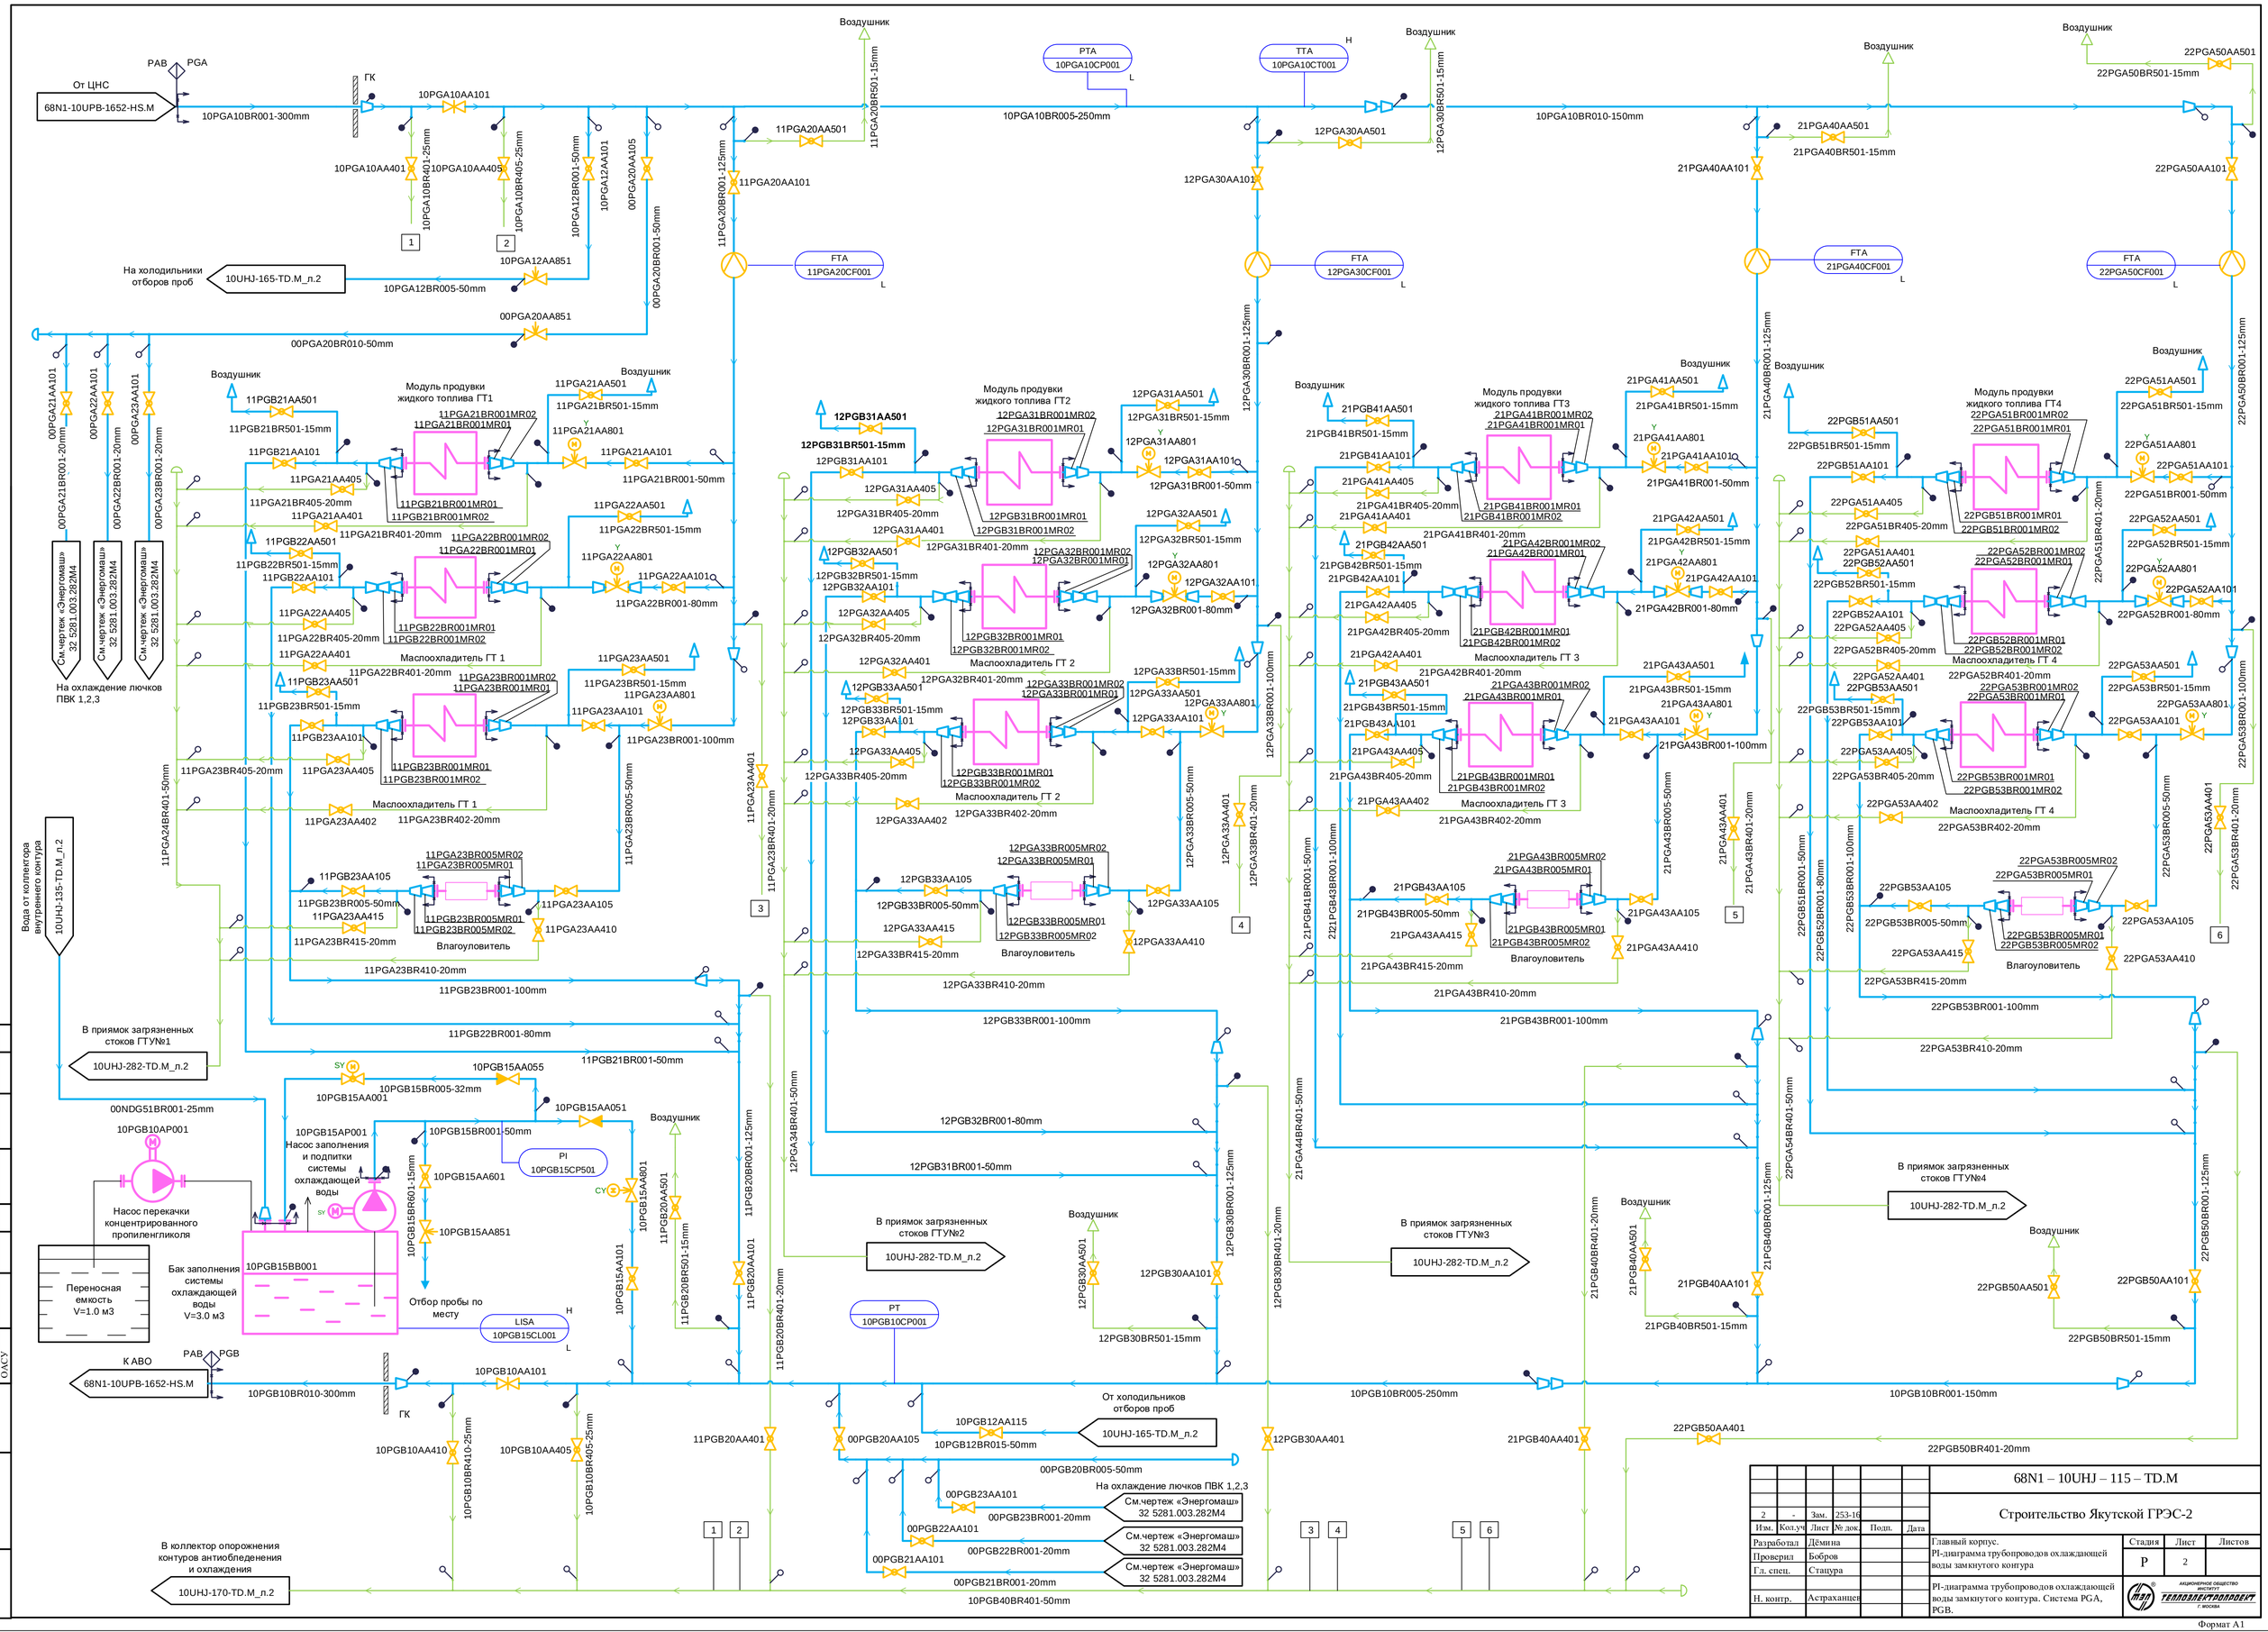

						68N1 – 10UHJ – 115 – TD.M			
2	-	Зам.	253-16			Строительство Якутской ГРЭС-2			
Изм.	Кол.уч	Лист	№ док.	Подп.	Дата				
Разработал		Дёмина				Главный корпус. PI-диаграмма трубопроводов охлаждающей воды замкнутого контура	Стадия	Лист	Листов
Проверил		Бобров					Р	2	
Гл. спец.		Стацура							
Н. контр.		Астраханцев				PI-диаграмма трубопроводов охлаждающей воды замкнутого контура. Система PGA, PGB.	АКЦИОНЕРНОЕ ОБЩЕСТВО ТЕПЛОЭЛЕКТРОПРОЕКТ г. МОСКВА		

Согласовано

ОТС

ОАСУ

Взам. инв. №

Подпись и дата

Инв. № подл.

Формат А1