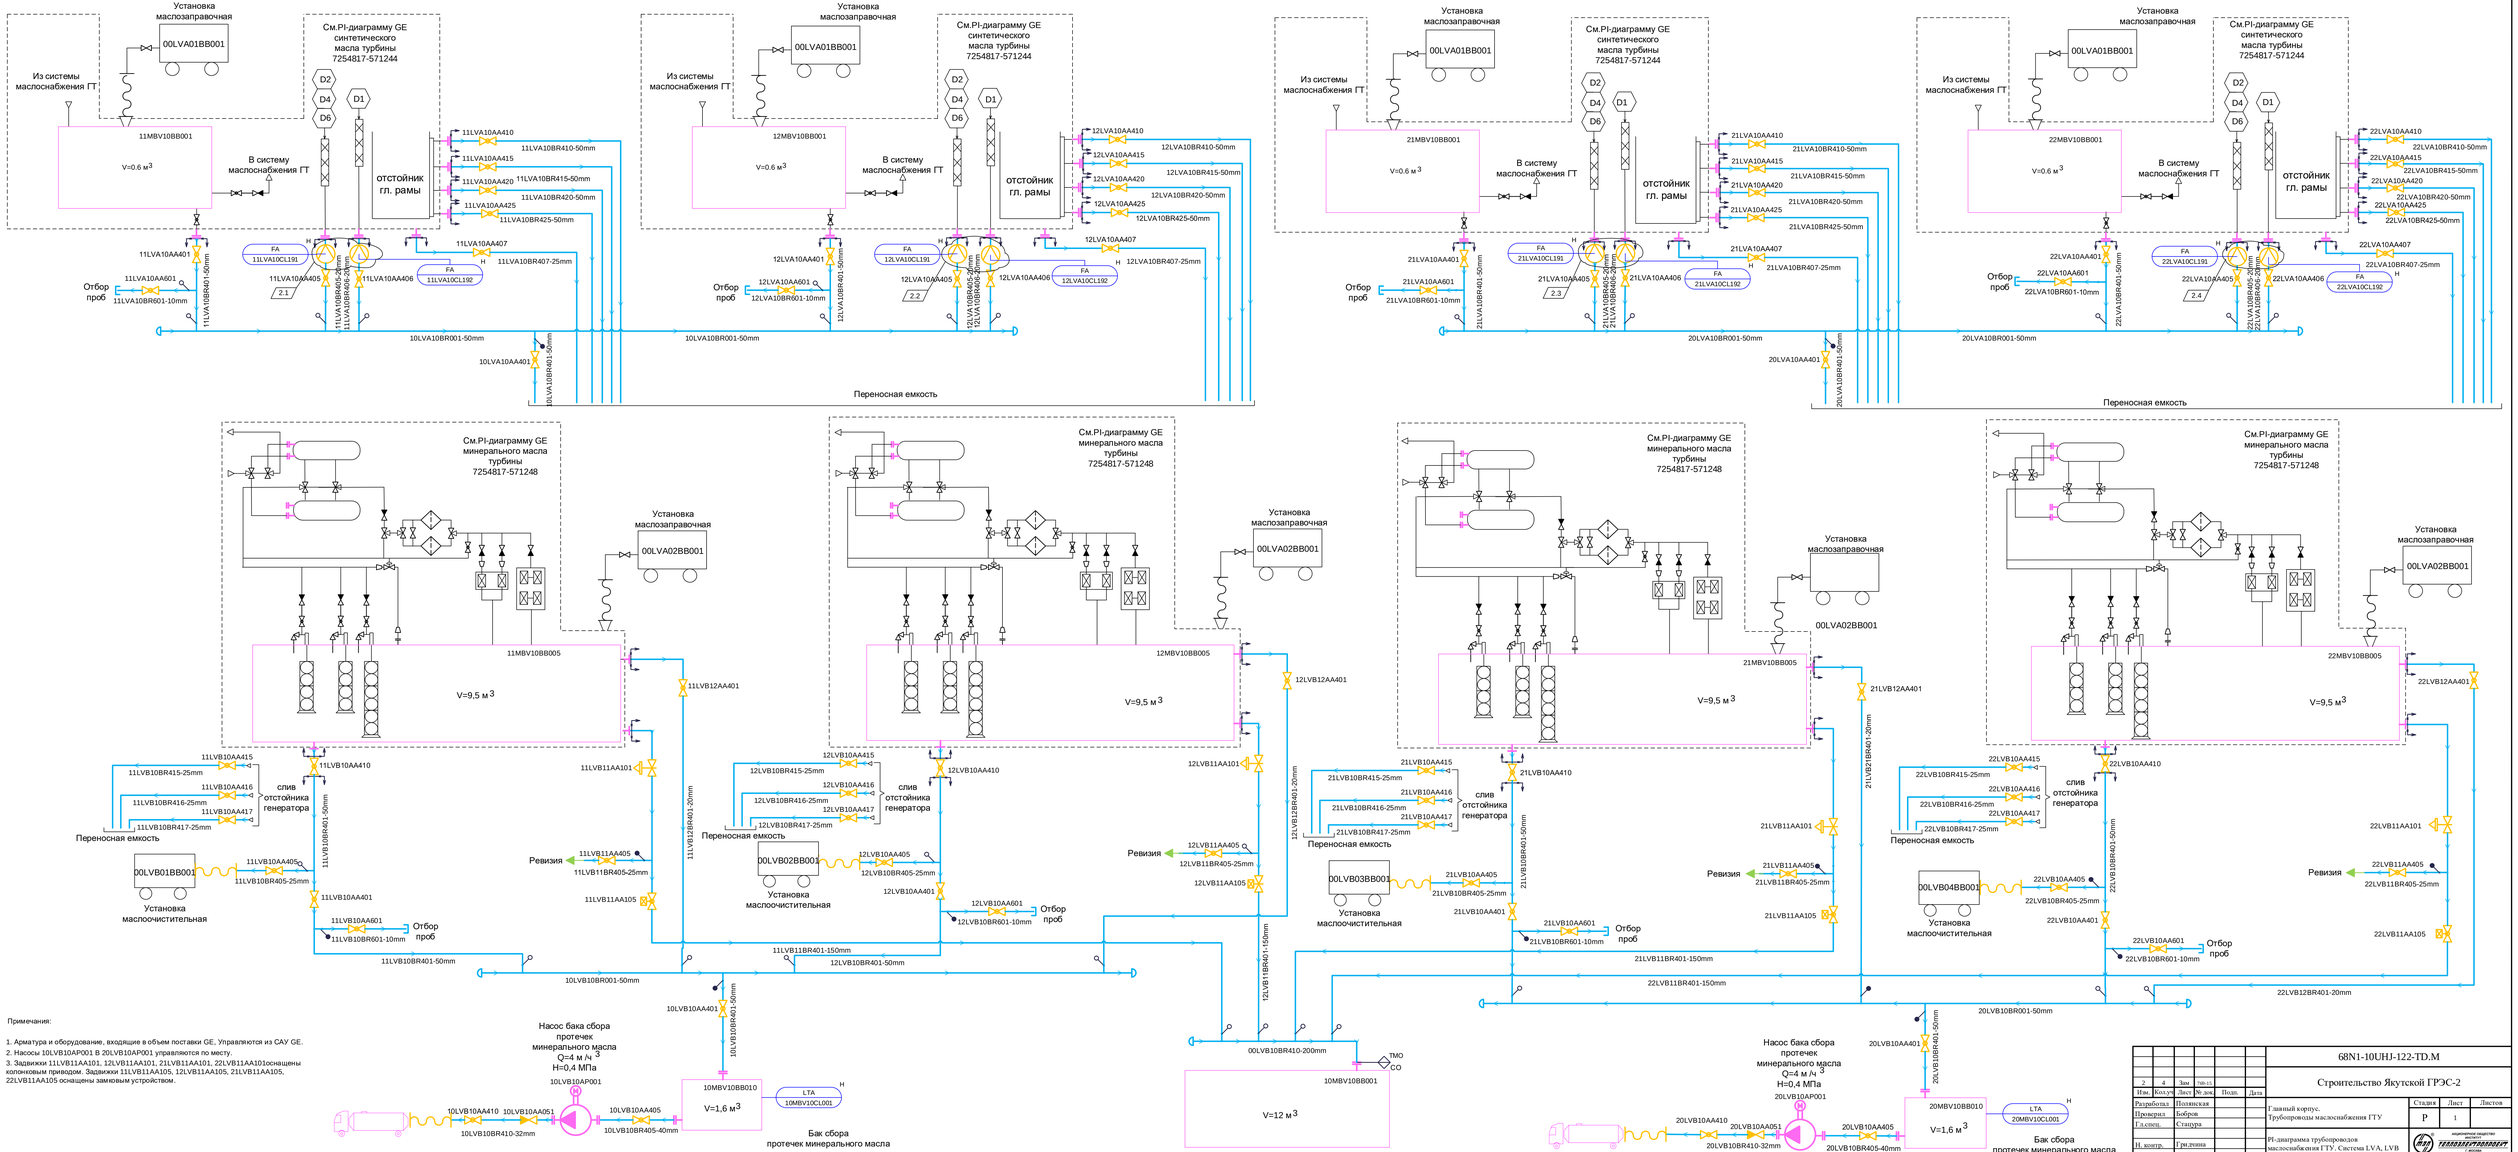

Примечания:

1. Арматура и оборудование, входящие в объем поставки GE, Управляются из САУ GE.
2. Насосы 10LVB10AP001 В 20LVB10AP001 управляются по месту.
3. Задвижки 11LVB11AA101, 12LVB11AA101, 21LVB11AA101, 22LVB11AA101оснащены колонковым приводом. Задвижки 11LVB11AA105, 12LVB11AA105, 21LVB11AA105, 22LVB11AA105 оснащены замковым устройством.

2	4	Зам	Лист-15			68N1-10UHJ-122-TD.M	
Изм.	Кол.уч.	Лист	№ док.	Подп.	Дата	Строительство Якутской ГРЭС-2	
Разработал		Полянская				Главный корпус. Трубопроводы маслоснабжения ГТУ	Стадия: Р; Лист: 1; Листов:
Проверил		Бобров					
Гл.спец.		Стацура					
Н. контр.		Гриднева				PI-диаграмма трубопроводов маслоснабжения ГТУ. Система LVA, LVB	АКЦИОНЕРНОЕ ОБЩЕСТВО ТЕХНИЧЕСКОЕ ОБЪЕДИНЕНИЕ ТЕХЭНЕРГОСЕРВИС

Согласовано

Взам. инв. №

Подпись и дата

Инв. № подл.

Формат А2х3