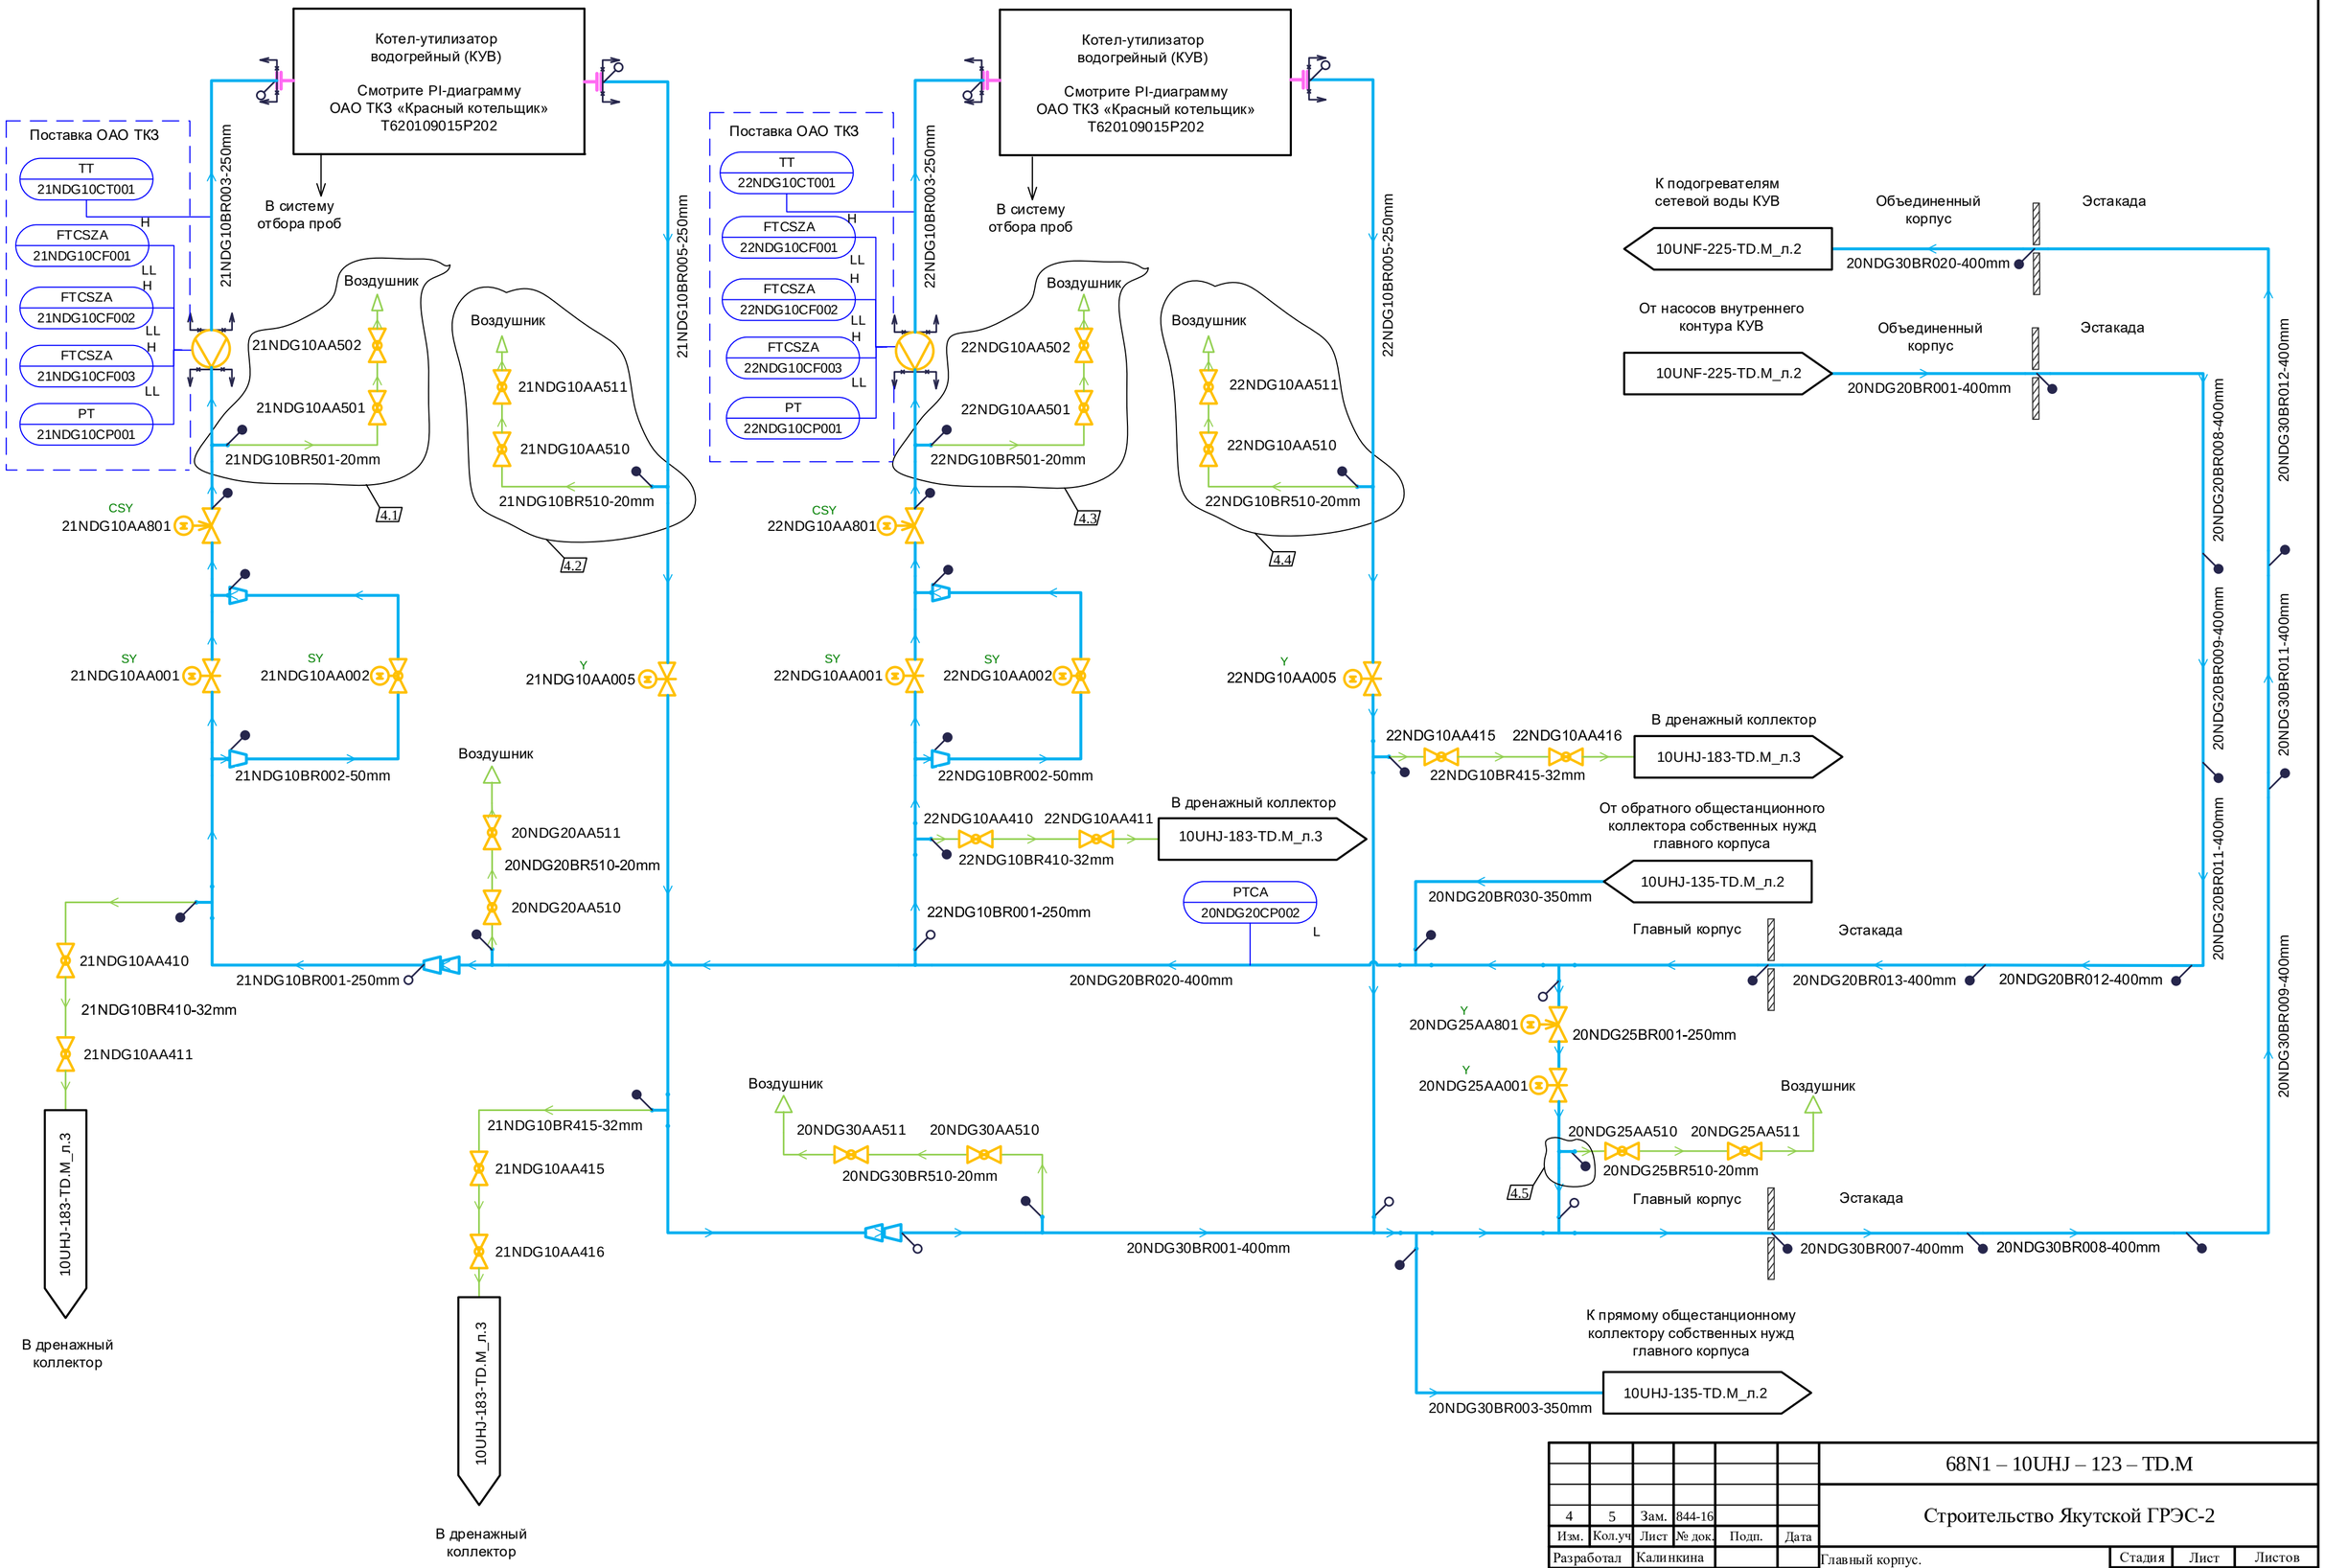

4	5	Зам.	844-16			68N1 – 10UHJ – 123 – TD.M
Изм.	Кол.уч	Лист	№ док.	Подп.	Дата	Строительство Якутской ГРЭС-2
Разработал		Калинкина				Главный корпус. PI-диаграмма трубопроводов воды внутреннего контура КУВ энергоблока №2
Проверил		Бобров				Стадия: Р; Лист: 2; Листов:
Гл. спец.		Стацура				
Н. контр.		Астраханцев				PI-диаграмма трубопроводов воды внутреннего контура КУВ энергоблока №2. Система NDG

АКЦИОНЕРНОЕ ОБЩЕСТВО ИНСТИТУТ ТЕПЛОЭЛЕКТРОПРОЕКТ г. МОСКВА

ОАСУ Морозова

Формат А2