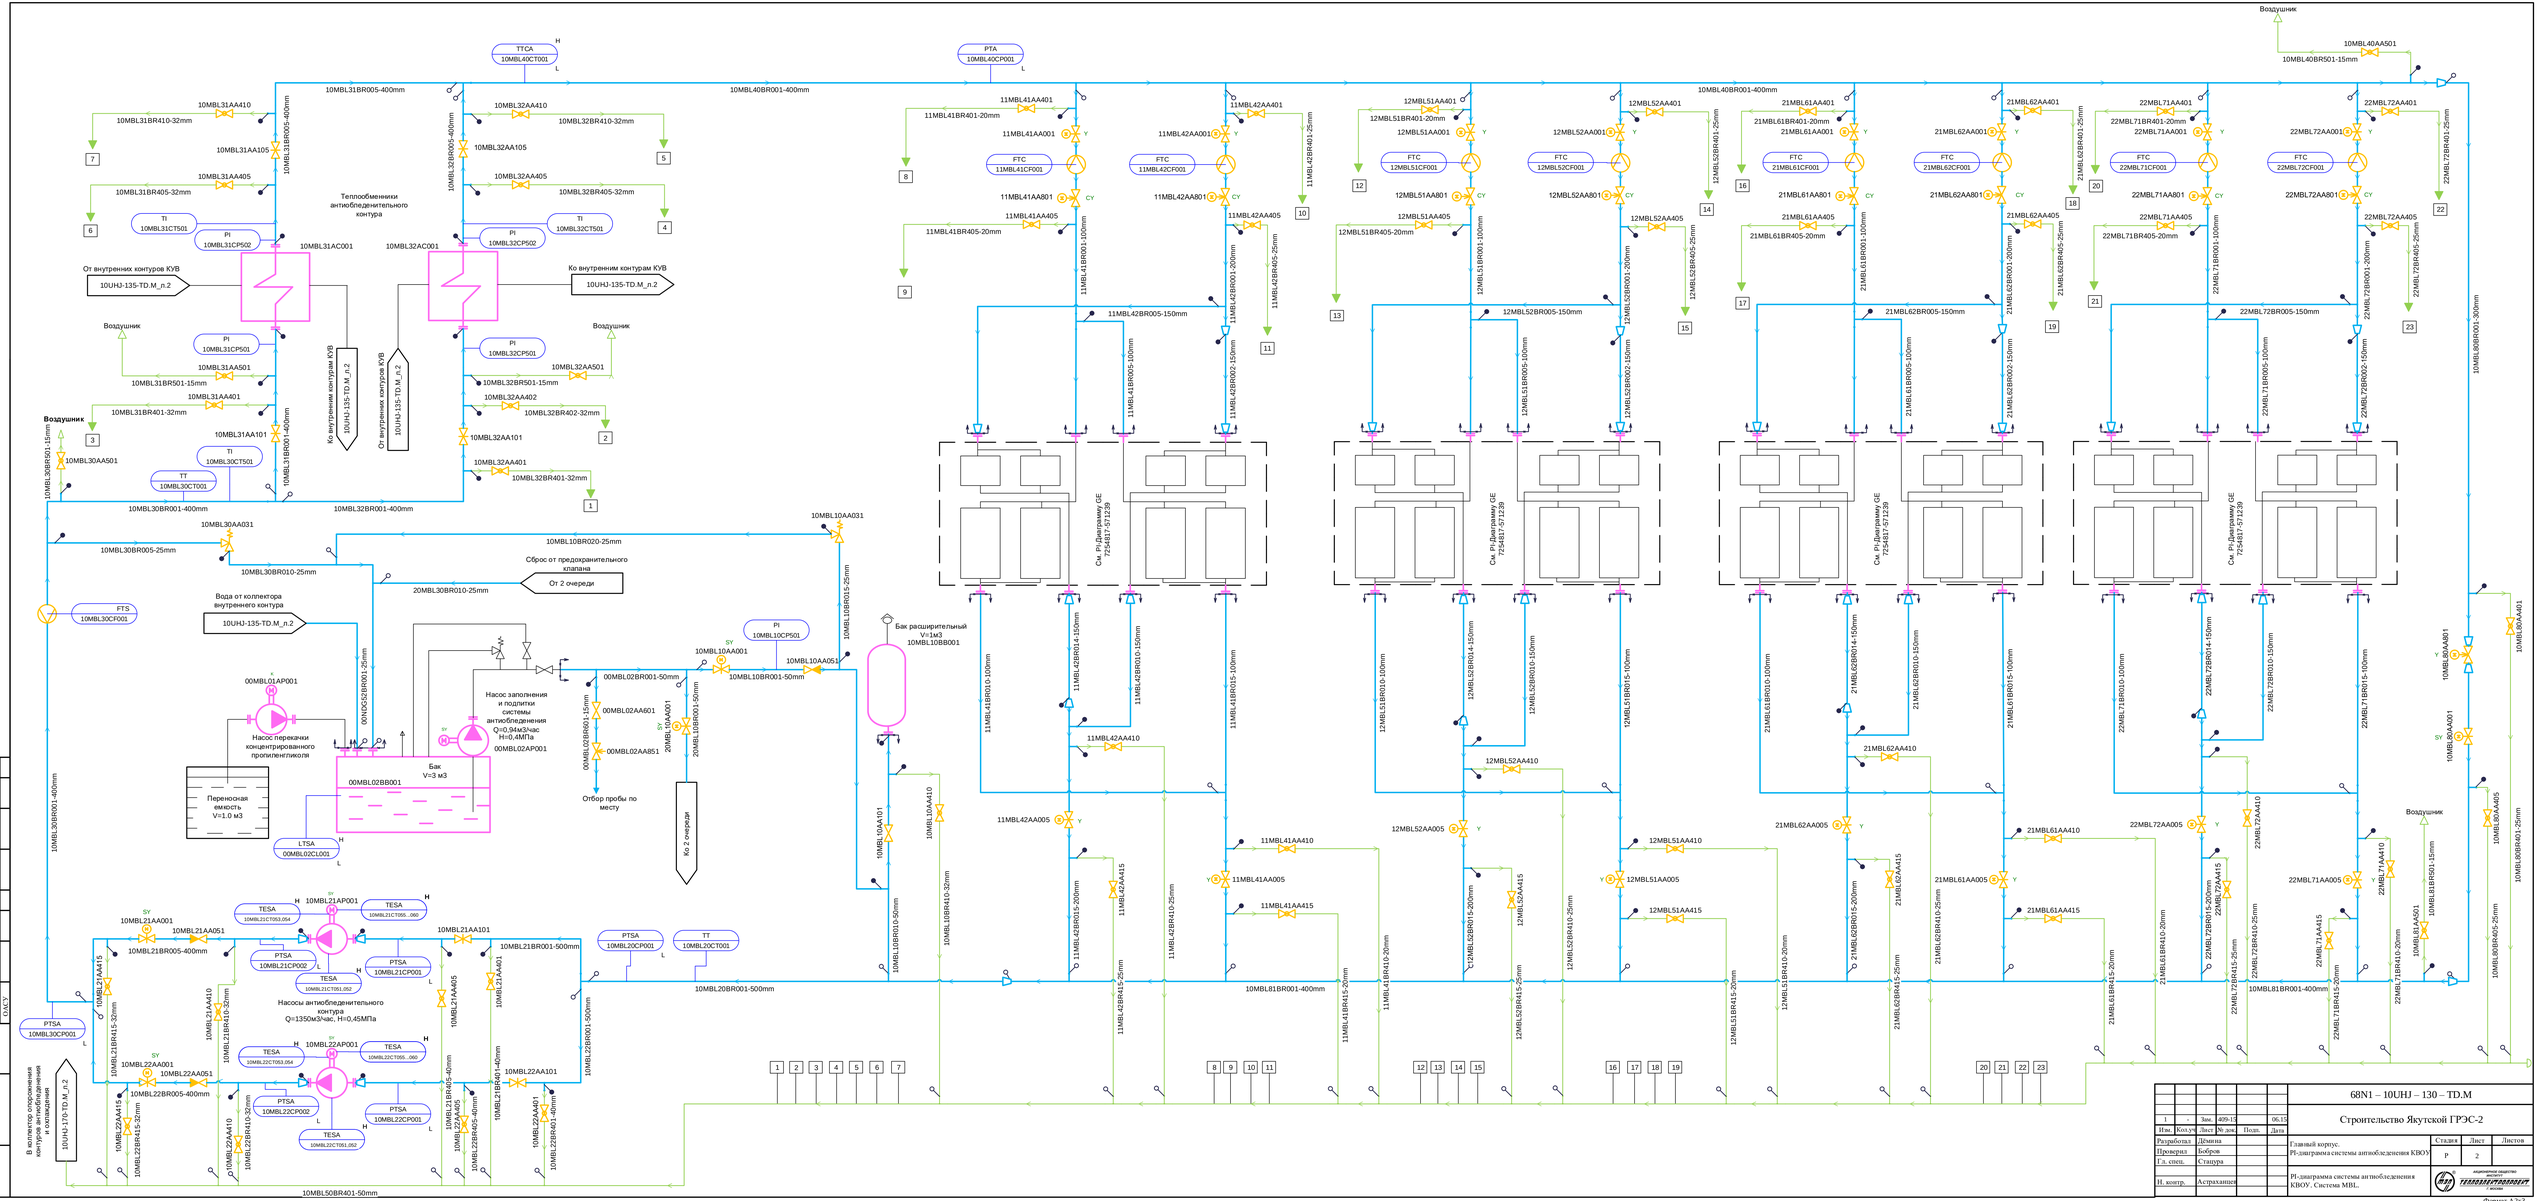
Теплообменники антиобледенительного контура
10MBL31AC001
10MBL32AC001
От внутренних контуров КУВ
10UHJ-135-TD.M_n.2
Ко внутренним контурам КУВ
10UHJ-135-TD.M_n.2
Воздушник
Насос перекачки концентрированного пропиленгликоля
00MBL01AP001
Переносная емкость V=1.0 м3
Насос заполнения и подпитки системы антиобледенения Q=0,94м3/час H=0,4МПа
00MBL02AP001
Бак V=3 м3
00MBL02BB001
Вода от коллектора внутреннего контура
Сброс от предохранительного клапана
От 2 очереди
Ко 2 очереди
Отбор пробы по месту
Бак расширительный V=1м3
10MBL10BB001
Насосы антиобледенительного контура Q=1350м3/час, H=0,45МПа
10MBL21AP001
10MBL22AP001
В коллектор опорожнения контуров обогревания и охлаждения
10UHJ-170-TD.M_n.2
См. PI-Диаграмму GE 7254817-571239
См. PI-Диаграмму GE 7254817-571238
68N1 – 10UHJ – 130 – TD.M
Строительство Якутской ГРЭС-2
Главный корпус.
PI-диаграмма системы антиобледенения КВОУ
PI-диаграмма системы антиобледенения КВОУ. Система MBL.
Разработал Демина
Проверил Бобров
Гл. спец. Стацура
Н. контр. Астраханцев
Стадия Р
Лист 2
Листов
Изм. Кол.уч. Лист № док. Подп. Дата
1 - Зам. 409-13 06.15
Согласовано
ПАСУ
Взам. инв. №
Подпись и дата
Инв. № подл.
Формат А2х3