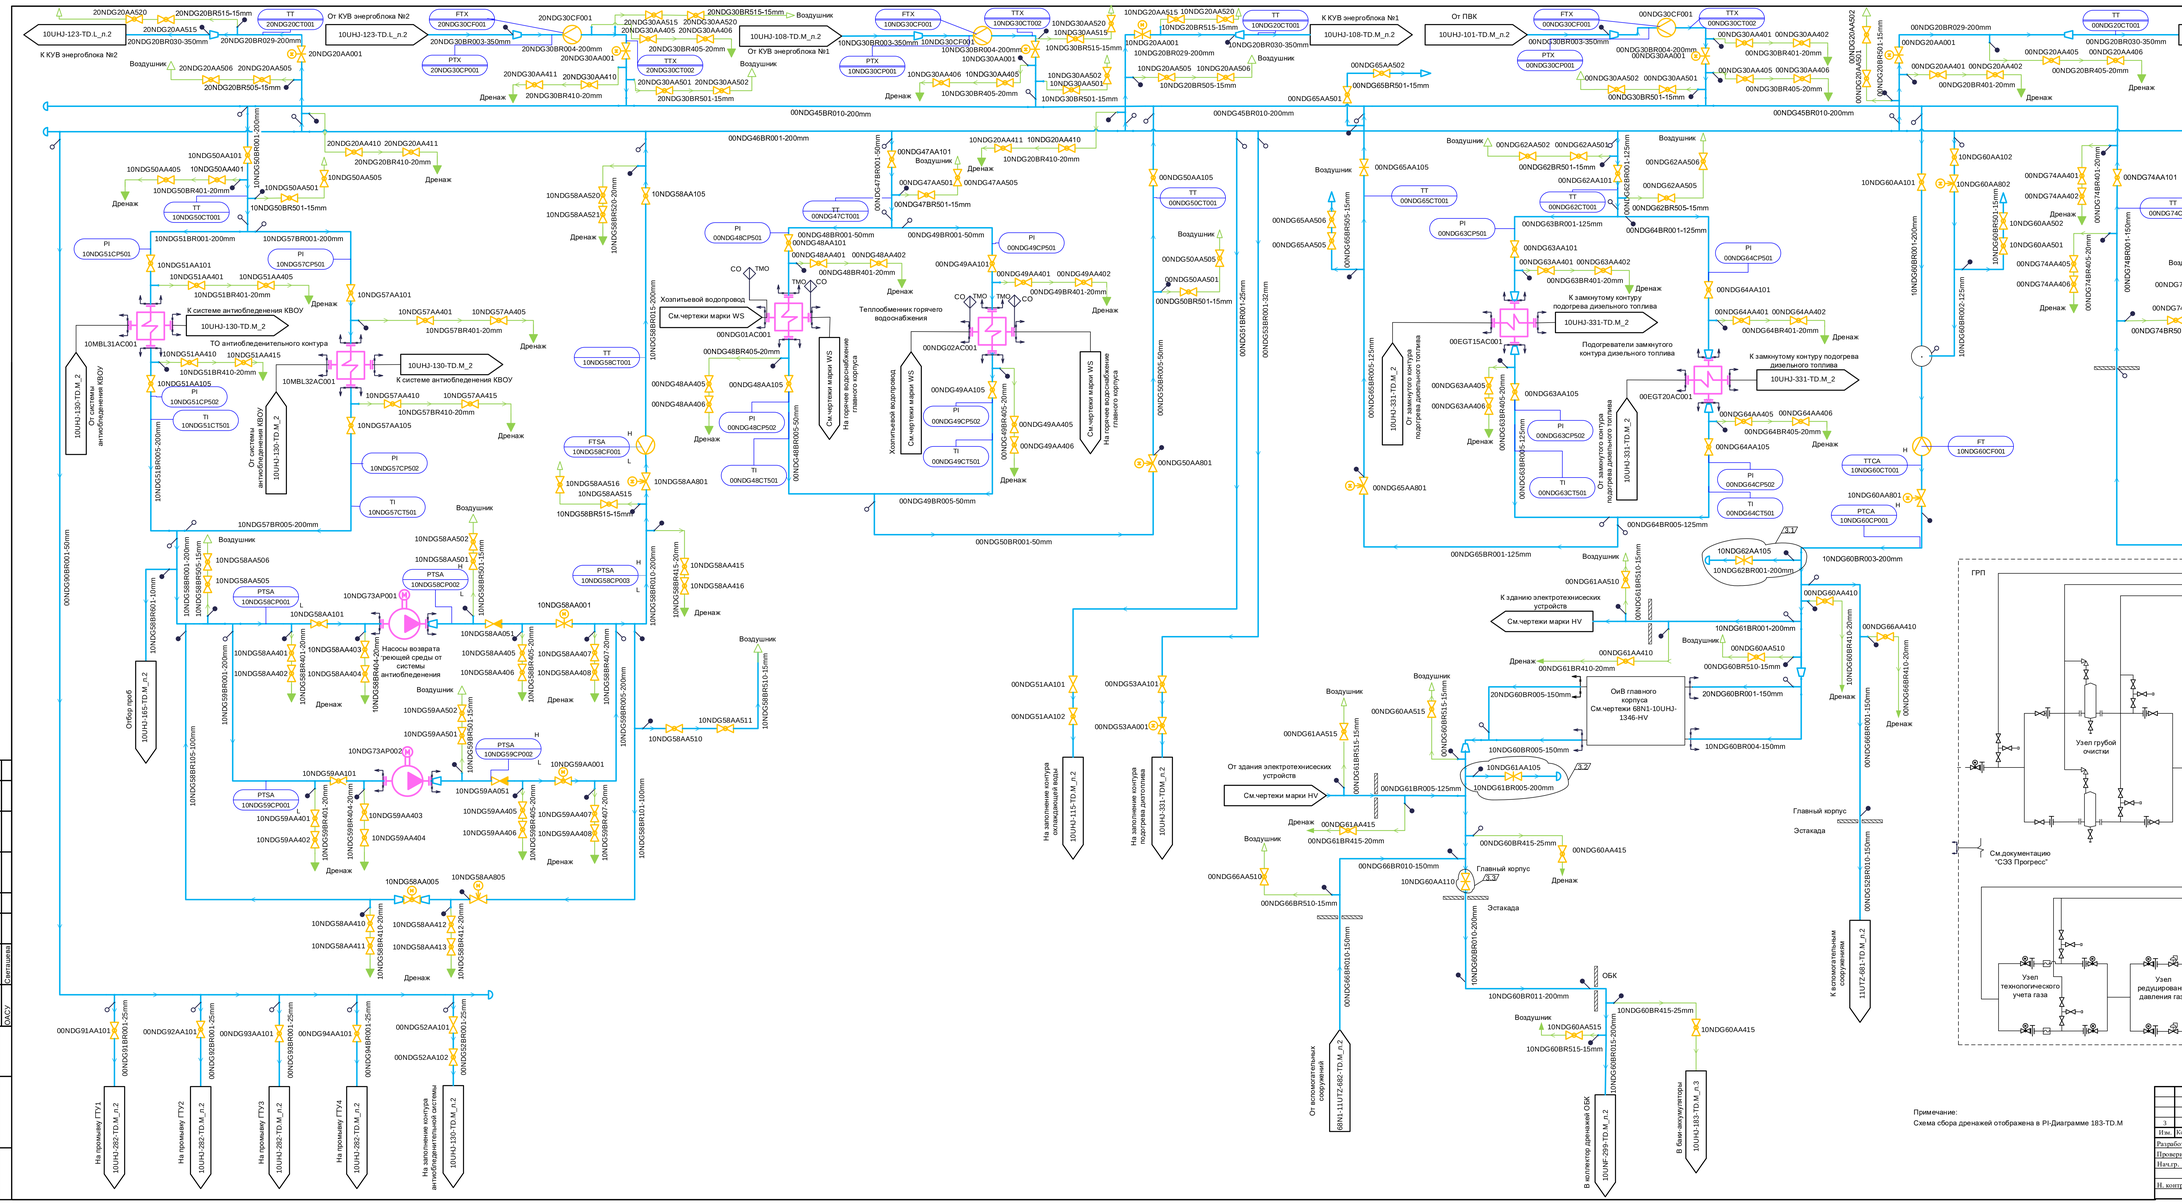

						68N1-10UHJ-135-TD.M	
						Строительство Якутской ГРЭС-2	
Изм.	Кол.уч.	Лист	№ док.	Подп.	Дата		
Разработал		Полянская				Главный корпус. Pi-диаграмма трубопроводов сетевой воды к потребителям собственных нужд	Стадия: Р; Лист: 2; Листов:
Проверил		Бобров					
Нач.пр.		Стадуха				Pi-диаграмма трубопроводов сетевой воды к потребителям собственных нужд	
Н. контр.		Грицина					Акционерное общество ТЕХЭКСПРОМ

Согласовано
Взам. инв. №
Подпись и дата
Инв. № подл.
Светлицкая
КИСУ

Формат А2х3