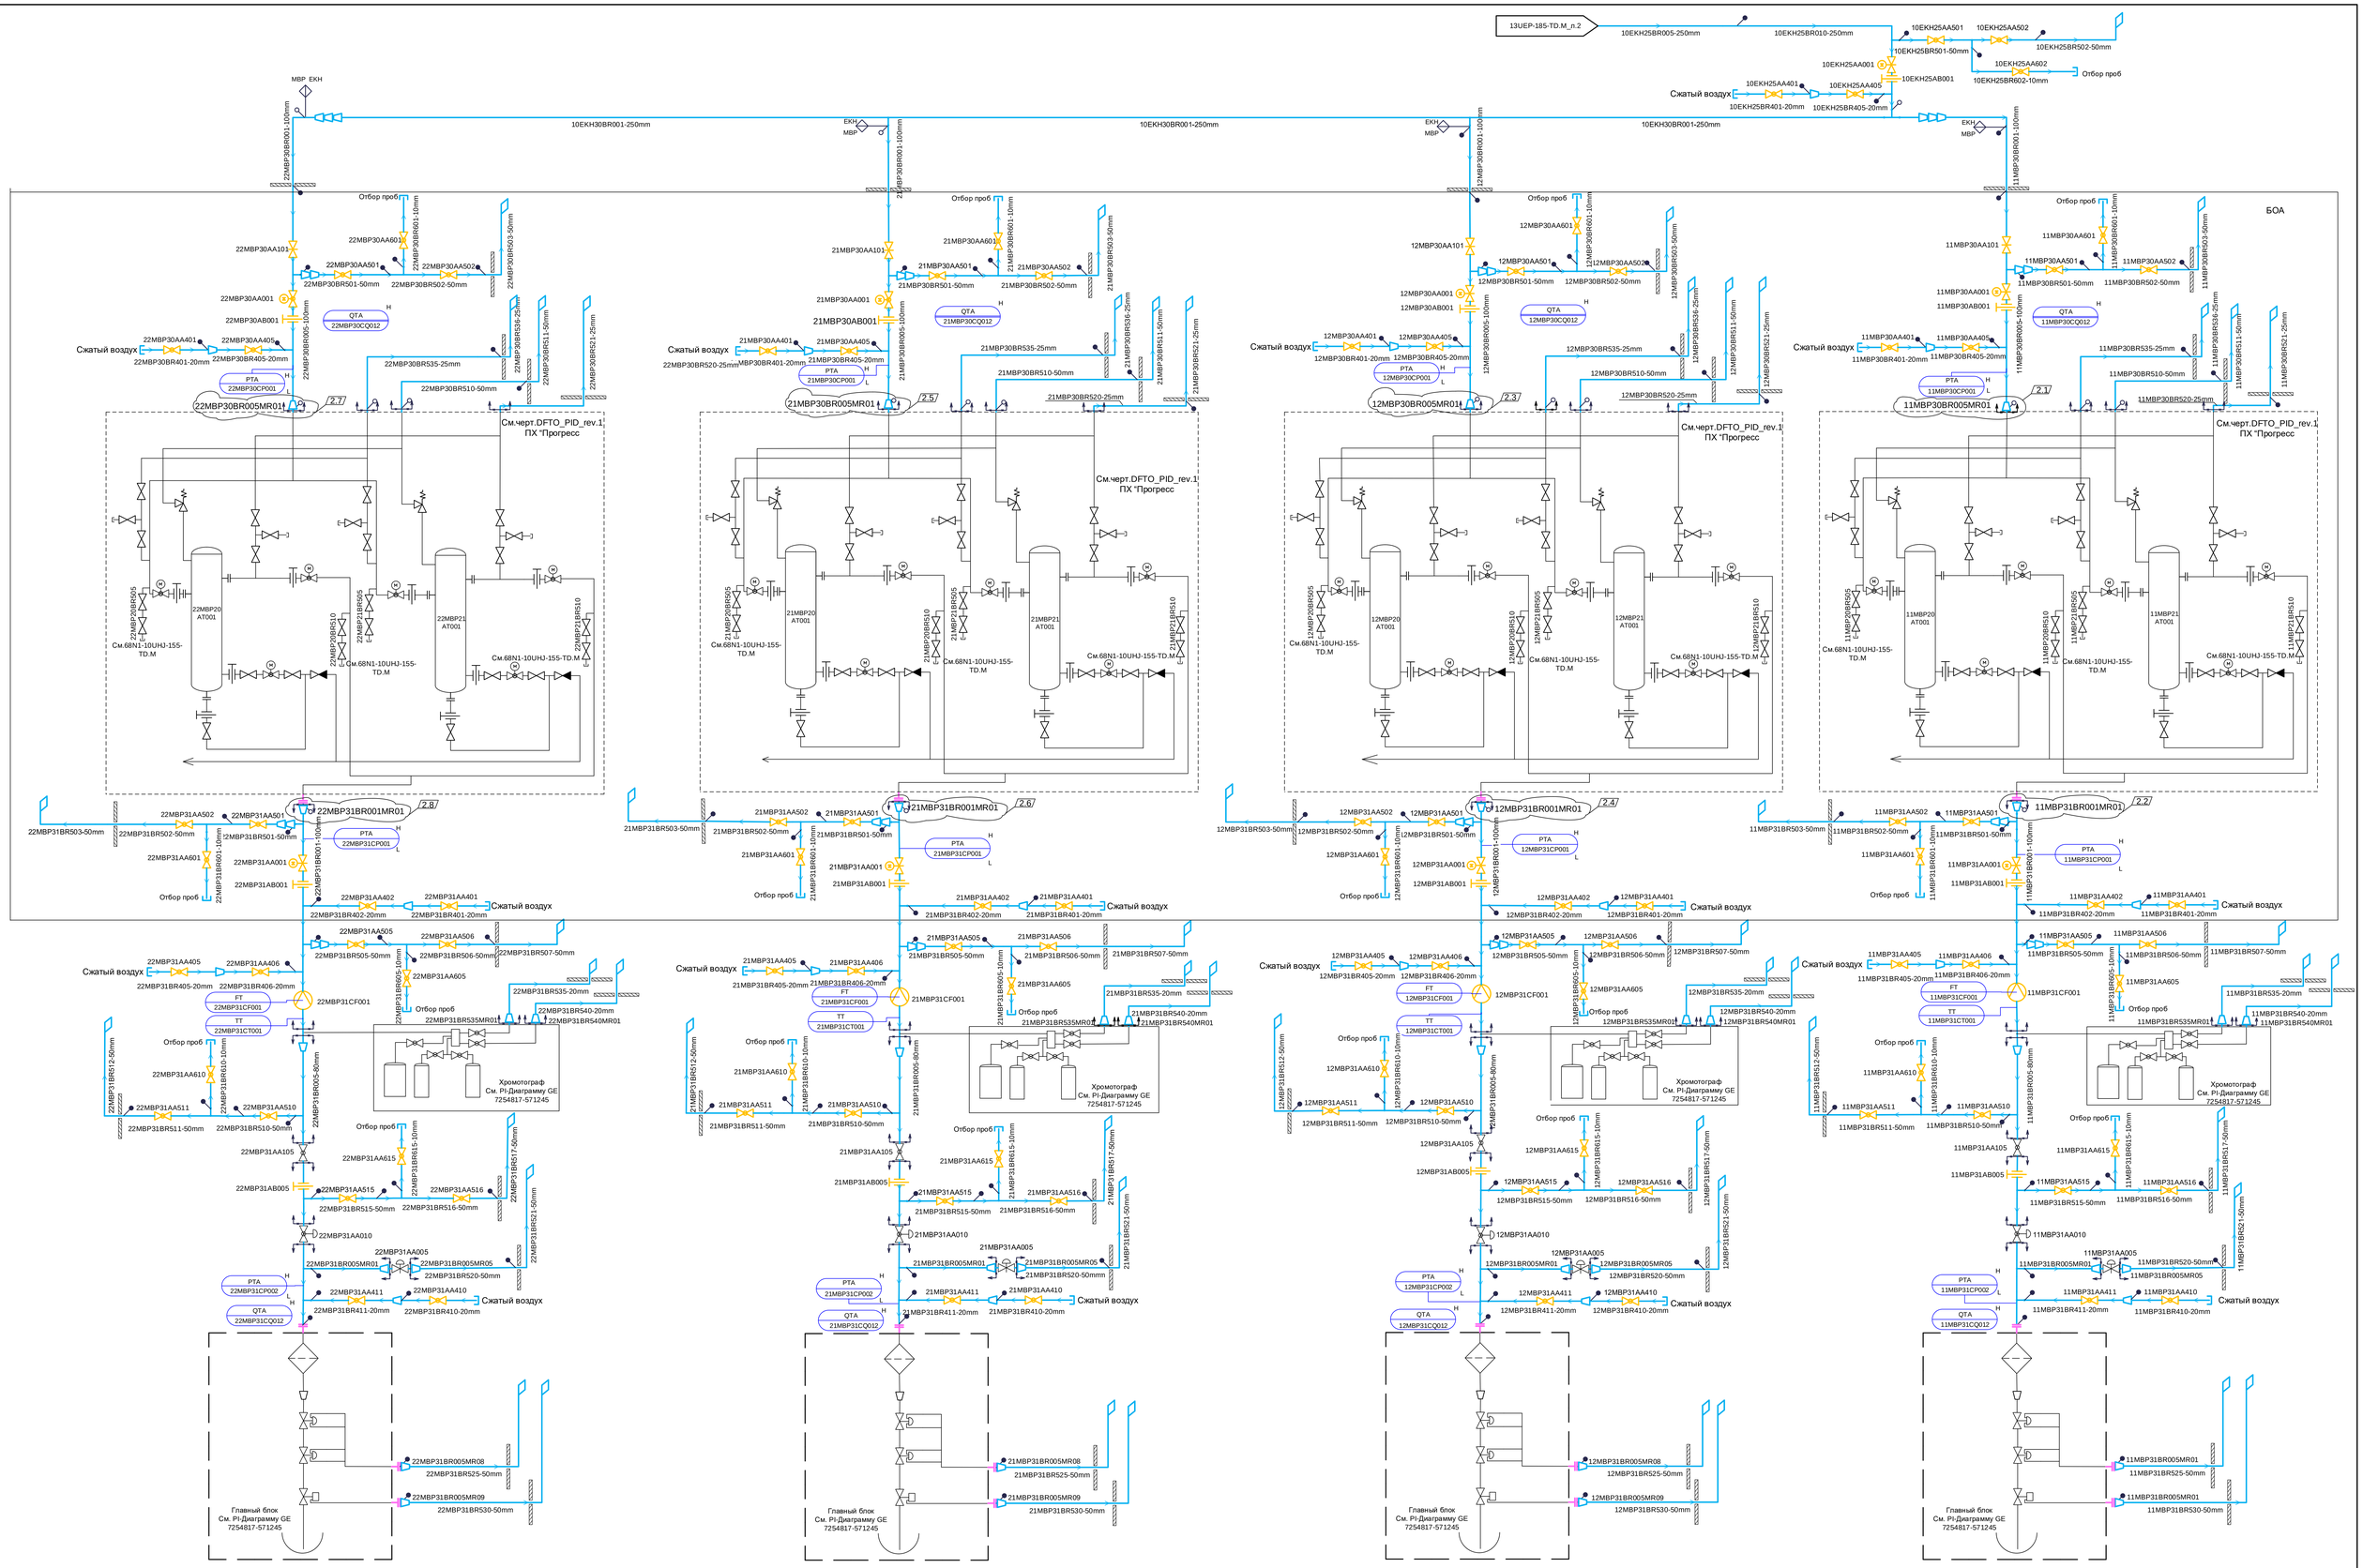

2	8	Зам	948-16				
Изм.	Кол.уч.	Лист	№ док.	Подп.	Дата		
Разработал		Полянская					
Проверил		Бобров					
Гл.спец.		Стацура					
Н. контр.		Астраханцев					

68N1-10UHJ-140-TD.M

Строительство Якутской ГРЭС-2

Главный корпус. PI-диаграмма трубопроводов газового топлива к ГТУ

Стадия	Лист	Листов
Р	2	

PI-диаграмма трубопроводов газового топлива к ГТУ. Система ЕКН, МВР

АКЦИОНЕРНОЕ ОБЩЕСТВО ТЕХНОЭКСПОРТНЕФТЕГАЗПРОЕКТ г. МОСКВА

Согласовано

Взам. инв. №

Подпись и дата

Инв. № подл.

Формат А0