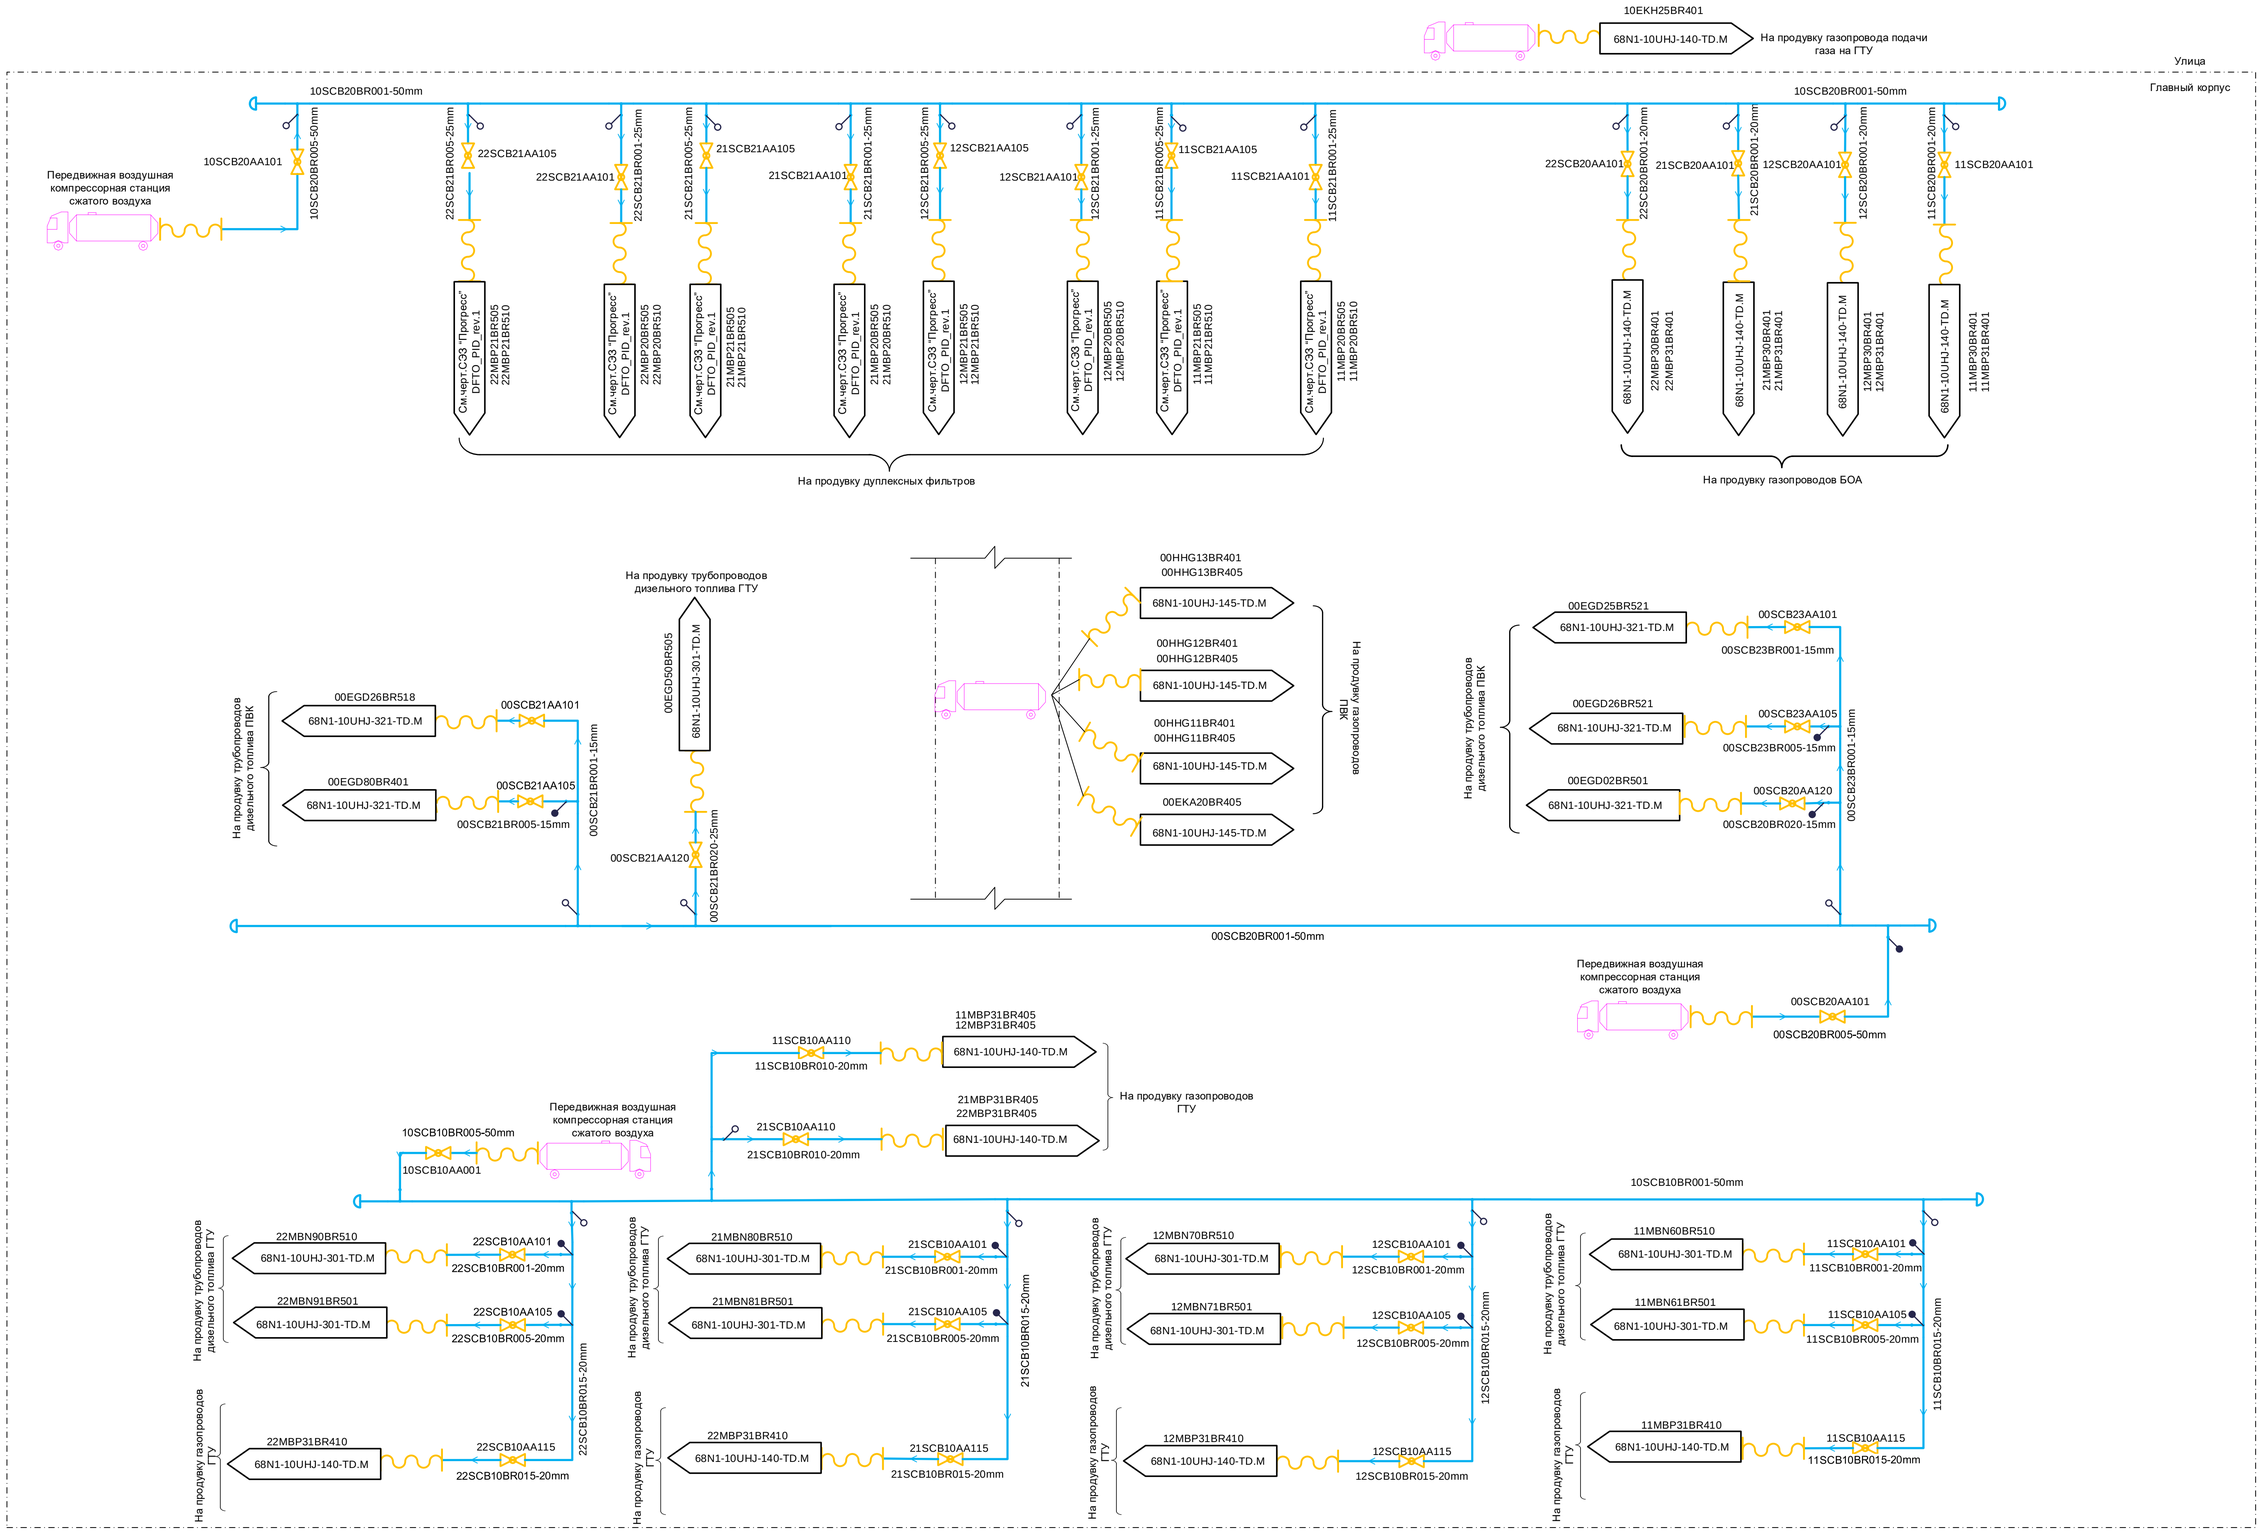

1	-	Зам	409-15		07.15	68N1 – 10UHJ – 155 – TD.M
Изм.	Кол.уч	Лист	№ док.	Подп.	Дата	Строительство Якутской ГРЭС-2
Разработал		Полянская			07.15	Главный корпус. PI-диаграмма сжатого воздуха на продувку газопроводов.
Проверил		Стацура			07.15	
Н. контр.		Астраханцев			07.15	PI-диаграмма сжатого воздуха на продувку газопроводов и трубопроводов дизельного топлива. Система SCB.

Стадия	Лист	Листов
Р	2	

АКЦИОНЕРНОЕ ОБЩЕСТВО ИНСТИТУТ ТЕПЛОЭЛЕКТРОПРОЕКТ Г. МОСКВА

Согласовано

Взам. инв. №

Подпись и дата

Инв. № подл.

Формат А1