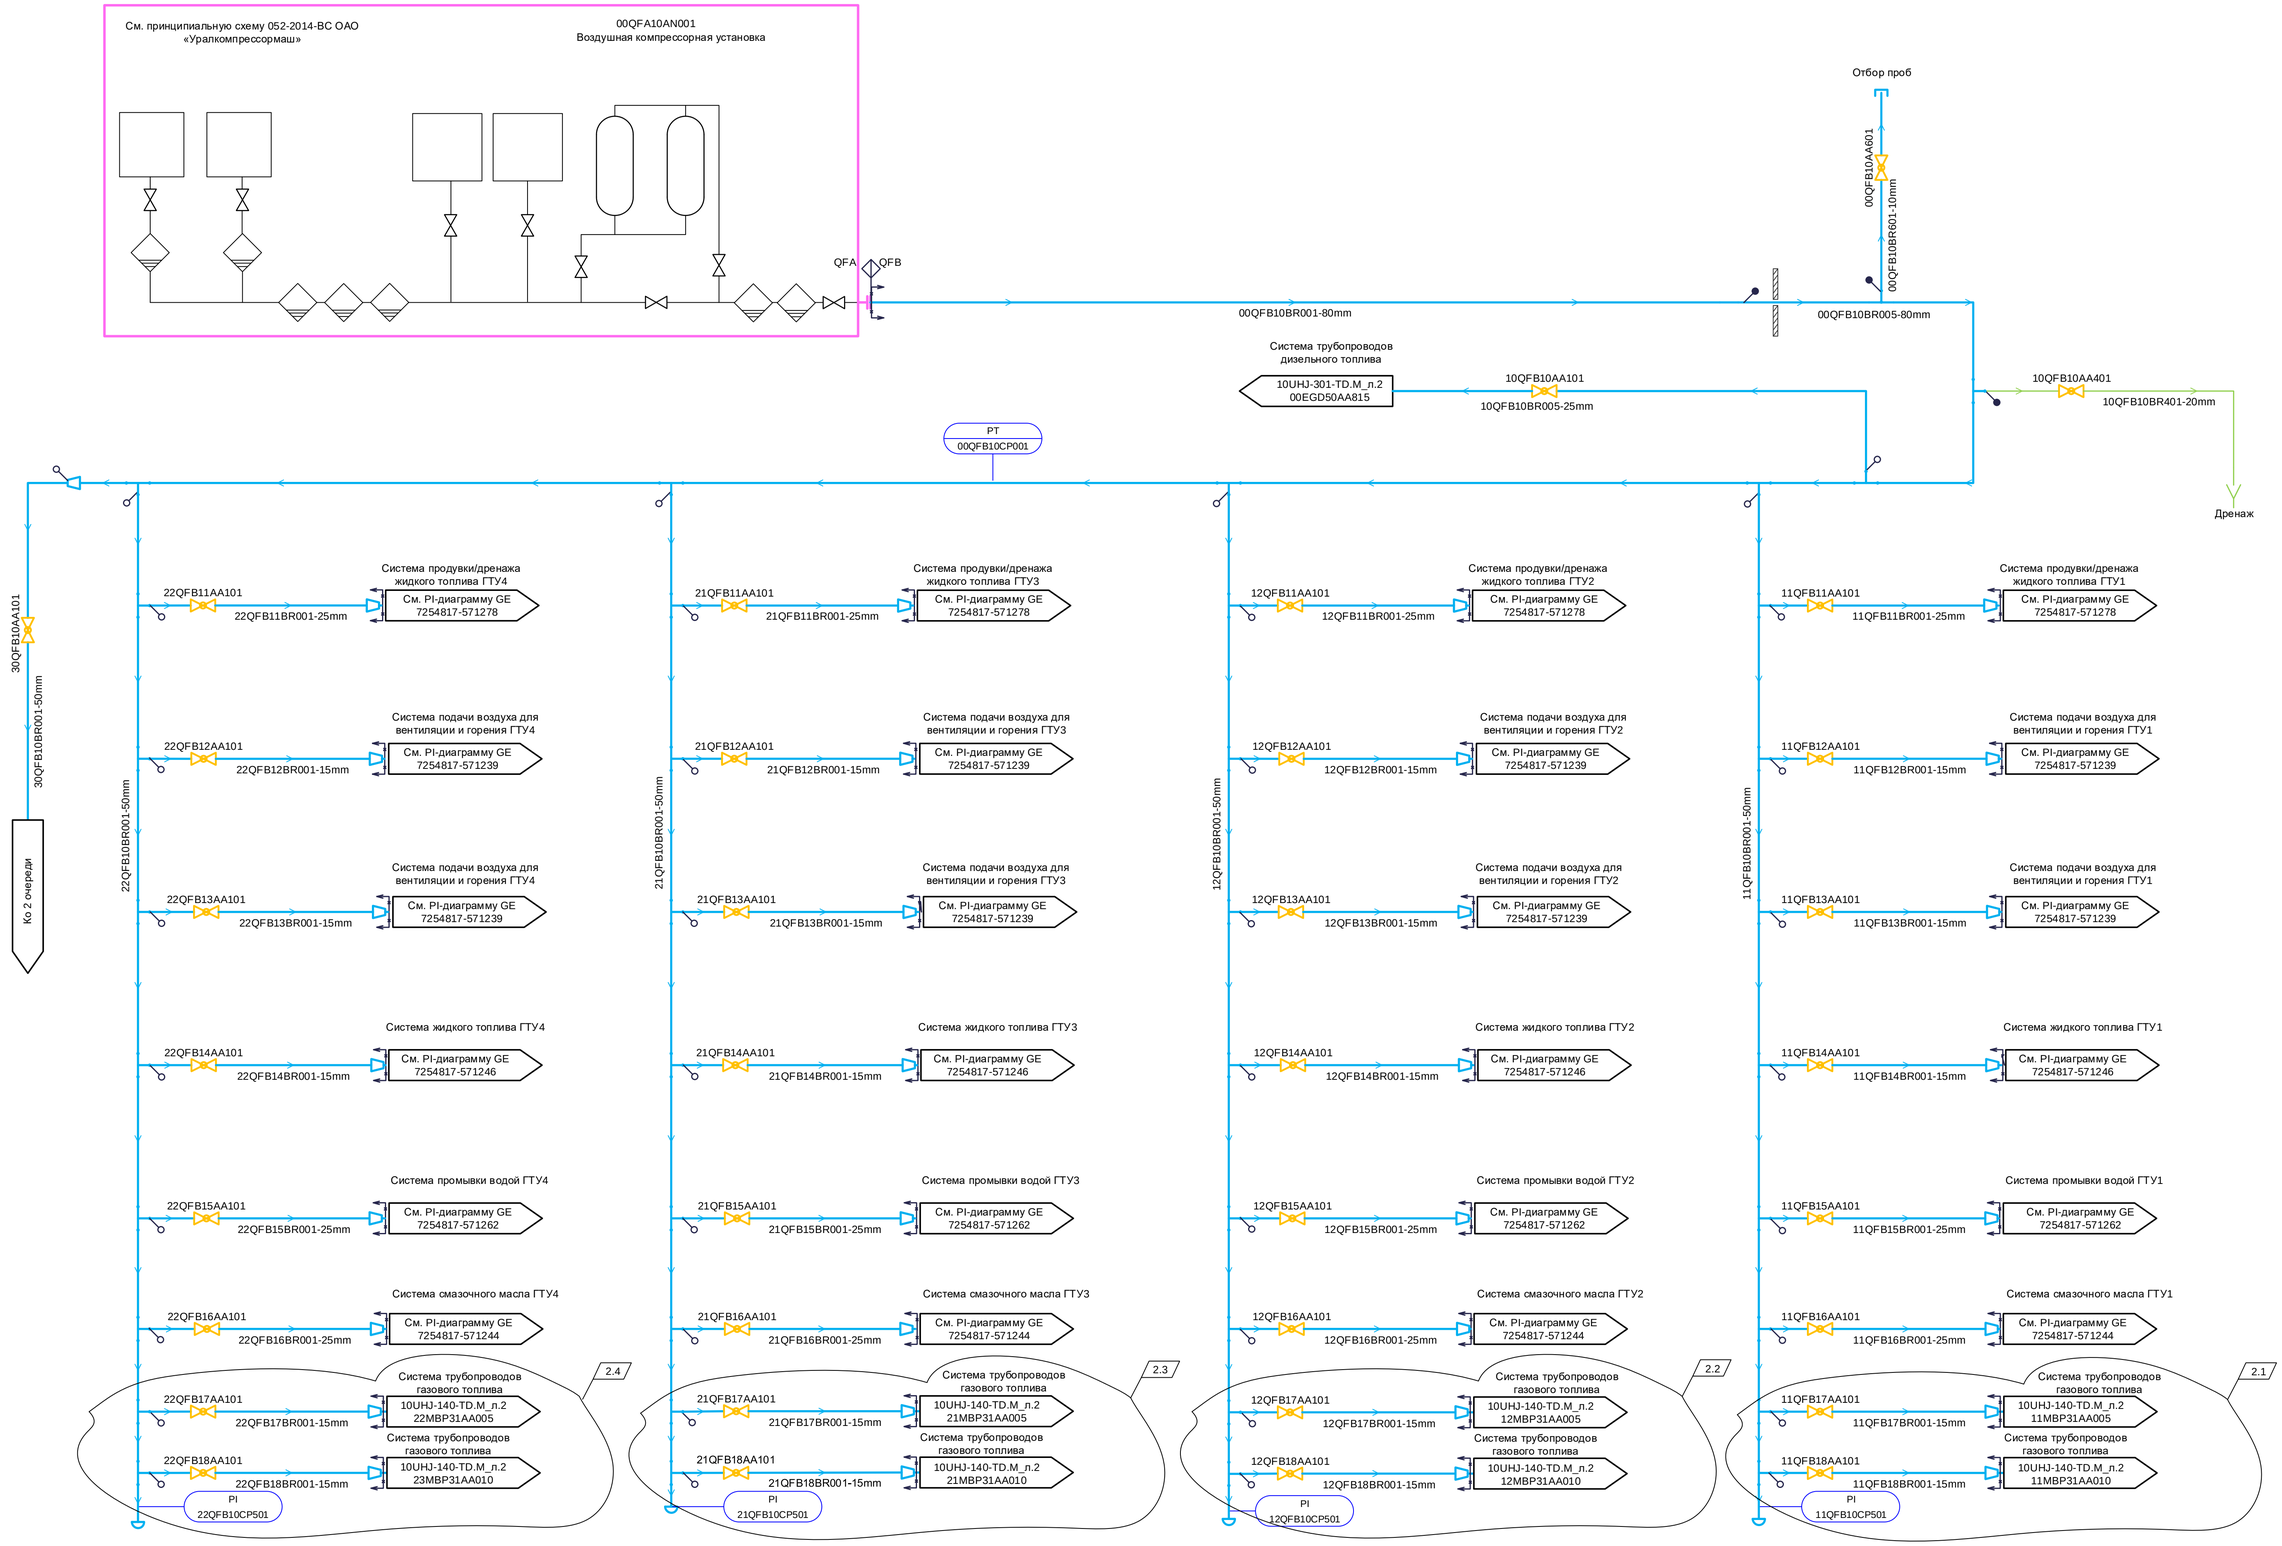

Примечание: Максимальное рабочее давление в трубопроводах инструментального сжатого воздуха не должно превышать 0,8МПа.

2	4	Зам.	886-15			68N1 – 10UHJ – 160 – TD.M
Изм.	Кол.уч	Лист	№ док.	Подп.	Дата	Строительство Якутской ГРЭС-2
Разработал		Дёмина				Главный корпус. PI-диаграмма трубопроводов инструментального сжатого воздуха
Проверил		Бобров				Стадия: Р; Лист: 2; Листов:
Гл. спец.		Стацура				
Н. контр.		Астраханцев				PI-диаграмма трубопроводов инструментального сжатого воздуха. Система QFA, QFB
						АКЦИОНЕРНОЕ ОБЩЕСТВО ИНСТИТУТ ТЕПЛОЭЛЕКТРОПРОЕКТ Г. МОСКВА

Согласовано

ОАСУ

Взам. инв. №

Подпись и дата

Инв. № подл.

Формат А1