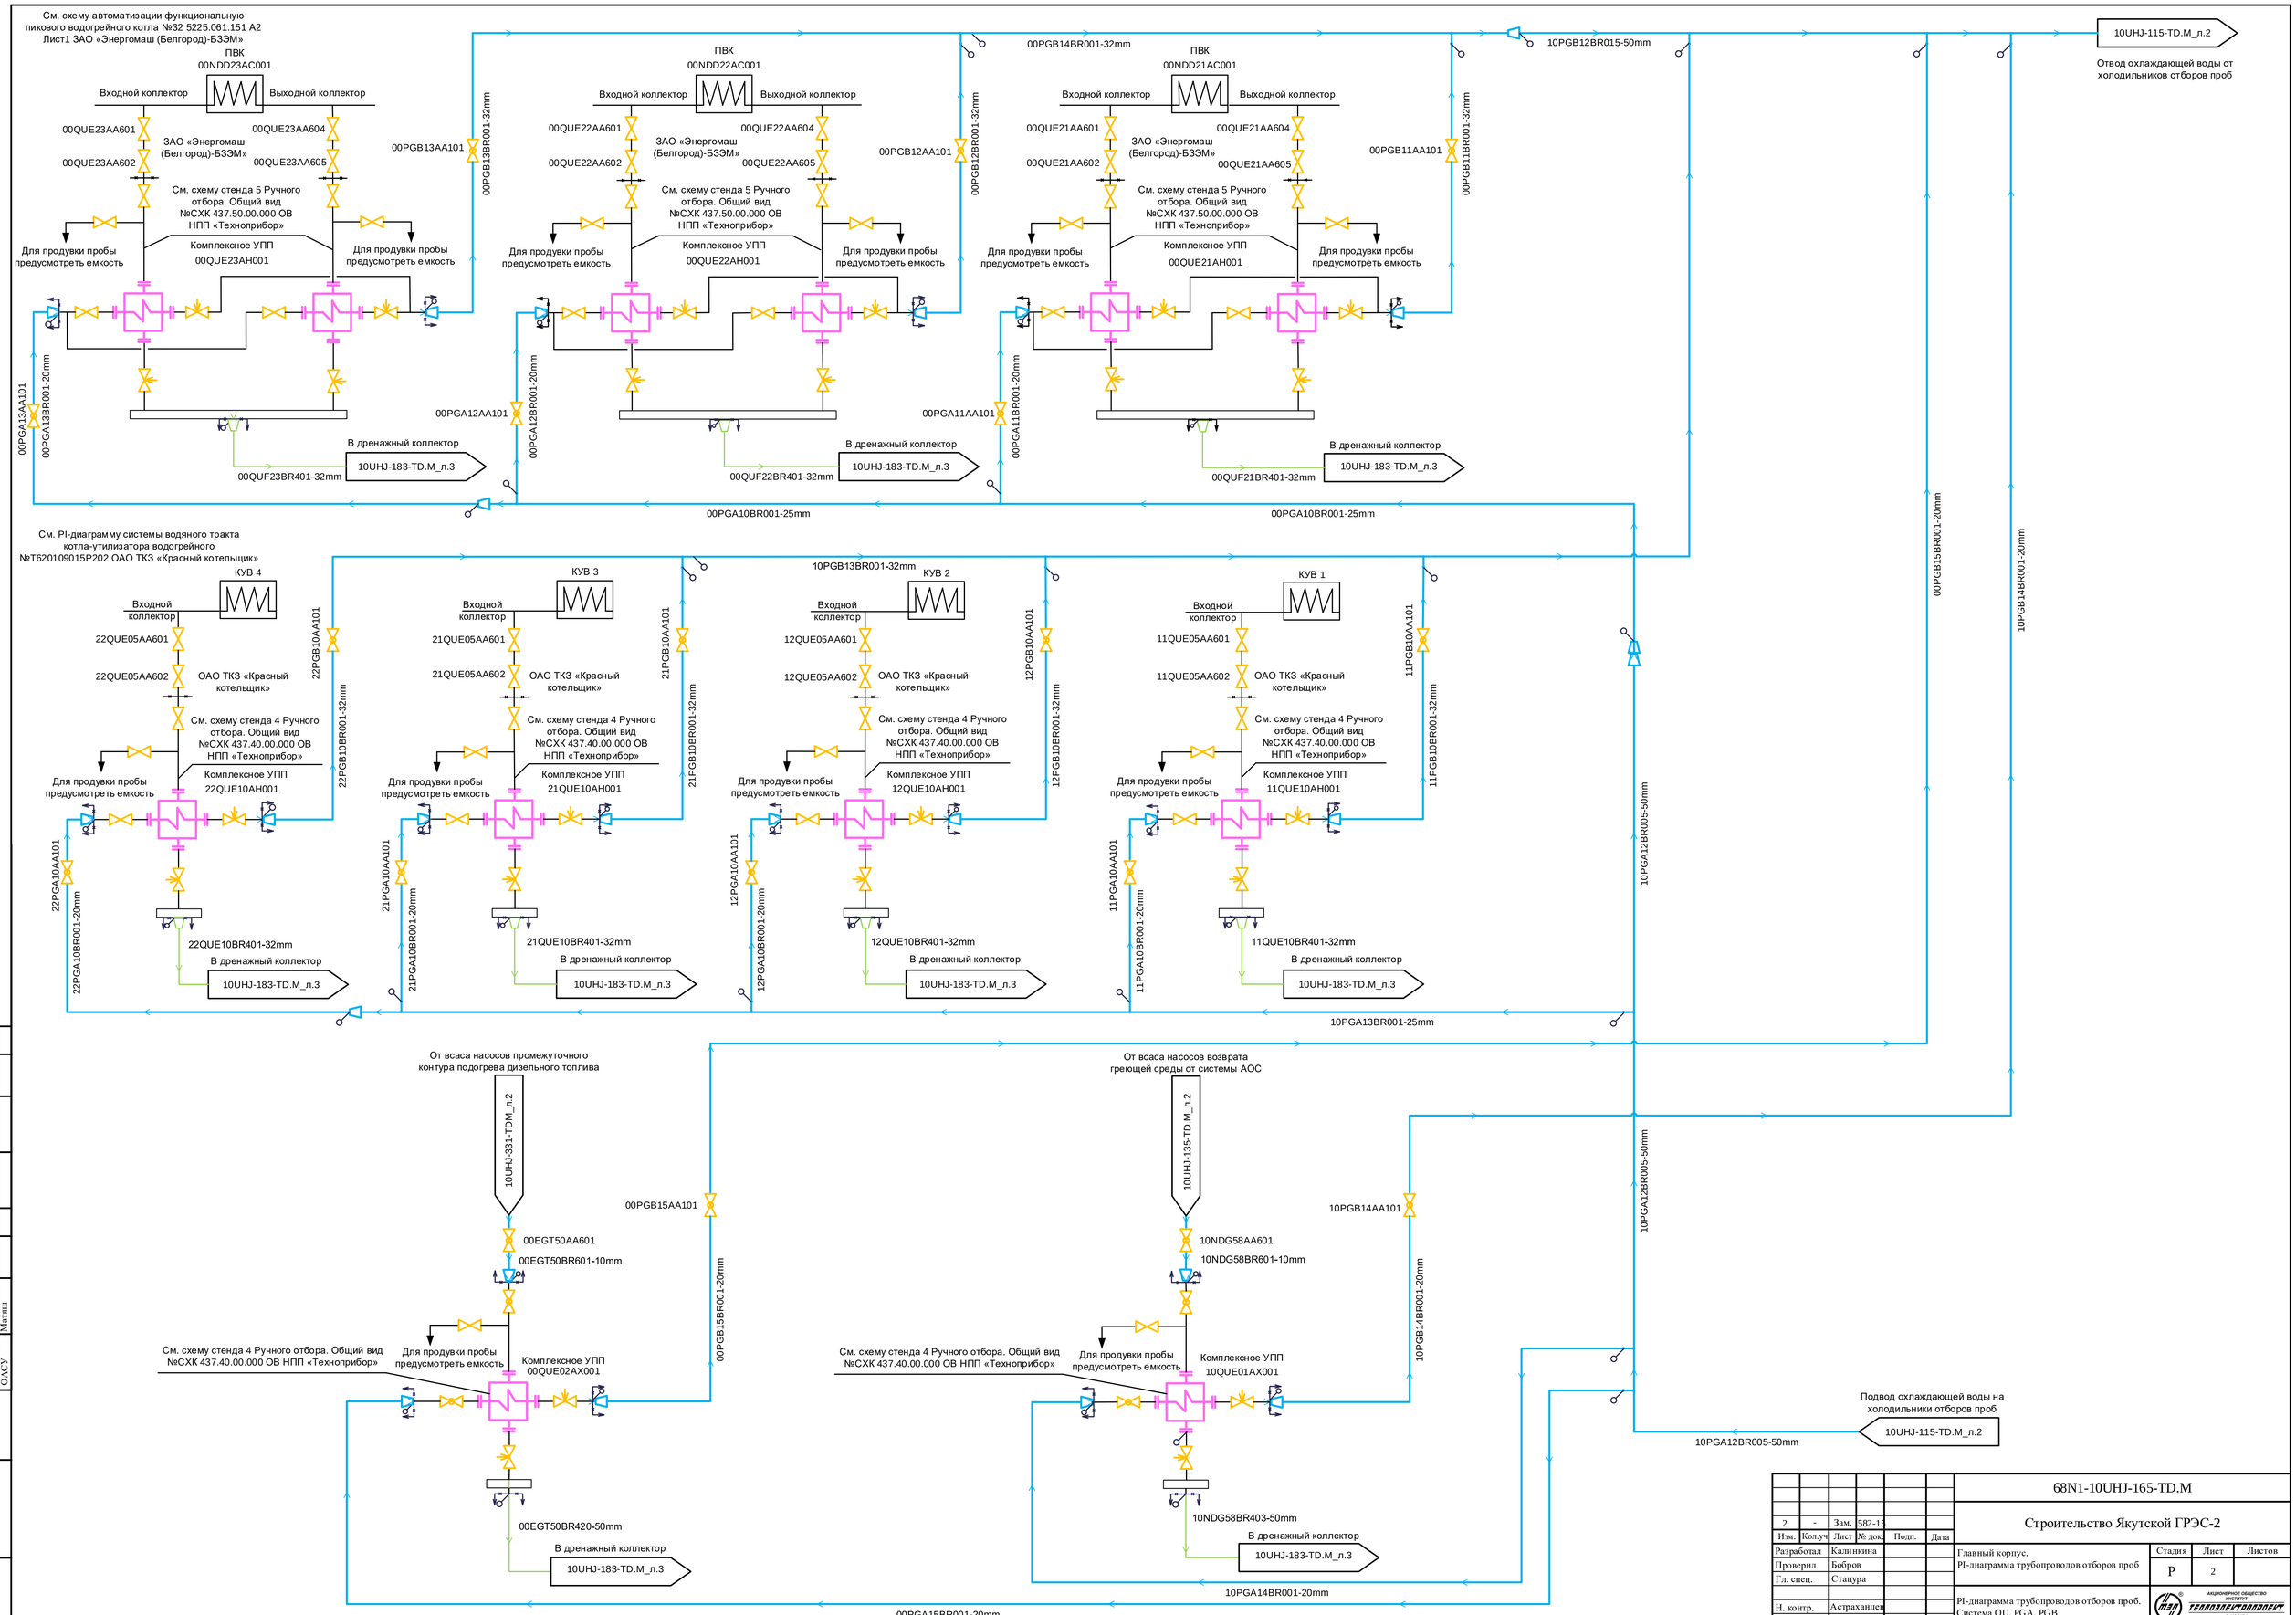
См. схему автоматизации функциональную пикового водогрейного котла №32 5225.061.151 А2 Лист1 ЗАО «Энергомаш (Белгород)-БЗЭМ»
ПВК 00NDD23AC001
Входной коллектор
Выходной коллектор
00QUE23AA601
00QUE23AA604
00QUE23AA602
00QUE23AA605
ЗАО «Энергомаш (Белгород)-БЗЭМ»
00PGB13AA101
00PGB13BR001-32mm
См. схему стенда 5 Ручного отбора. Общий вид №СХК 437.50.00.000 ОВ НПП «Техноприбор»
Комплексное УПП 00QUE23AH001
Для продувки пробы предусмотреть емкость
00PGA13AA101
00PGA13BR001-20mm
00PGA12AA101
00PGA12BR001-20mm
В дренажный коллектор
00QUF23BR401-32mm
10UHJ-183-TD.M_л.3
ПВК 00NDD22AC001
00QUE22AA601
00QUE22AA604
00QUE22AA602
00QUE22AA605
00PGB12AA101
00PGB12BR001-32mm
Комплексное УПП 00QUE22AH001
00QUF22BR401-32mm
00PGB14BR001-32mm
ПВК 00NDD21AC001
00QUE21AA601
00QUE21AA604
00QUE21AA602
00QUE21AA605
00PGB11AA101
00PGB11BR001-32mm
Комплексное УПП 00QUE21AH001
00PGA11AA101
00PGA11BR001-20mm
00QUF21BR401-32mm
00PGA10BR001-25mm
10PGB12BR015-50mm
10UHJ-115-TD.M_л.2
Отвод охлаждающей воды от холодильников отборов проб
00PGB15BR001-20mm
10PGB14BR001-20mm
См. PI-диаграмму системы водяного тракта котла-утилизатора водогрейного №Т62010915Р202 ОАО ТКЗ «Красный котельщик»
КУВ 4
Входной коллектор
22QUE05AA601
22QUE05AA602
ОАО ТКЗ «Красный котельщик»
22PGB10AA101
22PGB10BR001-32mm
См. схему стенда 4 Ручного отбора. Общий вид №СХК 437.40.00.000 ОВ НПП «Техноприбор»
Комплексное УПП 22QUE10AH001
22PGA10AA101
22PGA10BR001-20mm
22QUE10BR401-32mm
КУВ 3
21QUE05AA601
21QUE05AA602
21PGB10AA101
21PGB10BR001-32mm
Комплексное УПП 21QUE10AH001
21PGA10AA101
21PGA10BR001-20mm
21QUE10BR401-32mm
10PGB13BR001-32mm
КУВ 2
12QUE05AA601
12QUE05AA602
12PGB10AA101
12PGB10BR001-32mm
Комплексное УПП 12QUE10AH001
12PGA10AA101
12PGA10BR001-20mm
12QUE10BR401-32mm
КУВ 1
11QUE05AA601
11QUE05AA602
11PGB10AA101
11PGB10BR001-32mm
Комплексное УПП 11QUE10AH001
11PGA10AA101
11PGA10BR001-20mm
11QUE10BR401-32mm
10PGA13BR001-25mm
10PGA12BR005-50mm
От всаса насосов промежуточного контура подогрева дизельного топлива
10UHJ-331-TDM_л.2
00PGB15AA101
00EGT50AA601
00EGT50BR601-10mm
См. схему стенда 4 Ручного отбора. Общий вид №СХК 437.40.00.000 ОВ НПП «Техноприбор»
Комплексное УПП 00QUE02AX001
00EGT50BR420-50mm
От всаса насосов возврата греющей среды от системы АОС
10UHJ-135-TD.M_л.2
10PGB14AA101
10NDG58AA601
10NDG58BR601-10mm
Комплексное УПП 10QUE01AX001
10NDG58BR403-50mm
10PGA14BR001-20mm
00PGA15BR001-20mm
Подвод охлаждающей воды на холодильники отборов проб
10UHJ-115-TD.M_л.2
10PGA12BR005-50mm
Согласовано
ОАСУ
Матяш
Взам. инв. №
Подпись и дата
Инв. № подл.
68N1-10UHJ-165-TD.M
Строительство Якутской ГРЭС-2
2
-
Зам.
582-13
Изм.
Кол.уч
Лист
№ док.
Подп.
Дата
Разработал
Калинкина
Проверил
Бобров
Гл. спец.
Стацура
Н. контр.
Астраханцев
Главный корпус. PI-диаграмма трубопроводов отборов проб
Стадия
Лист
Листов
Р
2
PI-диаграмма трубопроводов отборов проб. Система QU, PGA, PGB
АКЦИОНЕРНОЕ ОБЩЕСТВО ИНСТИТУТ ТЕПЛОЭЛЕКТРОПРОЕКТ Г. МОСКВА
Формат А1