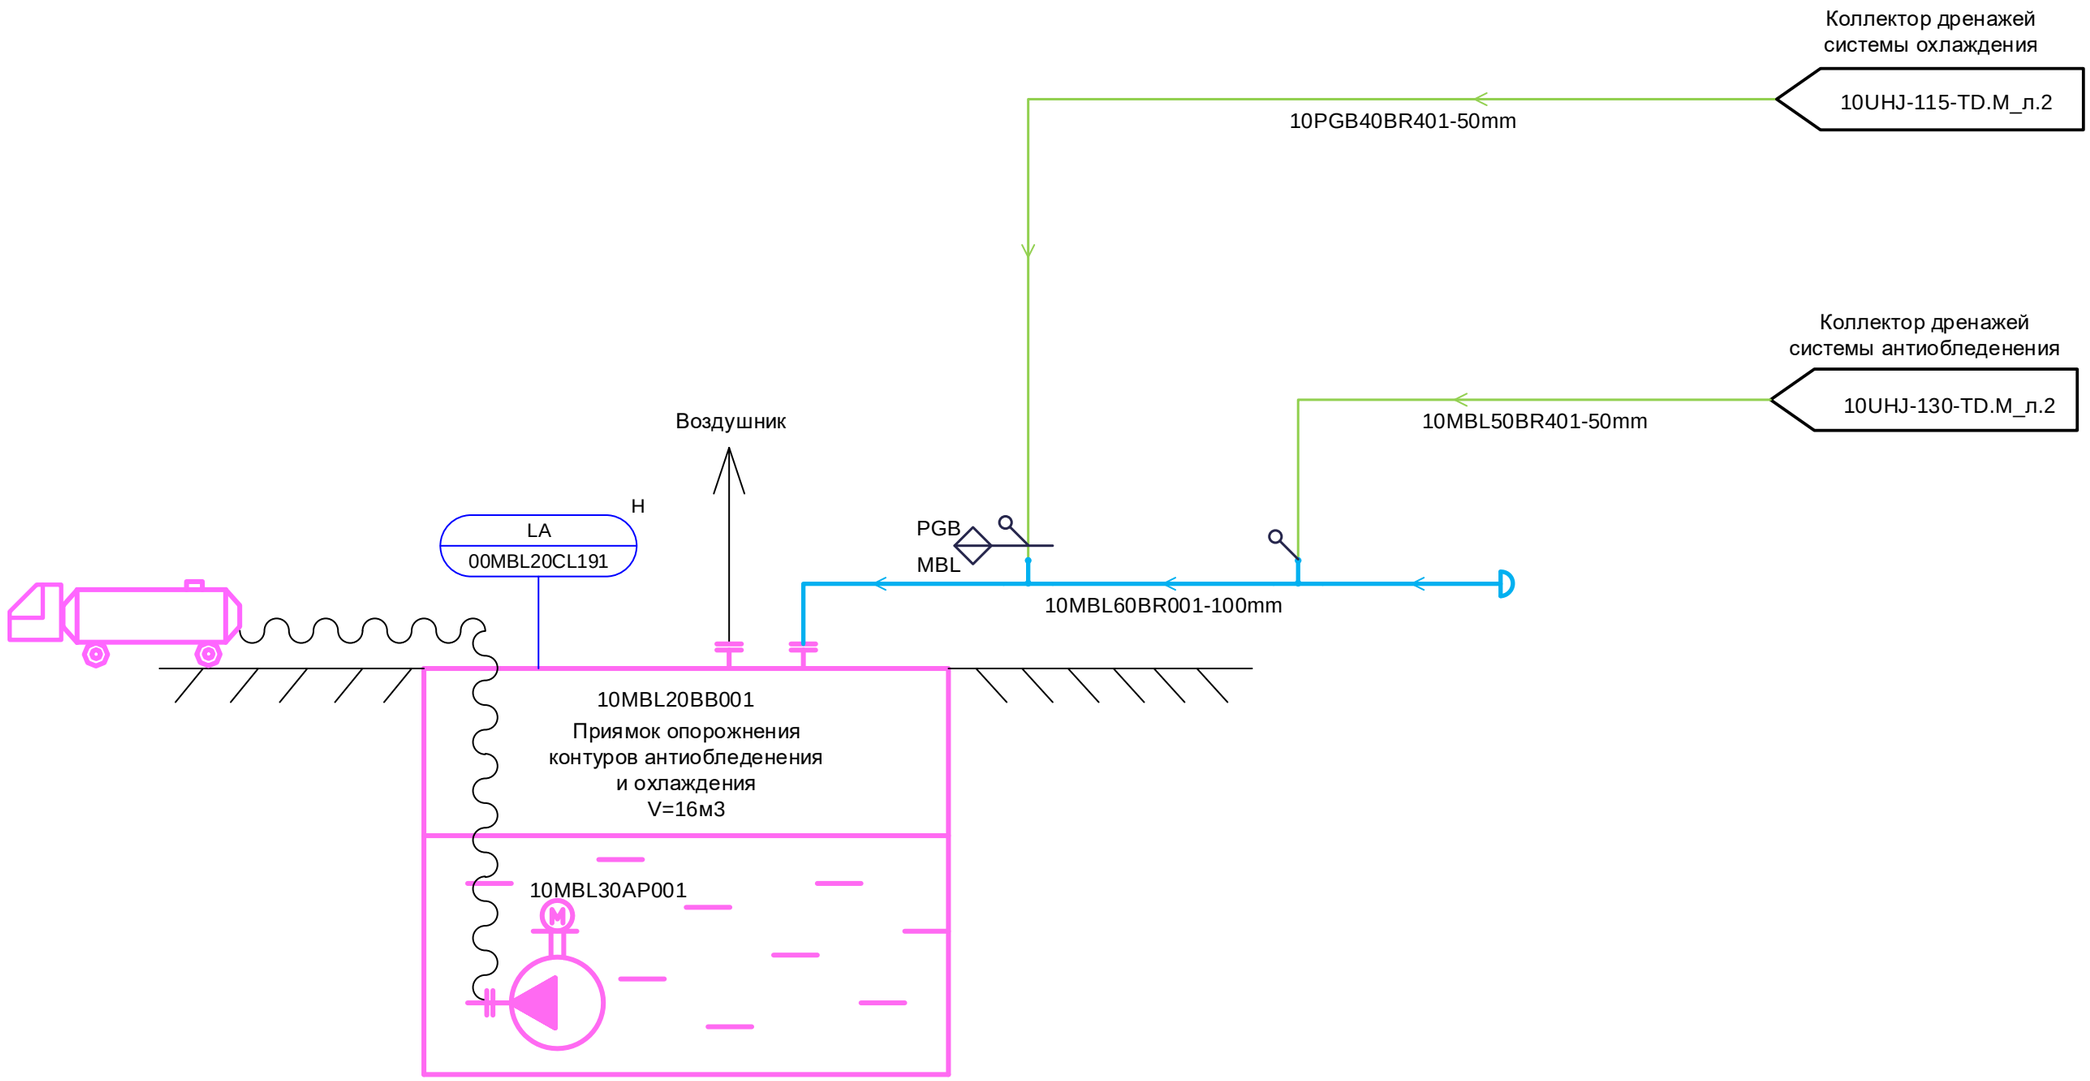


Примечание: Насос 10MBL30AP001 управляется по месту.

Согласовано

Взам. инв. №

Подпись и дата

Инв. № подл.

| Изм. | Кол.уч | Лист | № док. | Подп. | Дата |
|---|---|---|---|---|---|
| Разработал | | Дёмина | | | |
| Проверил | | Бобров | | | |
| Гл. спец. | | Стацура | | | |
| Н. контр. | | Астраханцев | | | |

68N1 – 10UHJ – 170 – TD.M

Строительство Якутской ГРЭС-2

Главный корпус. Трубопроводы дренажной системы антиобледенения и охлаждения. PI-диаграмма.

| Стадия | Лист | Листов |
|---|---|---|
| Р | 2 | |

PI-диаграмма трубопроводов дренажной системы антиобледенения и охлаждения. Система MBL.

АКЦИОНЕРНОЕ ОБЩЕСТВО ИНСТИТУТ ТЕПЛОЭЛЕКТРОПРОЕКТ Г. МОСКВА

Формат А3