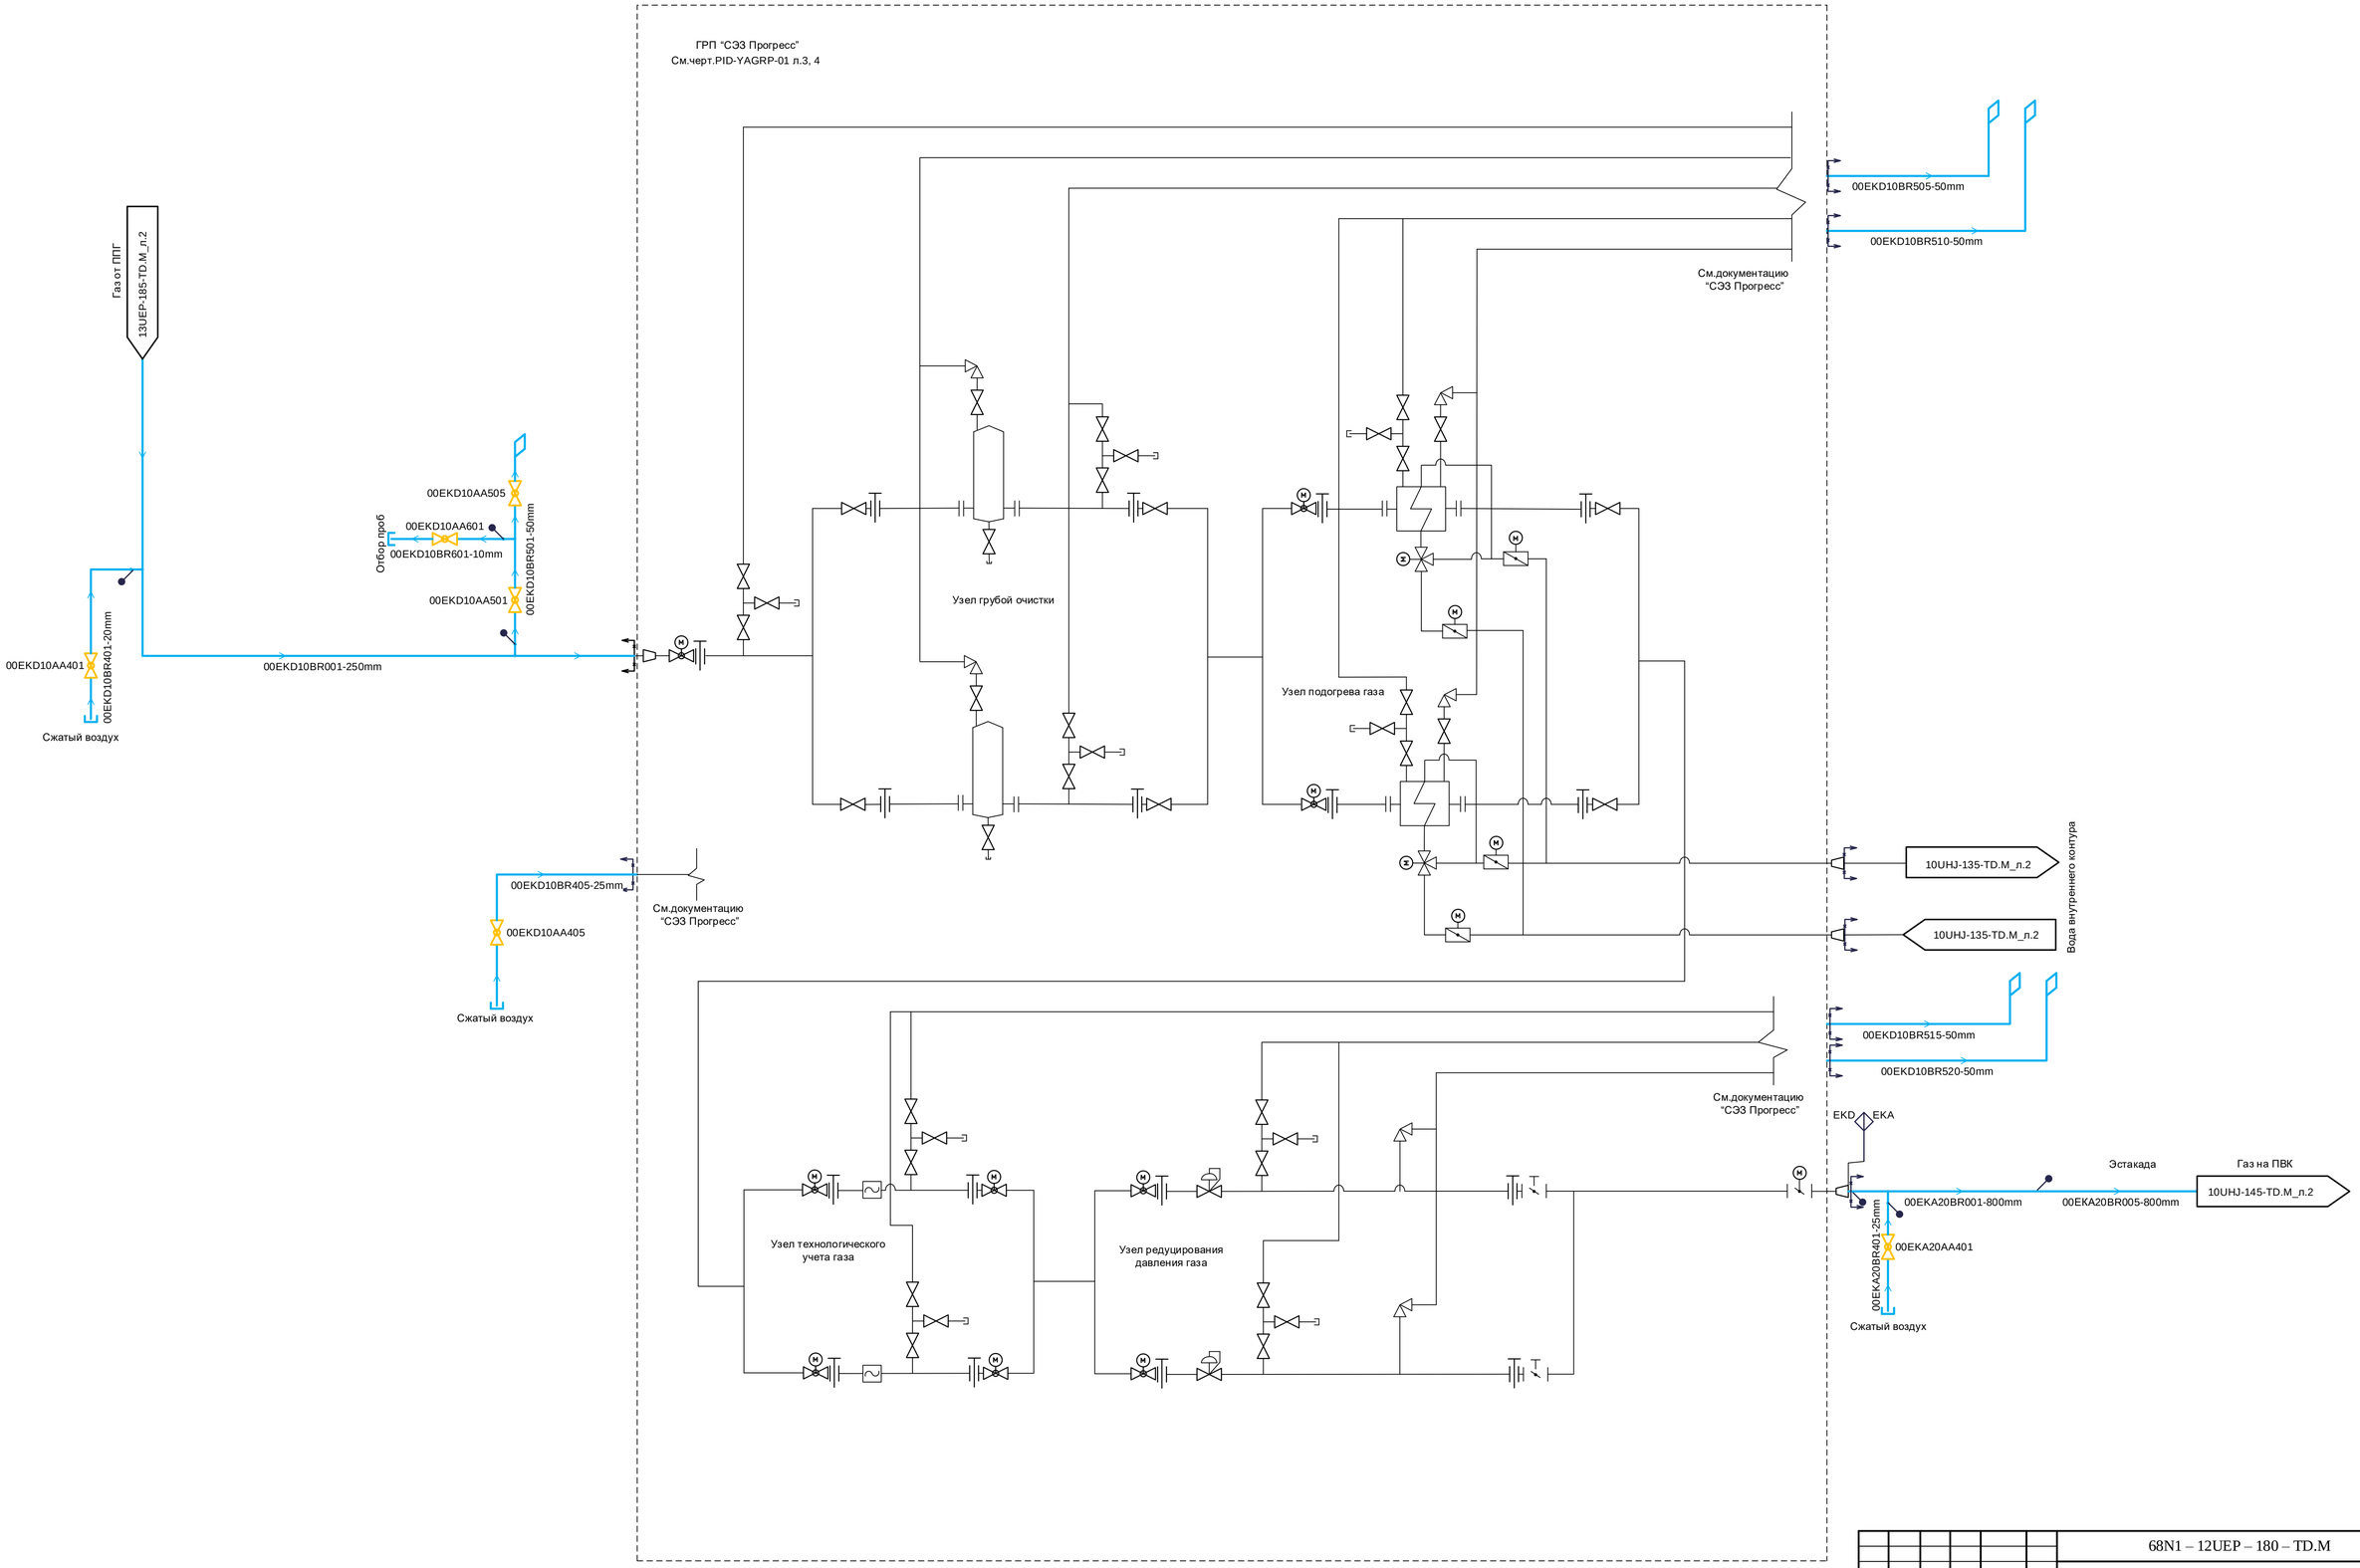

1	-	Зам	333-15		05.15	68N1 – 12UEP – 180 – TD.M
Изм.	Кол.уч	Лист	№ док.	Подп.	Дата	Строительство Якутской ГРЭС-2
Разработал		Полянская				Газовое хозяйство. Газопроводы ГРП
Проверил		Попова				Стадия: Р; Лист: 2; Листов:
Гл.спец.		Станцура				PI-Диаграмма газопроводов ГРП. Системы EKA, EKD
Н. контр.		Гридчина				АКЦИОНЕРНОЕ ОБЩЕСТВО ИНСТИТУТ ТЕПЛОЭЛЕКТРОПРОЕКТ г. МОСКВА

Согласовано

Взам. инв. №

Подпись и дата

Инв. № подл.

Формат А1