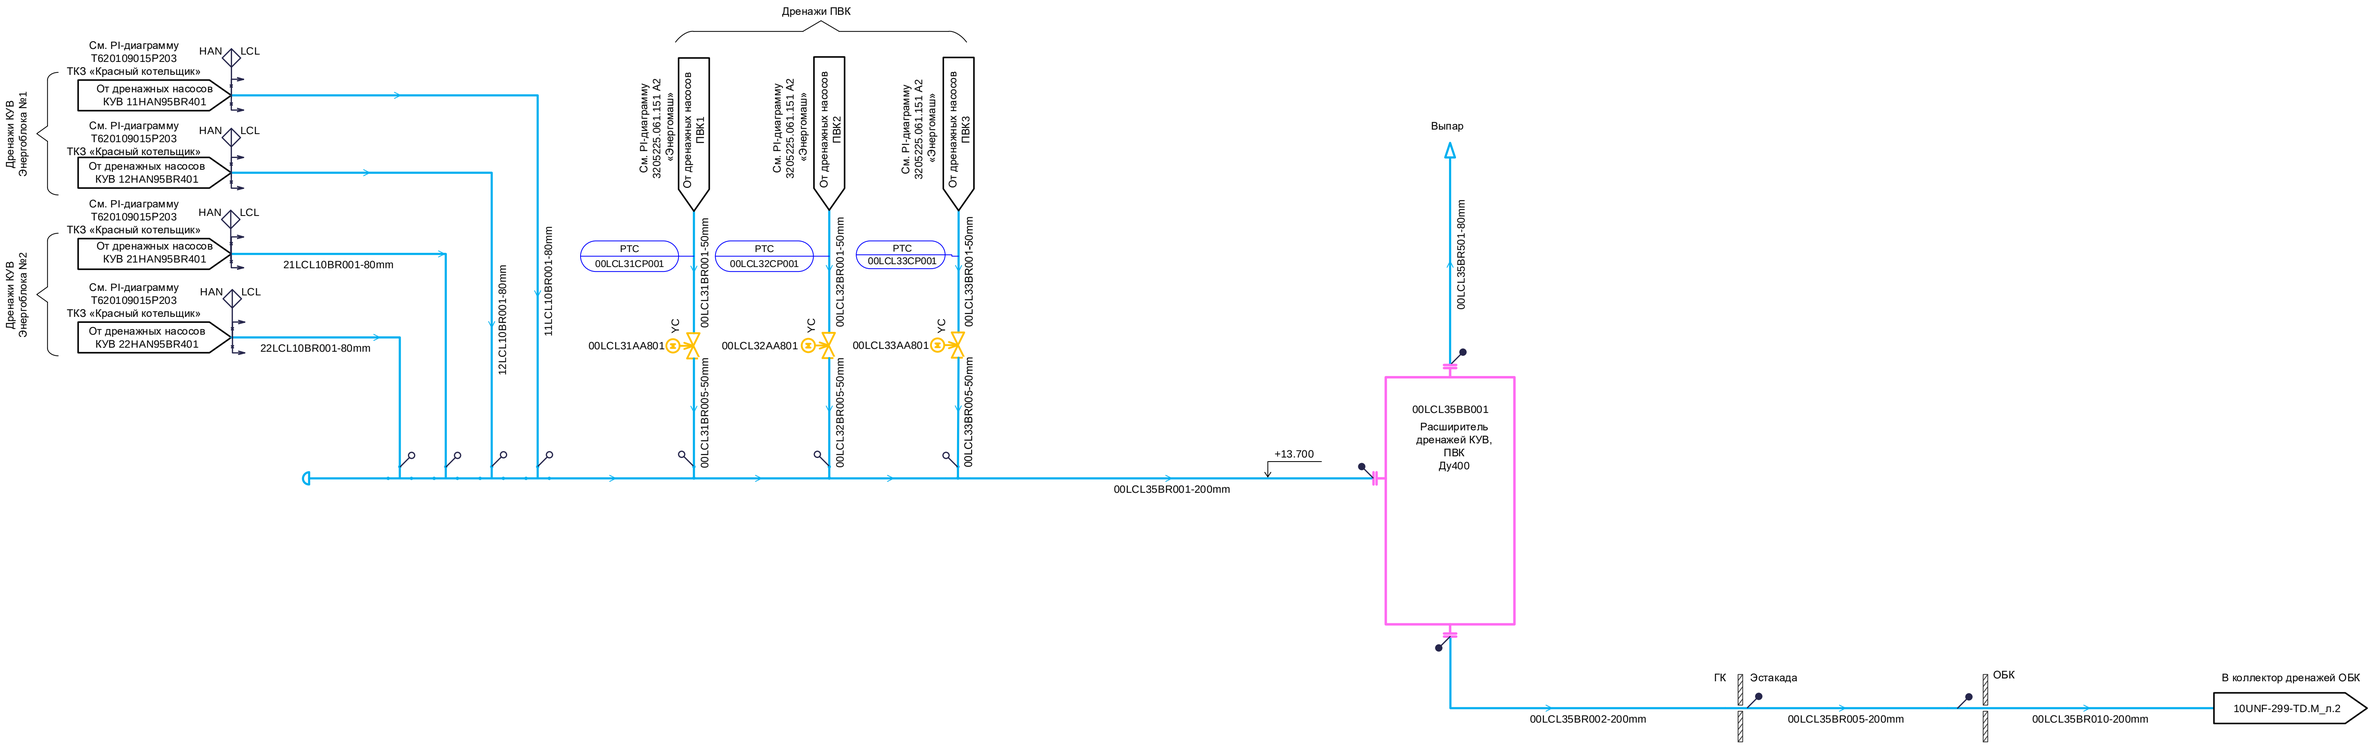

Примечание.

Управление регулирующими клапанами 00LCL31AA801, 00LCL32AA801, 00LCL33AA801 на напоре дренажных насосов ПВК:

Управление – оператором через ПТК и по алгоритмам технологического авторегулирования.

Регулирование давления 00LCL31CP001 (00LCL32CP001, 00LCL33CP001) «до себя» в напорном коллекторе дренажных насосов бака слива из ПВК1 (ПВК2, ПВК3) осуществляется регулятором, воздействующим на РК 00LCL31AA801 (00LCL32AA801, 00LCL33AA801). Задание – 0,40 МПа (уточняется при пусконаладочных работах).

						68N1 – 10UHJ – 183 – TD.M			
3	1	Зам	986-16			Строительство Якутской ГРЭС-2			
Изм.	Кол.уч	Лист	№ док.	Подп.	Дата				
Разработал		Дёмина				Главный корпус. Трубопроводы дренажей КУВ, ПВК. PI-диаграмма	Стадия	Лист	Листов
Проверил		Бобров					Р	2	
Гл. спец.		Стацура							
Н. контр.		Астраханцев				PI-диаграмма трубопроводов дренажей КУВ, ПВК. Система LCL.	АКЦИОНЕРНОЕ ОБЩЕСТВО ИНСТИТУТ ТЕПЛОЭЛЕКТРОПРОЕКТ Г. МОСКВА		

Согласовано

Взам. инв. №

Подпись и дата

Инв. № подл.

Формат А1