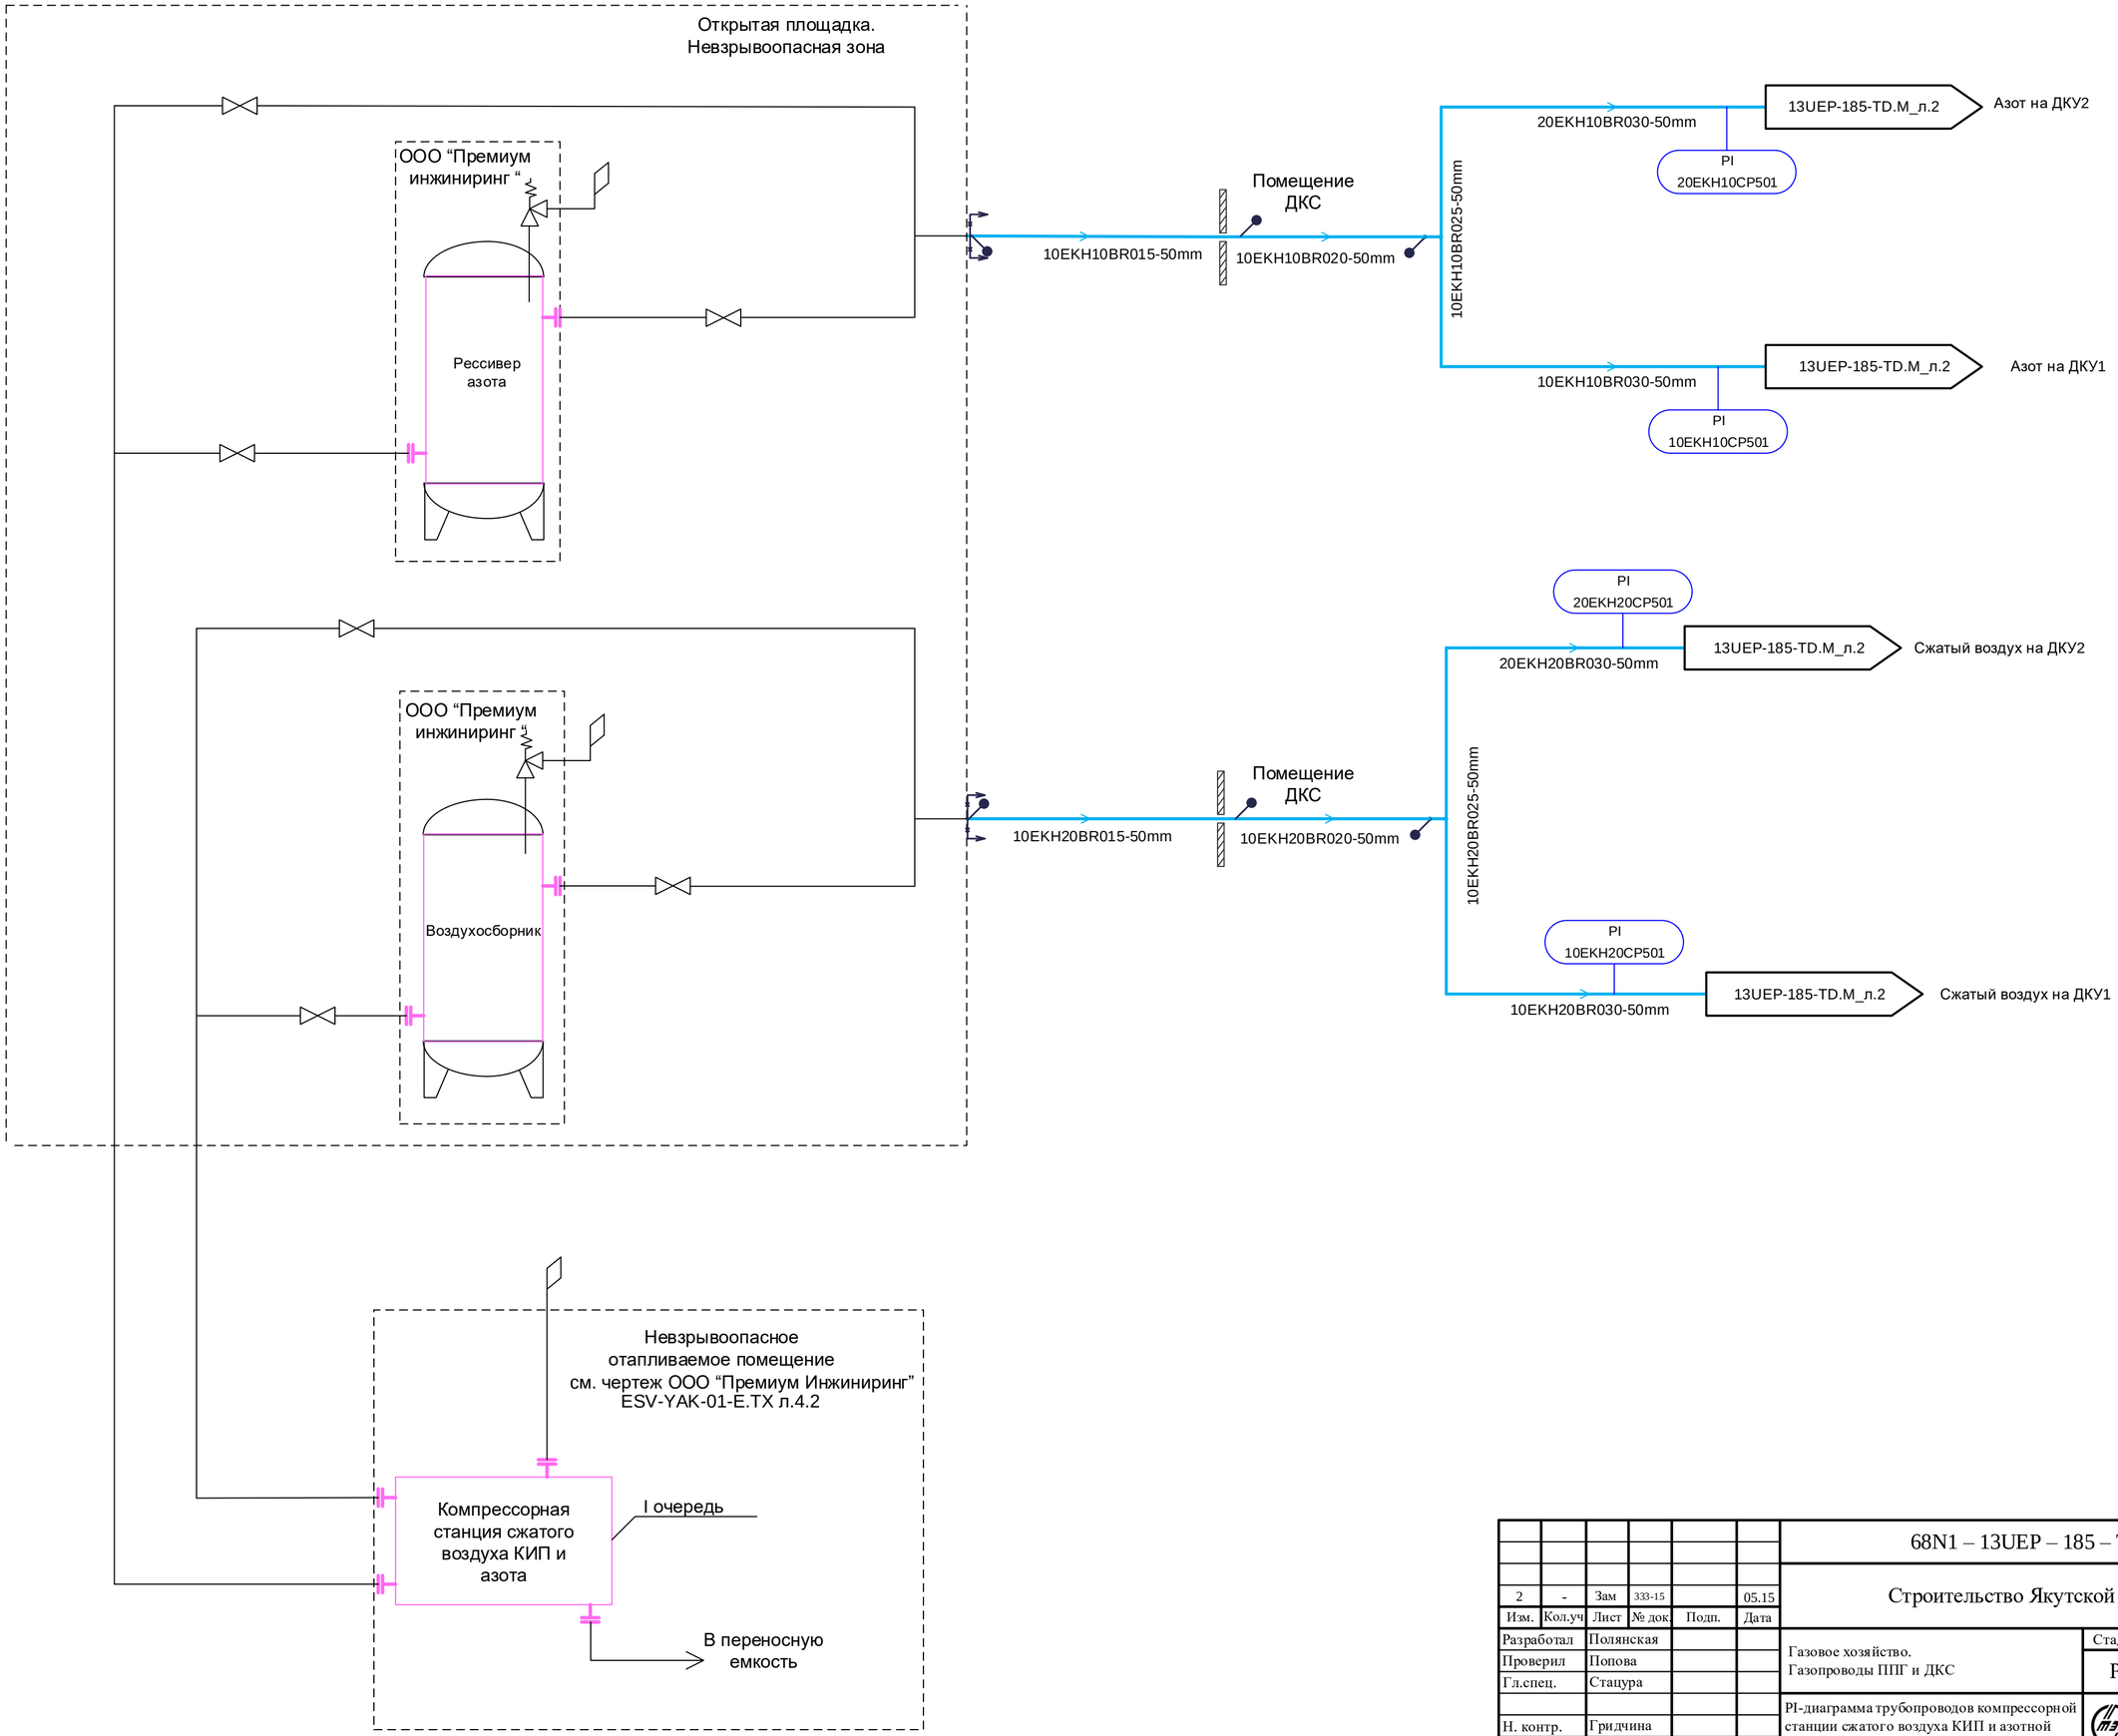

Согласовано

Взам. инв. №

Подпись и дата

Инв. № подл.

2	-	Зам	333-15		05.15	
Изм.	Кол.уч	Лист	№ док.	Подп.	Дата	
Разработал		Полянская				
Проверил		Попова				
Гл.спец.		Стацура				
Н. контр.		Гридчина				

68N1 – 13UEP – 185 – TD.M

Строительство Якутской ГРЭС-2

Газовое хозяйство.
Газопроводы ППГ и ДКС

Стадия	Лист	Листов
Р	3	

PI-диаграмма трубопроводов компрессорной станции сжатого воздуха КИП и азотной станции.

АКЦИОНЕРНОЕ ОБЩЕСТВО ИНСТИТУТ ТЕПЛОЭЛЕКТРОПРОЕКТ Г. МОСКВА

Формат А2